

ДИЗЙН ПРОЕКТ

АВТОРСКИЙ

ЖК АКВИЛОН BESIDE
РЯЗАНСКИЙ ПРОСПЕКТ
Д. 2/2, КВ. 177



Лист	Наименование	Примечание
01	ОБЛОЖКА	
02	ВЕДОМОСТЬ ЧЕРТЕЖЕЙ	
03	ПОЯСНИТЕЛЬНАЯ ЗАПИСКА	
04	ОБМЕРНЫЙ ПЛАН	
05	ДЕМОНТАЖНЫЙ ПЛАН	
06	МОНТАЖНЫЙ ПЛАН	
07	ПЛАН ПОСЛЕ ПЕРЕПЛАНИРОВКИ	
08	ПЛАН РАССТАНОВКИ МЕБЕЛИ И ОБОРУДОВАНИЯ	
09	ПЛАН РАССТАНОВКИ МЕБЕЛИ И ОБОРУДОВАНИЯ (РАЗМЕРЫ)	
10	СХЕМА УКАЗАНИЯ ПОДКЛЮЧЕНИЯ САНТЕХНИКИ	
11	ПЛАН РОЗЕТОК И ВЫКЛЮЧАТЕЛЕЙ (ПРИВЯЗКИ)	
12	ПЛАН РОЗЕТОК И ВЫКЛЮЧАТЕЛЕЙ (РАЗМЕРЫ)	
13	СПЕЦИФИКАЦИЯ ЭЛЕКТРООБОРУДОВАНИЯ	
14	ПЛАН РАССТАНОВКИ СВЕТИЛЬНИКОВ	
15	ПЛАН УПРАВЛЕНИЯ ОСВЕЩЕНИЕМ	
16	ПЛАН ТЕПЛОГО ПОЛА	
17	ПЛАН КОНДИЦИОНИРОВАНИЯ	
18	ПЛАН ОТДЕЛКИ ПОТОЛКОВ	
19	ПЛАН НАПОЛЬНЫХ ПОКРЫТИЙ	
20	ПЛАН ОТДЕЛКИ СТЕН	
21	ПЛАН ОТКРЫВАНИЯ ДВЕРЕЙ	
22	РАЗВЕРТКИ ПРИХОЖЕЙ	
23	ВИЗУАЛИЗАЦИИ ПРИХОЖЕЙ	
24	ВИЗУАЛИЗАЦИИ ПРИХОЖЕЙ	

Лист	Наименование	Примечание
25	РАЗВЕРТКИ САНУЗЛА	
26	ВИЗУАЛИЗАЦИИ САНУЗЛА	
27	ВИЗУАЛИЗАЦИИ САНУЗЛА	
28	РАЗВЕРТКИ СПАЛЬНИ	
29	ВИЗУАЛИЗАЦИИ СПАЛЬНИ	
30	ВИЗУАЛИЗАЦИИ СПАЛЬНИ	
31	РАЗВЕРТКИ КУХНИ-ГОСТИНОЙ	
32	ВИЗУАЛИЗАЦИИ КУХНИ-ГОСТИНОЙ	
33	ВИЗУАЛИЗАЦИИ КУХНИ-ГОСТИНОЙ	
34	ВИЗУАЛИЗАЦИИ КУХНИ-ГОСТИНОЙ	
35	ВИЗУАЛИЗАЦИИ КУХНИ-ГОСТИНОЙ	
36	ВИЗУАЛИЗАЦИИ КУХНИ-ГОСТИНОЙ	
37	РАЗВЕРТКИ БАЛКОНА	
38	ВИЗУАЛИЗАЦИ БАЛКОНА	

Существующее положение:

Объект строительства – квартира площадью 41,27 м² (на основании обмеров).

Монтажные работы осуществить согласно плана монтажа.

Сантехническое оборудование – разводку воды и канализации осуществить согласно инженерным проектам и техническим картам производителей на сантехоборудование.

Отделка выполняется согласно дизайн проекта с соблюдением технических условий при работе с каждым отделочным покрытием.

Замена относительно проекта строительных материалов, осветительных и сантехнических приборов влечет за собой изменения размеров, привязок и корректировки рабочей документации.

Фактические размеры могут отличаться от проектных.

За относительную отметку ±0,000 принят уровень чистого пола.

Привязки сантехнического оборудования даны от чистой поверхности стен с учетом отделки. Смотреть технические схемы оборудования, а также совместно с листами “Развертки стен санузла”.

Расположение и привязки бытовой техники на кухне согласовать с изготовителями кухонной мебели.

Предусмотреть доступ к инженерным коммуникациям посредством лючков или другим способом.


Дизайн проект			Подпись	Дата	Квартира Жк Аквилон beside	ПОЯСНИТЕЛЬНАЯ ЗАПИСКА	Стадия	Лист	Масштаб
	Разработал	Соколов Н.Е.					ДП	03	1:40
	Заказчик	Середин Д.П.							


ОБМЕРНЫЙ ПЛАН

Экспликация помещений

№	Наименование	Площадь, кв.м.
1	Прихожая	3,97
2	Санузел	3,77
3	Спальня	11,68
4	Кухня - гостиная	17,60
5	Балкон	4,25
		41,27 м²

Условные обозначения

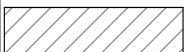Обозначение на плане	Наименование
	Несущая стена – бетон
	Пазогребневый блок
	Жилые помещения
	Мокрая зона кухни
	Мокрая зона санузлов

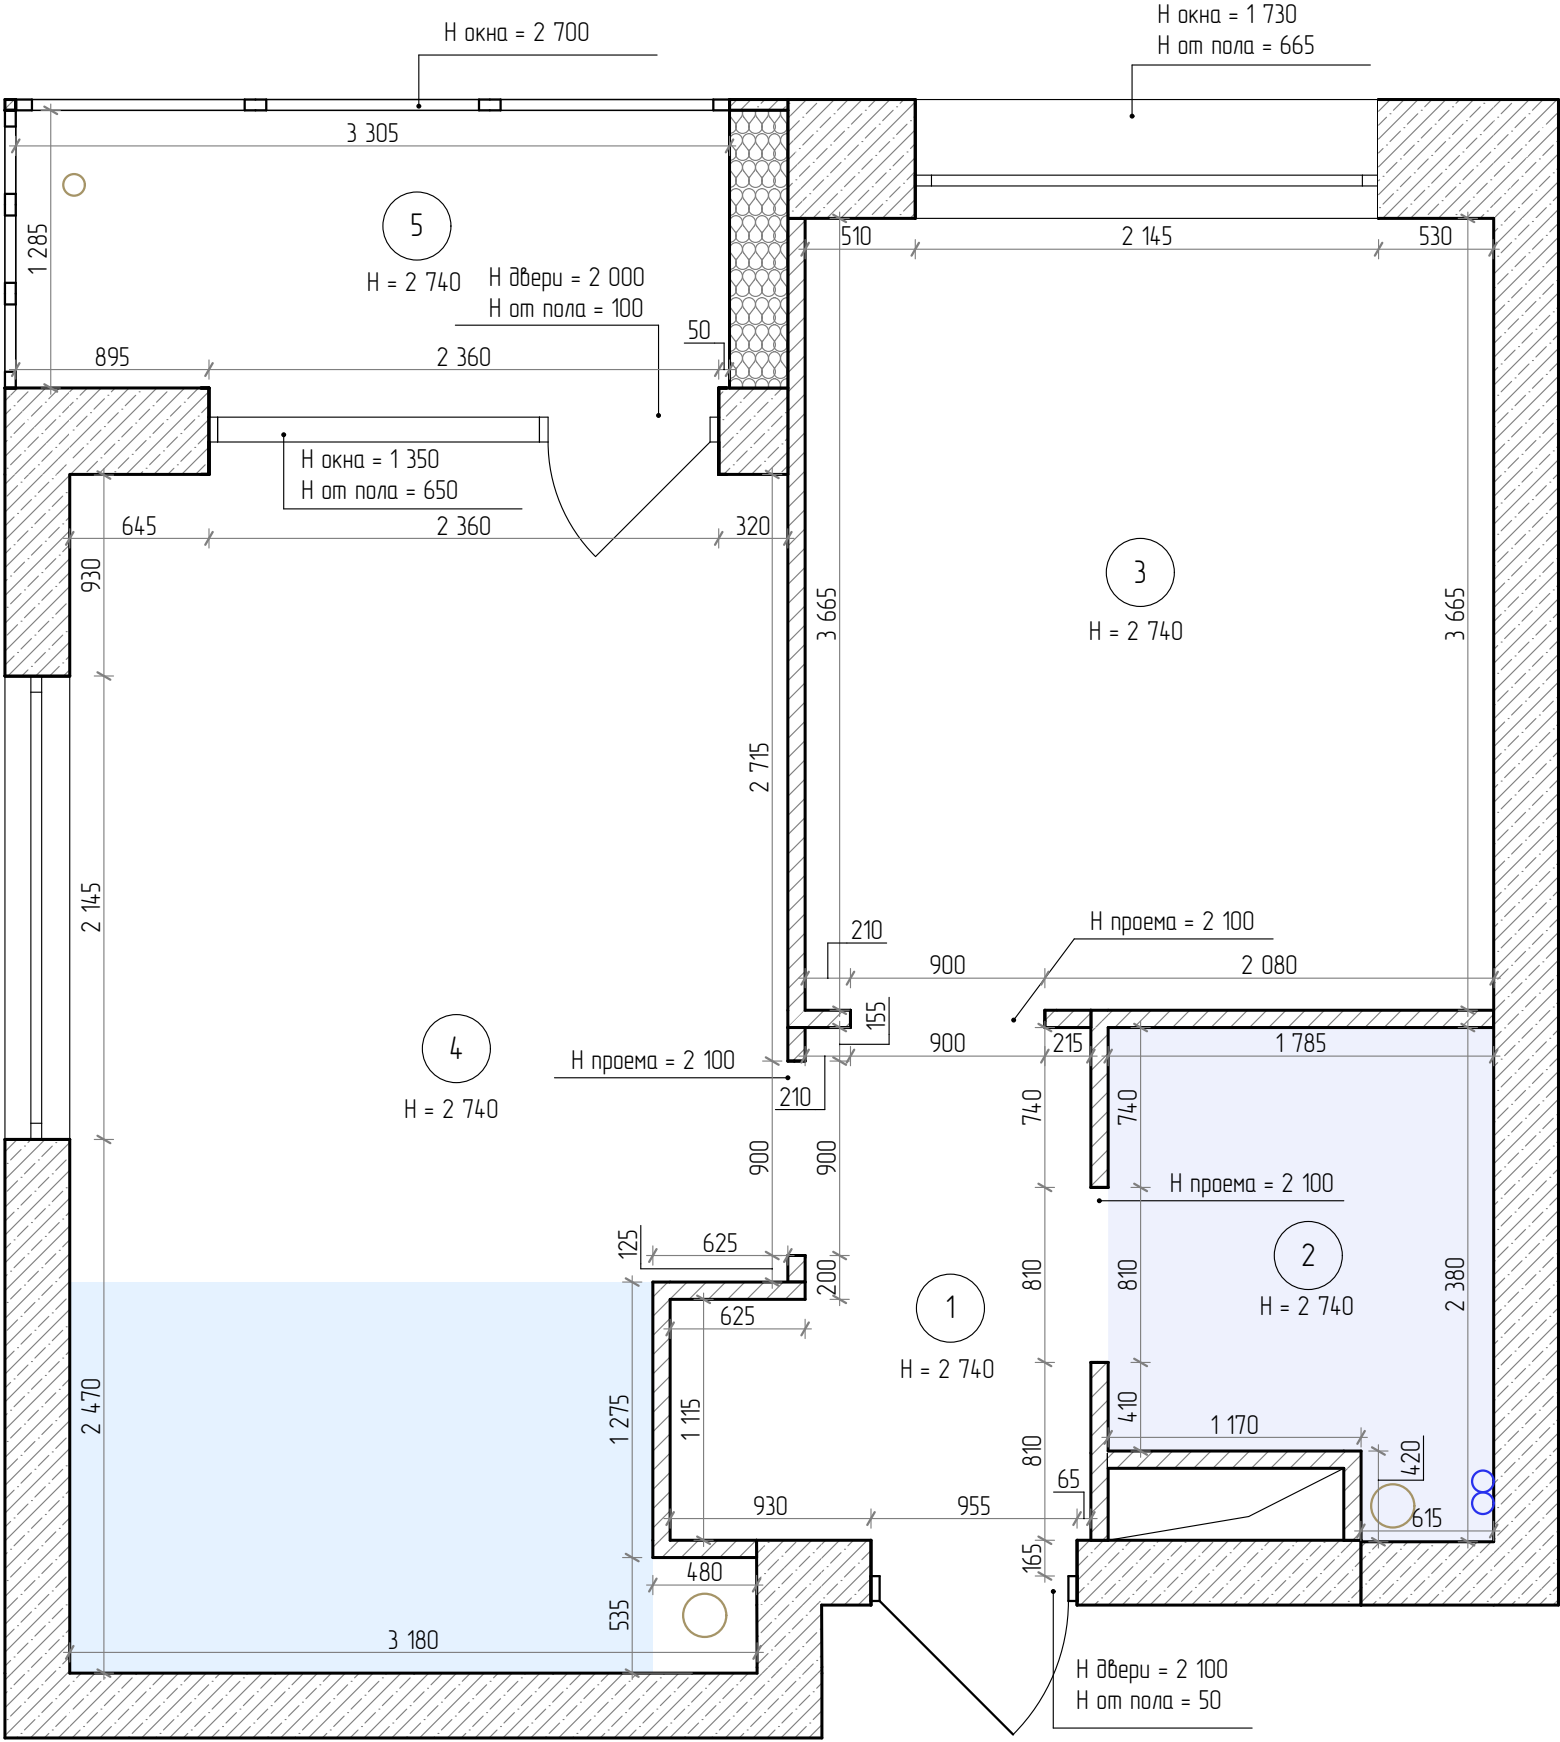

Дизайн проект

Разработал	Соколов Н.Е.	Подпись	Дата	Квартира
Заказчик	Середин Д.П.			Жк Аквилон beside

ОБМЕРНЫЙ ПЛАН


Стадия	Лист	Масштаб
ДП	04	1:40


ДЕМОНТАЖНЫЙ ПЛАН

Экспликация помещений

№	Наименование	Площадь, кв.м.
1	Прихожая	3,97
2	Санузел	3,77
3	Спальня	11,68
4	Кухня - гостиная	17,60
5	Балкон	4,25
		41,27 м²

Условные обозначения

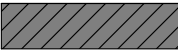Обозначение на плане	Наименование
	Несущая стена - бетон
	Пазогребневый блок
	Демонтируемые элементы

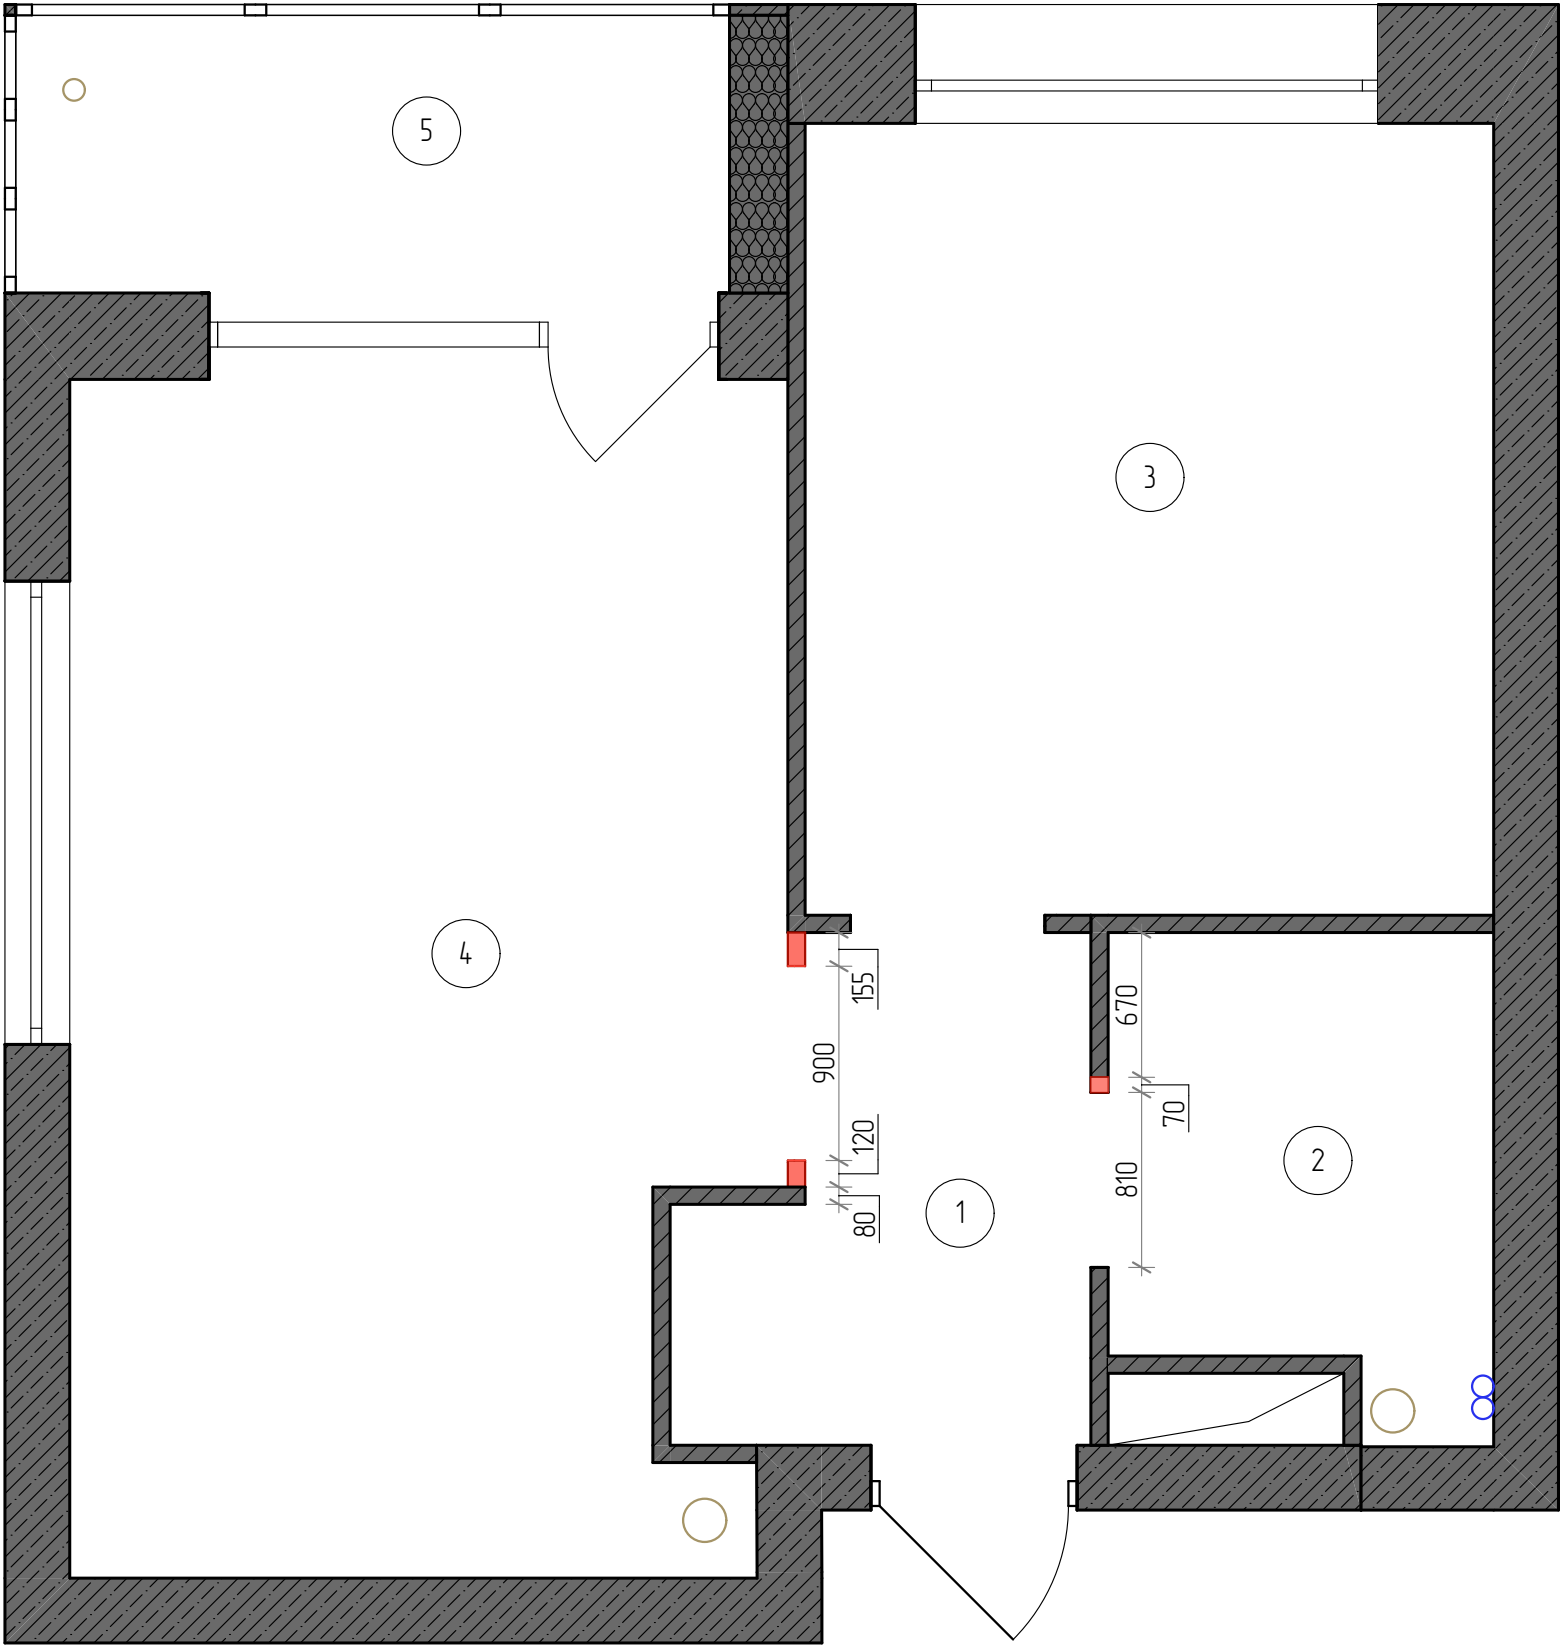

Дизайн проект

Разработал	Соколов Н.Е.	Подпись	Дата	Квартира
Заказчик	Середин Д.П.			Жк Аквилон beside

ДЕМОНТАЖНЫЙ ПЛАН

Стадия	Лист	Масштаб
ДП	05	1:40


МОНТАЖНЫЙ ПЛАН

Экспликация помещений

№	Наименование	Площадь, кв.м.
1	Прихожая	3,87
2	Санузел	3,14
3	Спальня	11,49
4	Кухня - гостиная	17,33
5	Балкон	4,25
		40,08 м²

Условные обозначения

Обозначение на плане	Наименование
	Несущая стена - бетон
	Пазогребневый блок
	Возводимые перегородки
	Штукатурка - 20мм
	Керамогранит - 15мм

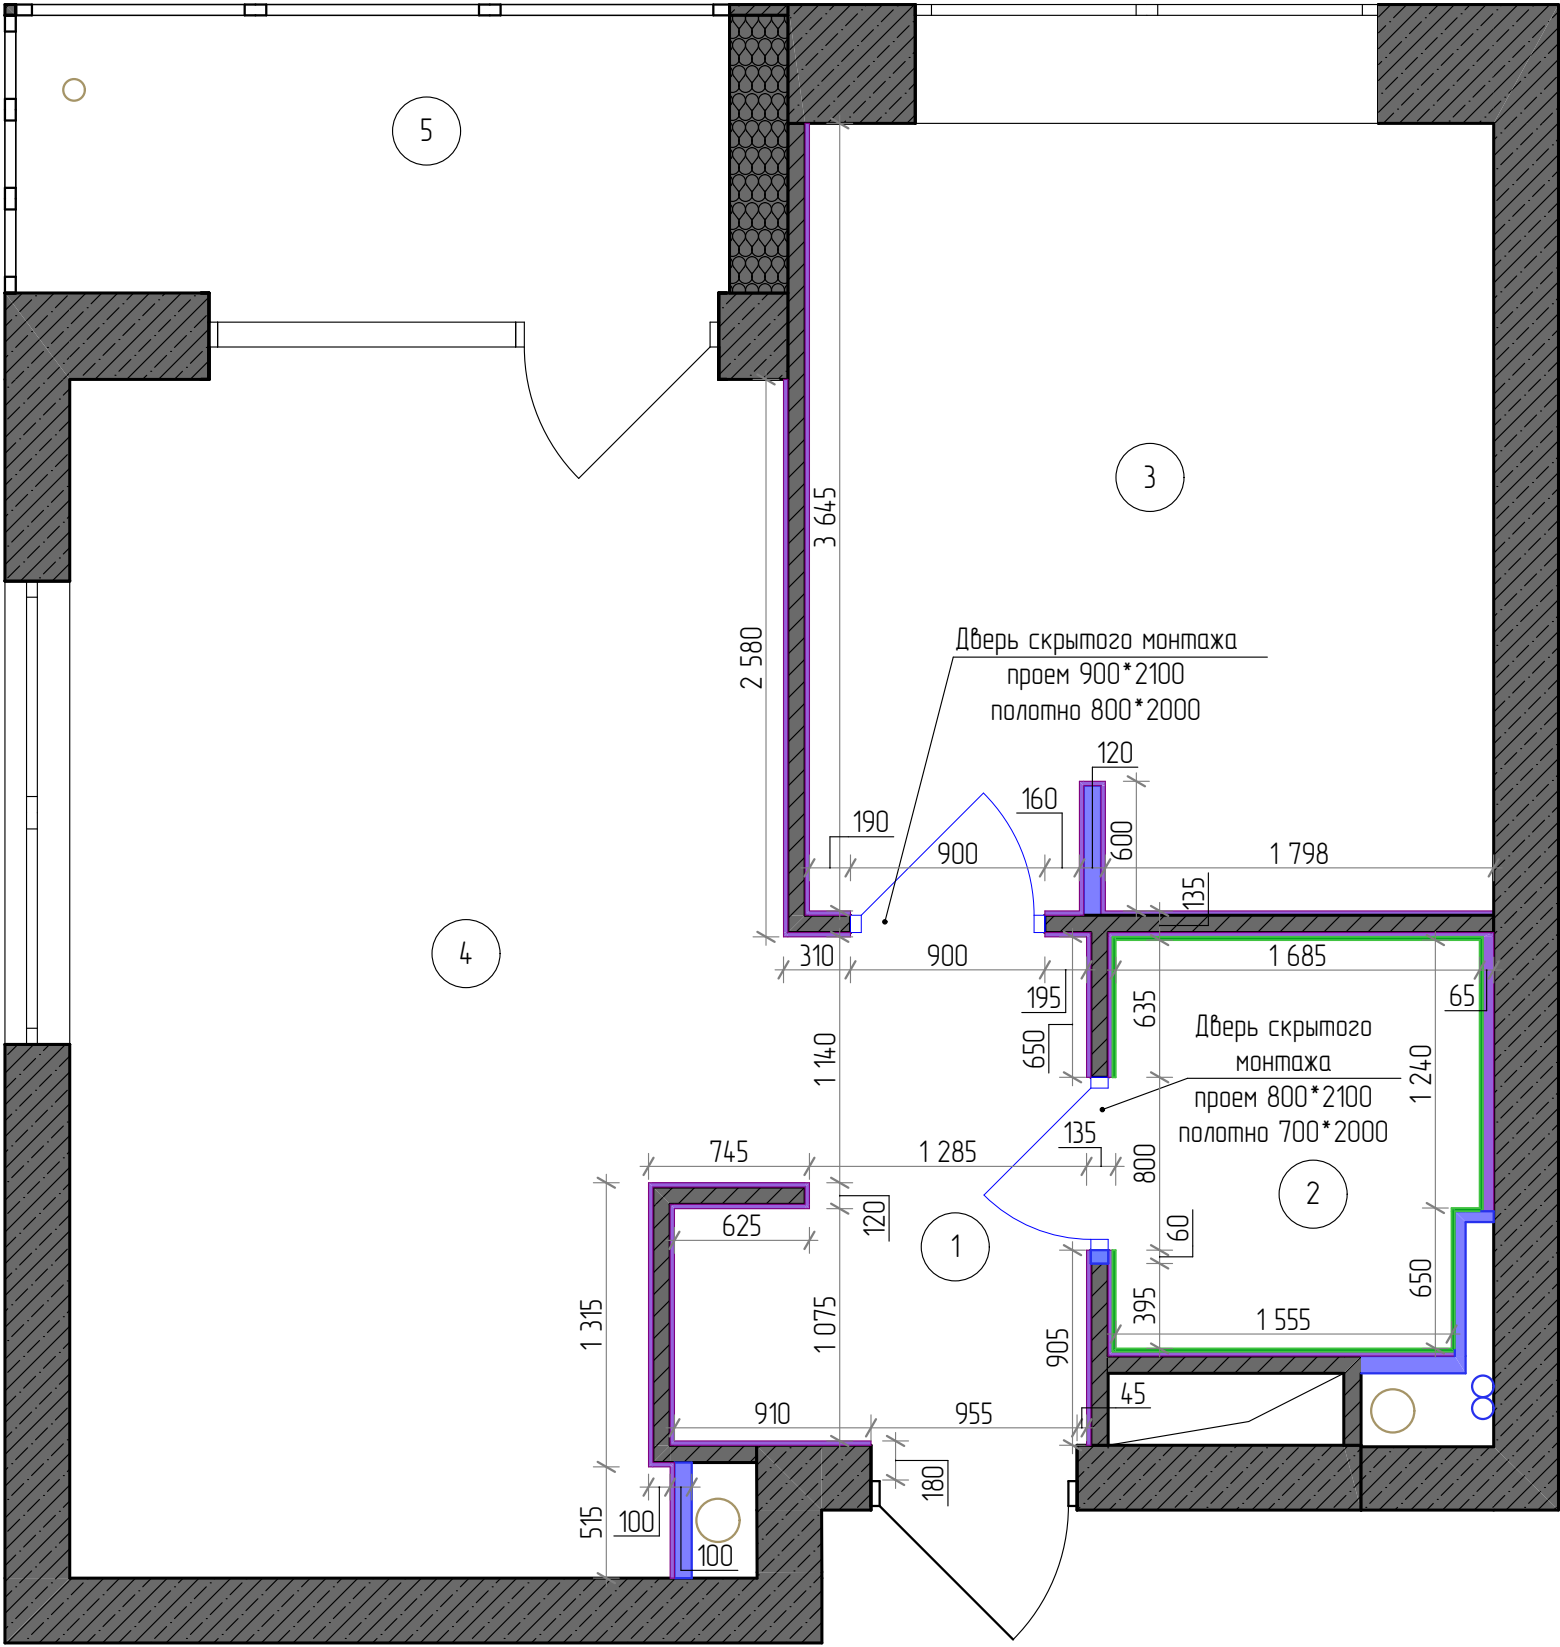

Дизайн проект


Разработал	Соколов Н.Е.	Подпись	Дата	Квартира
Заказчик	Середин Д.П.			Жк Аквилон beside

МОНТАЖНЫЙ ПЛАН

Стадия	Лист	Масштаб
ДП	06	1:40

Экспликация помещений

№	Наименование	Площадь, кв.м.
1	Прихожая	3,87
2	Санузел	3,14
3	Спальня	11,49
4	Кухня - гостиная	17,33
5	Балкон	4,25
		40,08 м²

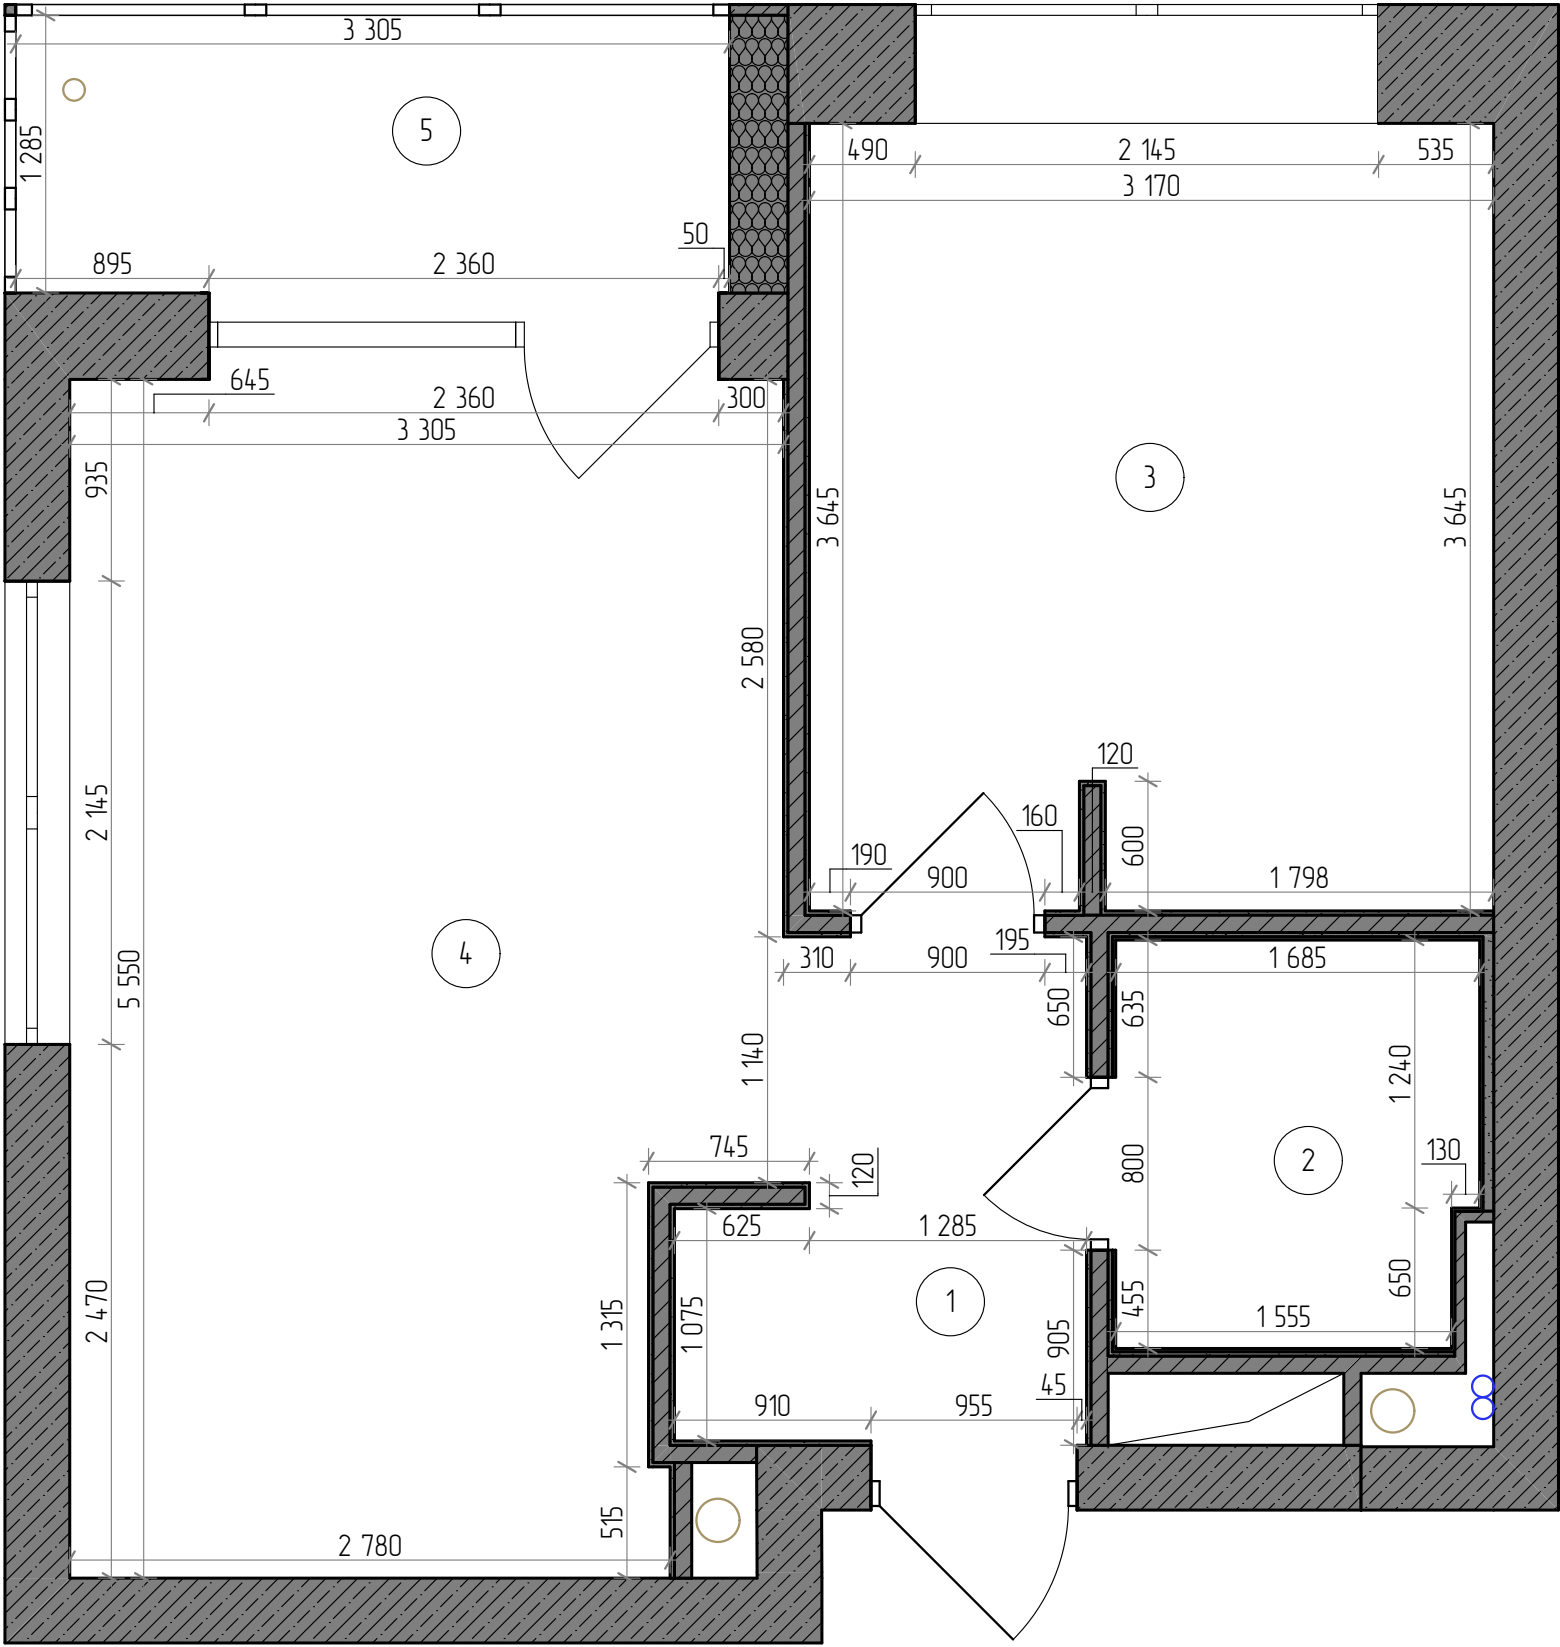


Дизайн проект

Разработал	Соколов Н.Е.	Подпись	Дата	Квартира
Заказчик	Середин Д.П.			Жк Аквилон beside

ПЛАН ПОСЛЕ ПЕРЕПЛАНИРОВКИ

Стадия	Лист	Масштаб
ДП	07	1:40

ПЛАН РАССТАНОВКИ МЕБЕЛИ И ОБОРУДОВАНИЯ

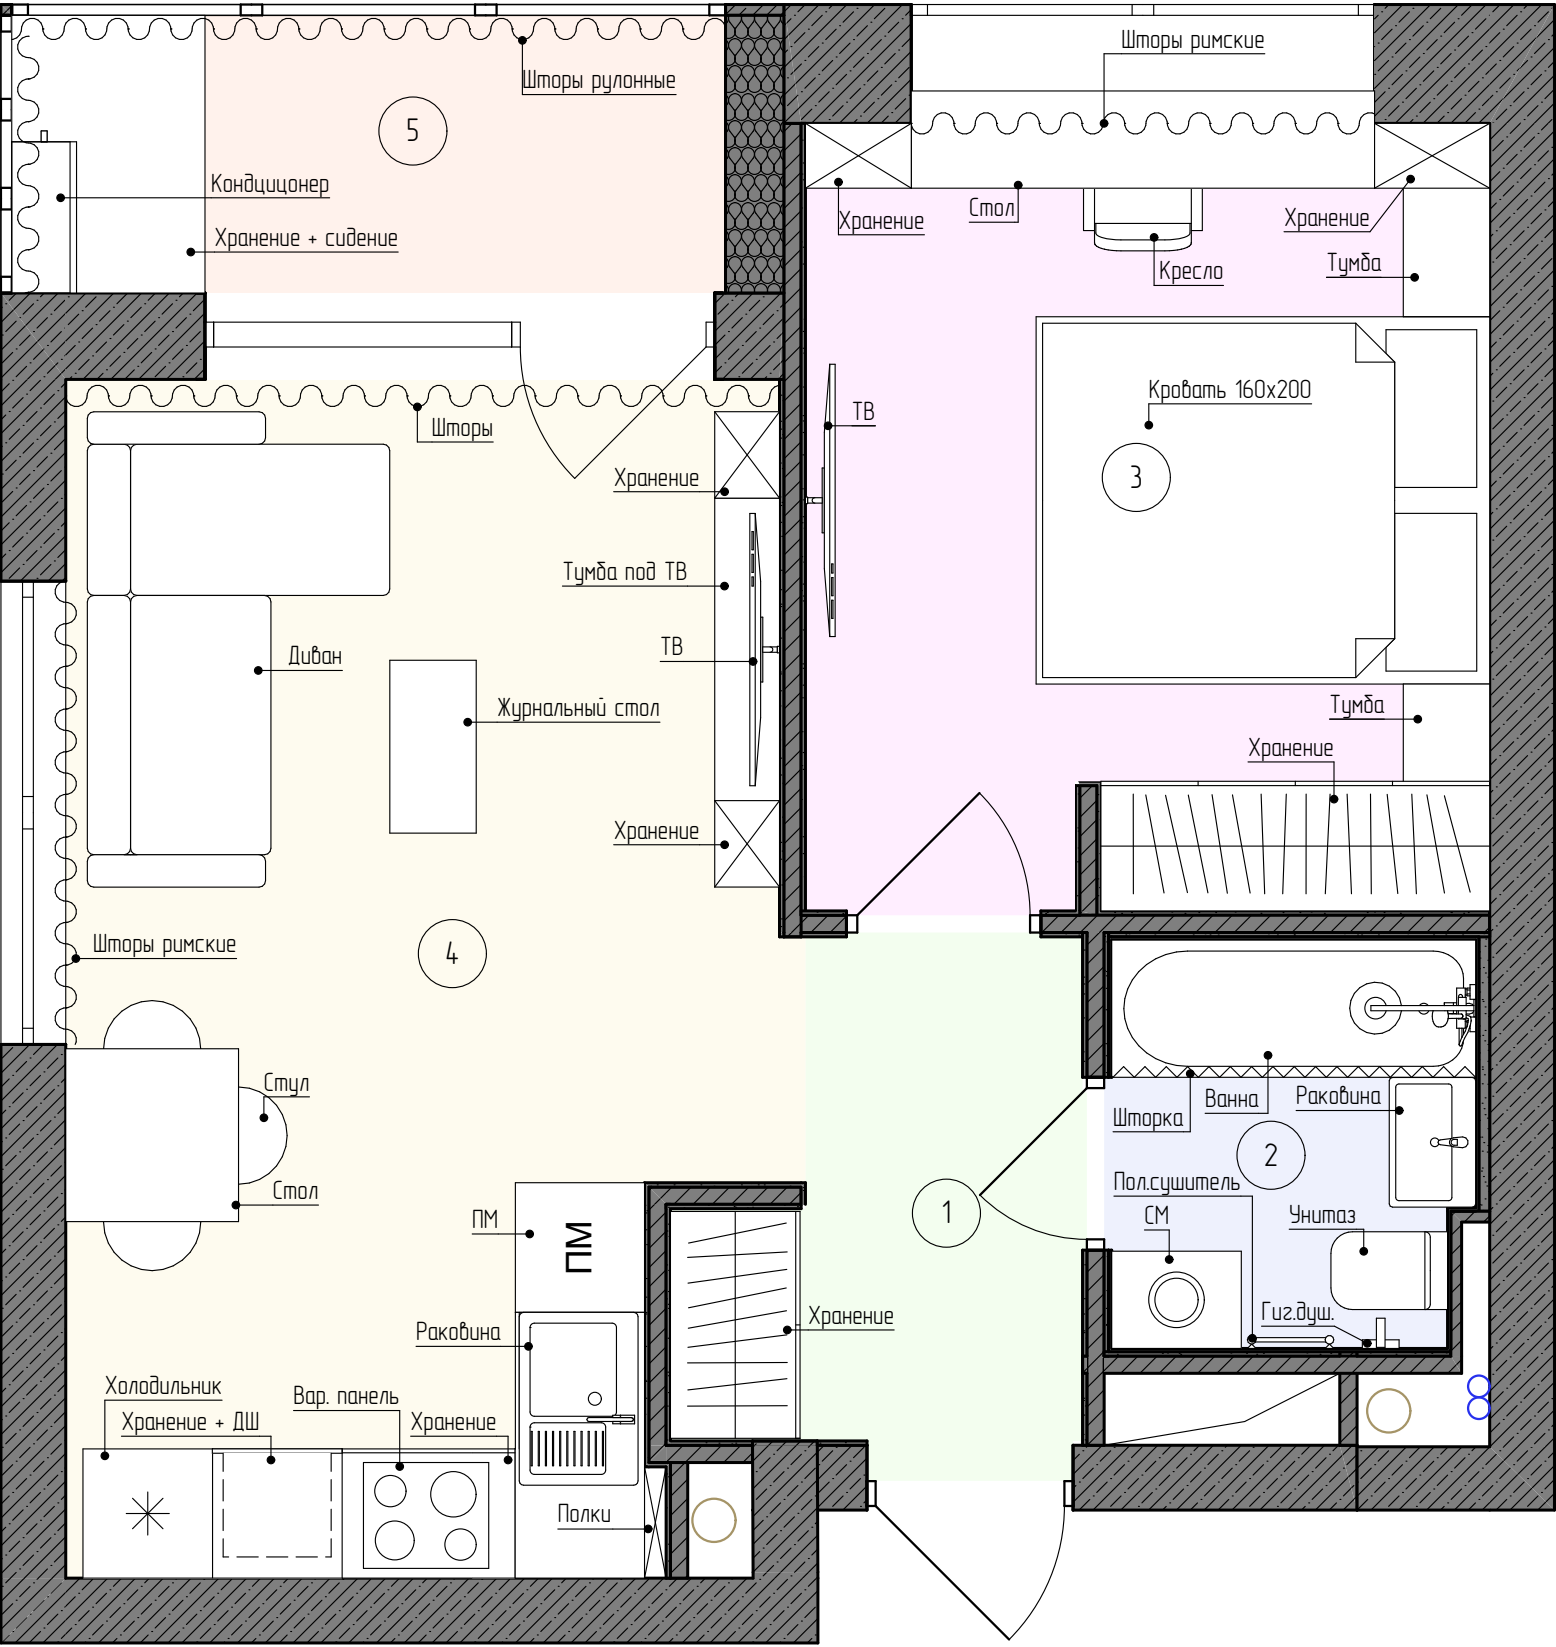

Экспликация помещений

№	Наименование	Площадь, кв.м.
1	Прихожая	3,97
2	Санузел	3,77
3	Спальня	11,68
4	Кухня - гостиная	17,60
5	Балкон	4,25
		41,27 м²

Дизайн проект


Разработал	Соколов Н.Е.	Подпись	Дата	Квартира
Заказчик	Середин Д.П.			Жк Аквилон beside

ПЛАН РАССТАНОВКИ МЕБЕЛИ И ОБОРУДОВАНИЯ

Стадия	Лист	Масштаб
ДП	08	1:40


Экспликация помещений


№	Наименование	Площадь, кв.м.
1	Прихожая	3,97
2	Санузел	3,77
3	Спальня	11,68
4	Кухня - гостиная	17,60
5	Балкон	4,25
		41,27 м²

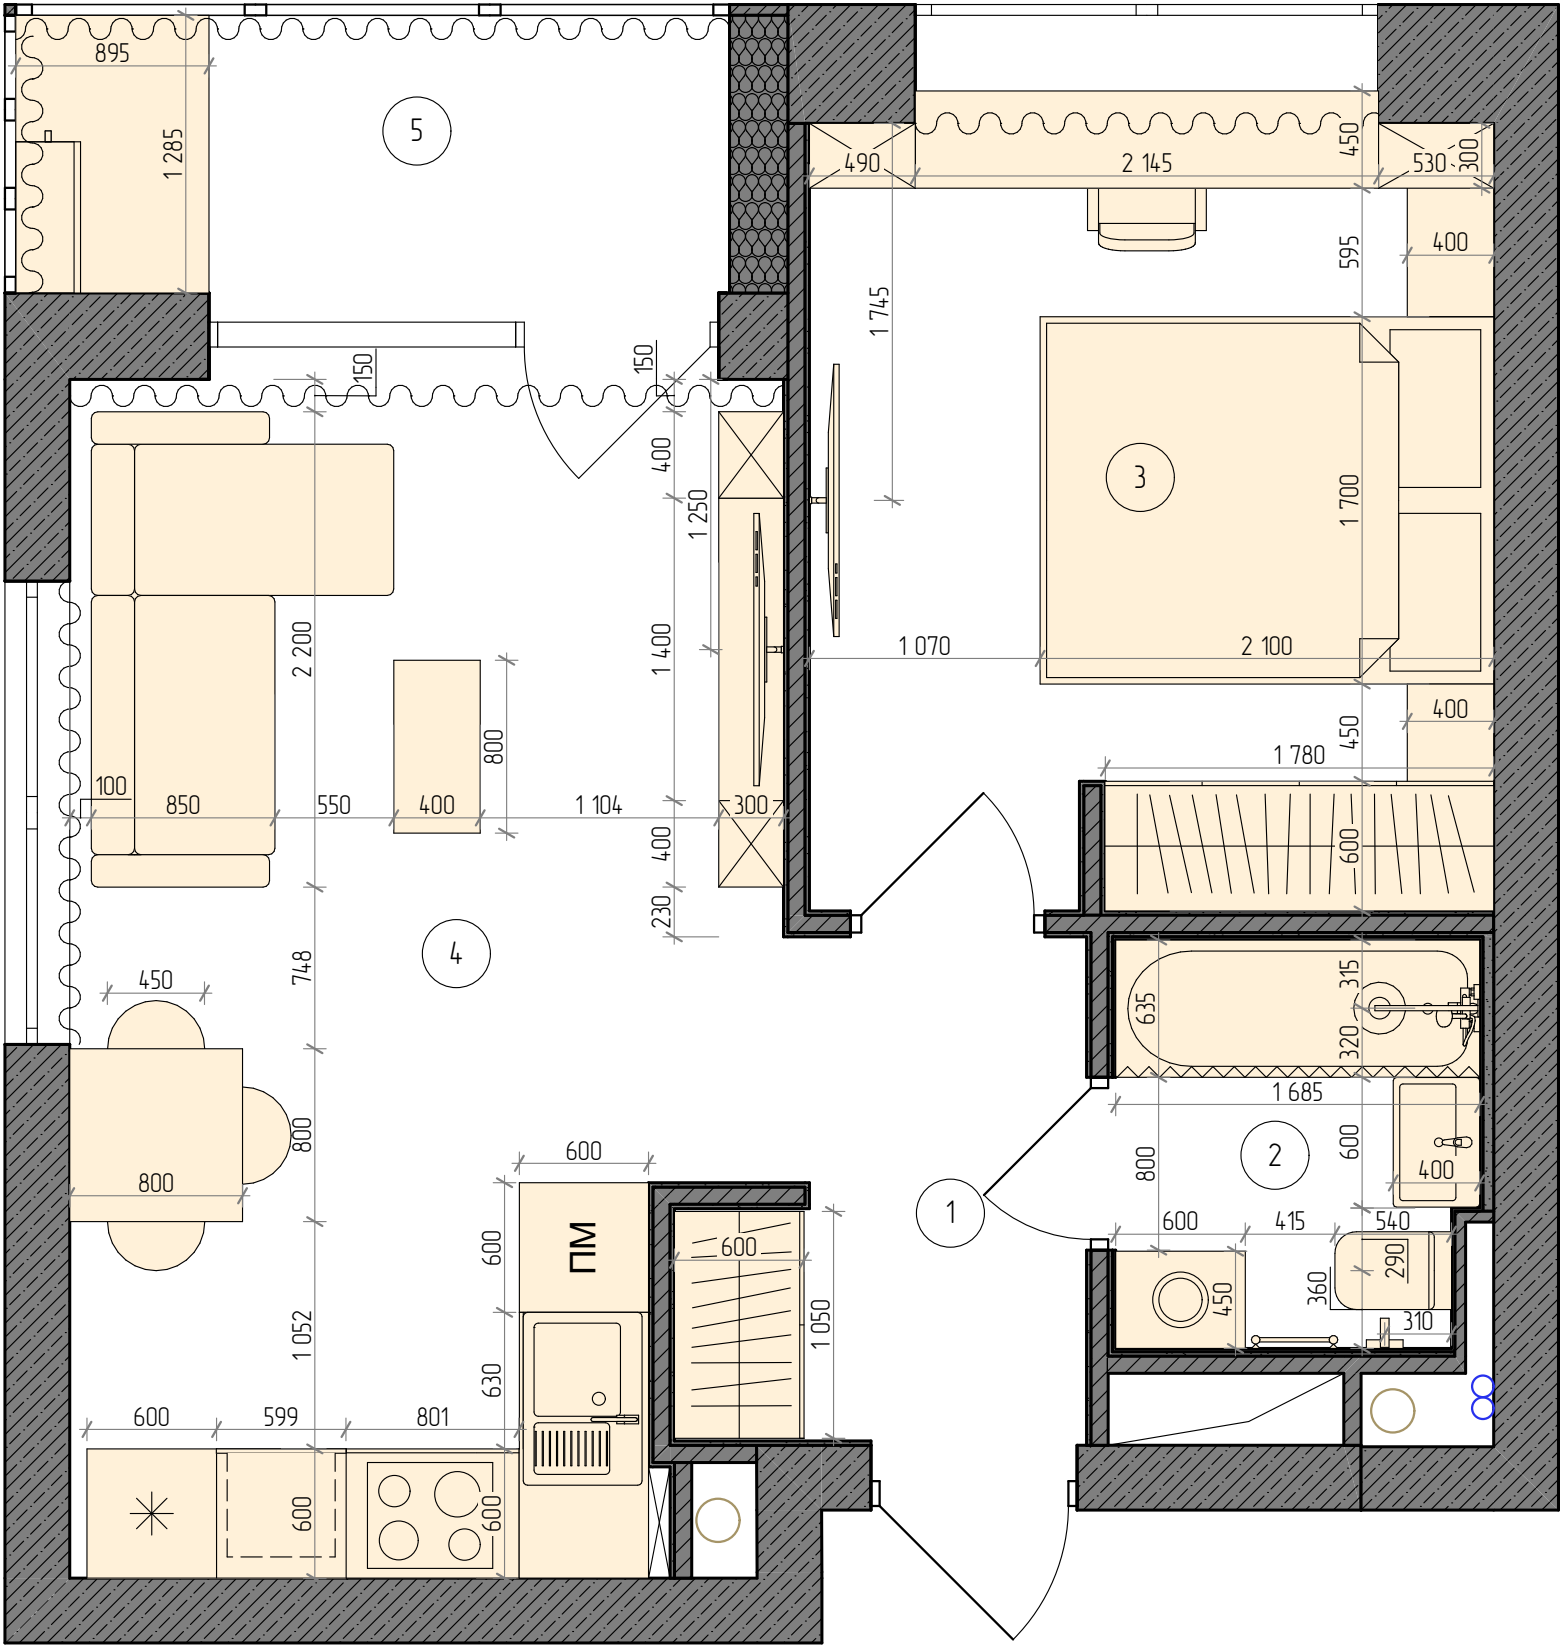

Экспликация помещений

№	Наименование	Площадь, кв.м.
1	Прихожая	3,97
2	Санузел	3,77
3	Спальня	11,68
4	Кухня - гостиная	17,60
5	Балкон	4,25
		41,27 м²

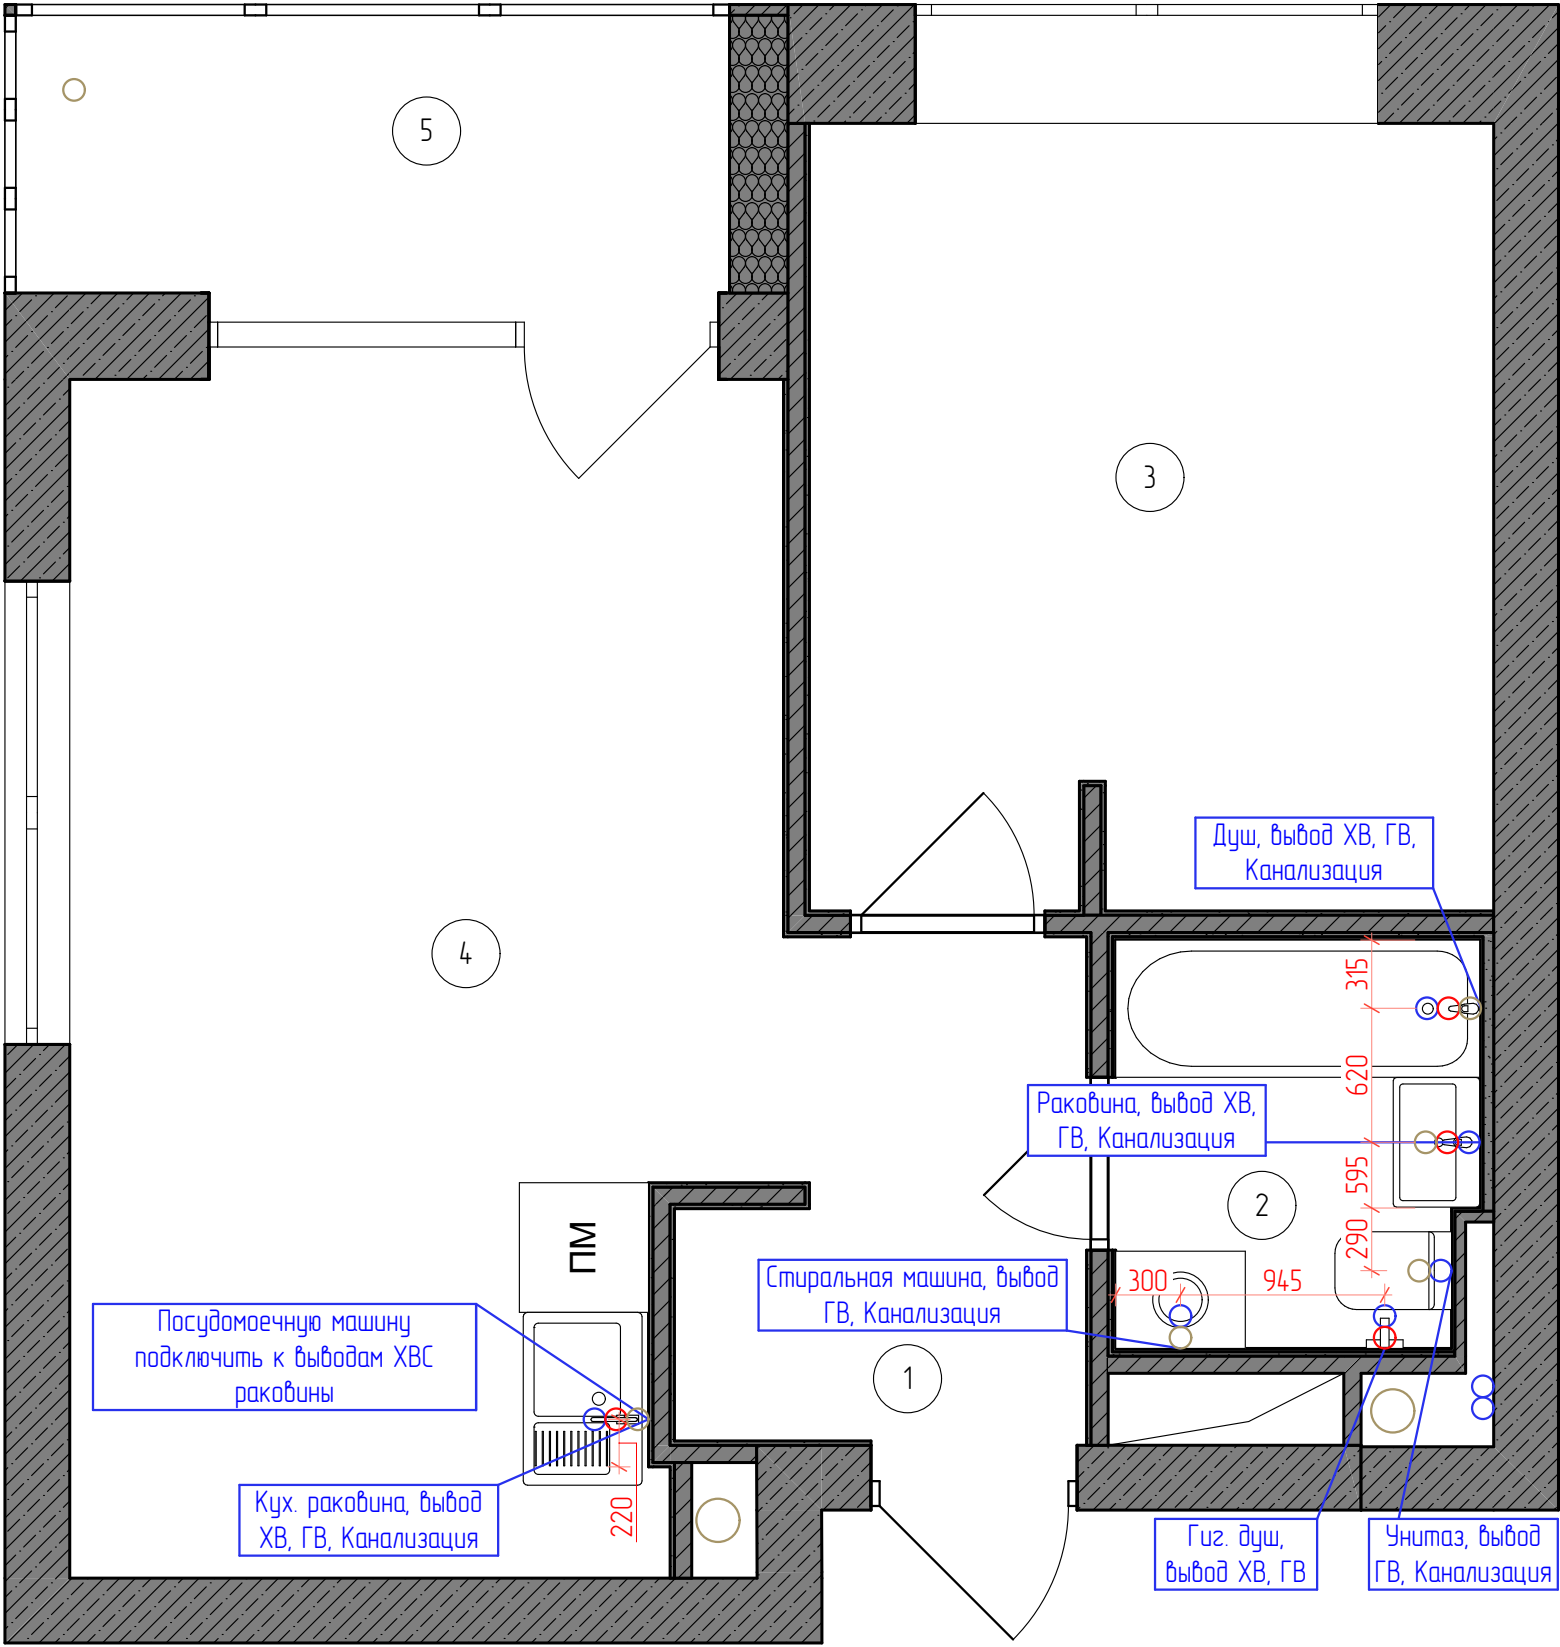

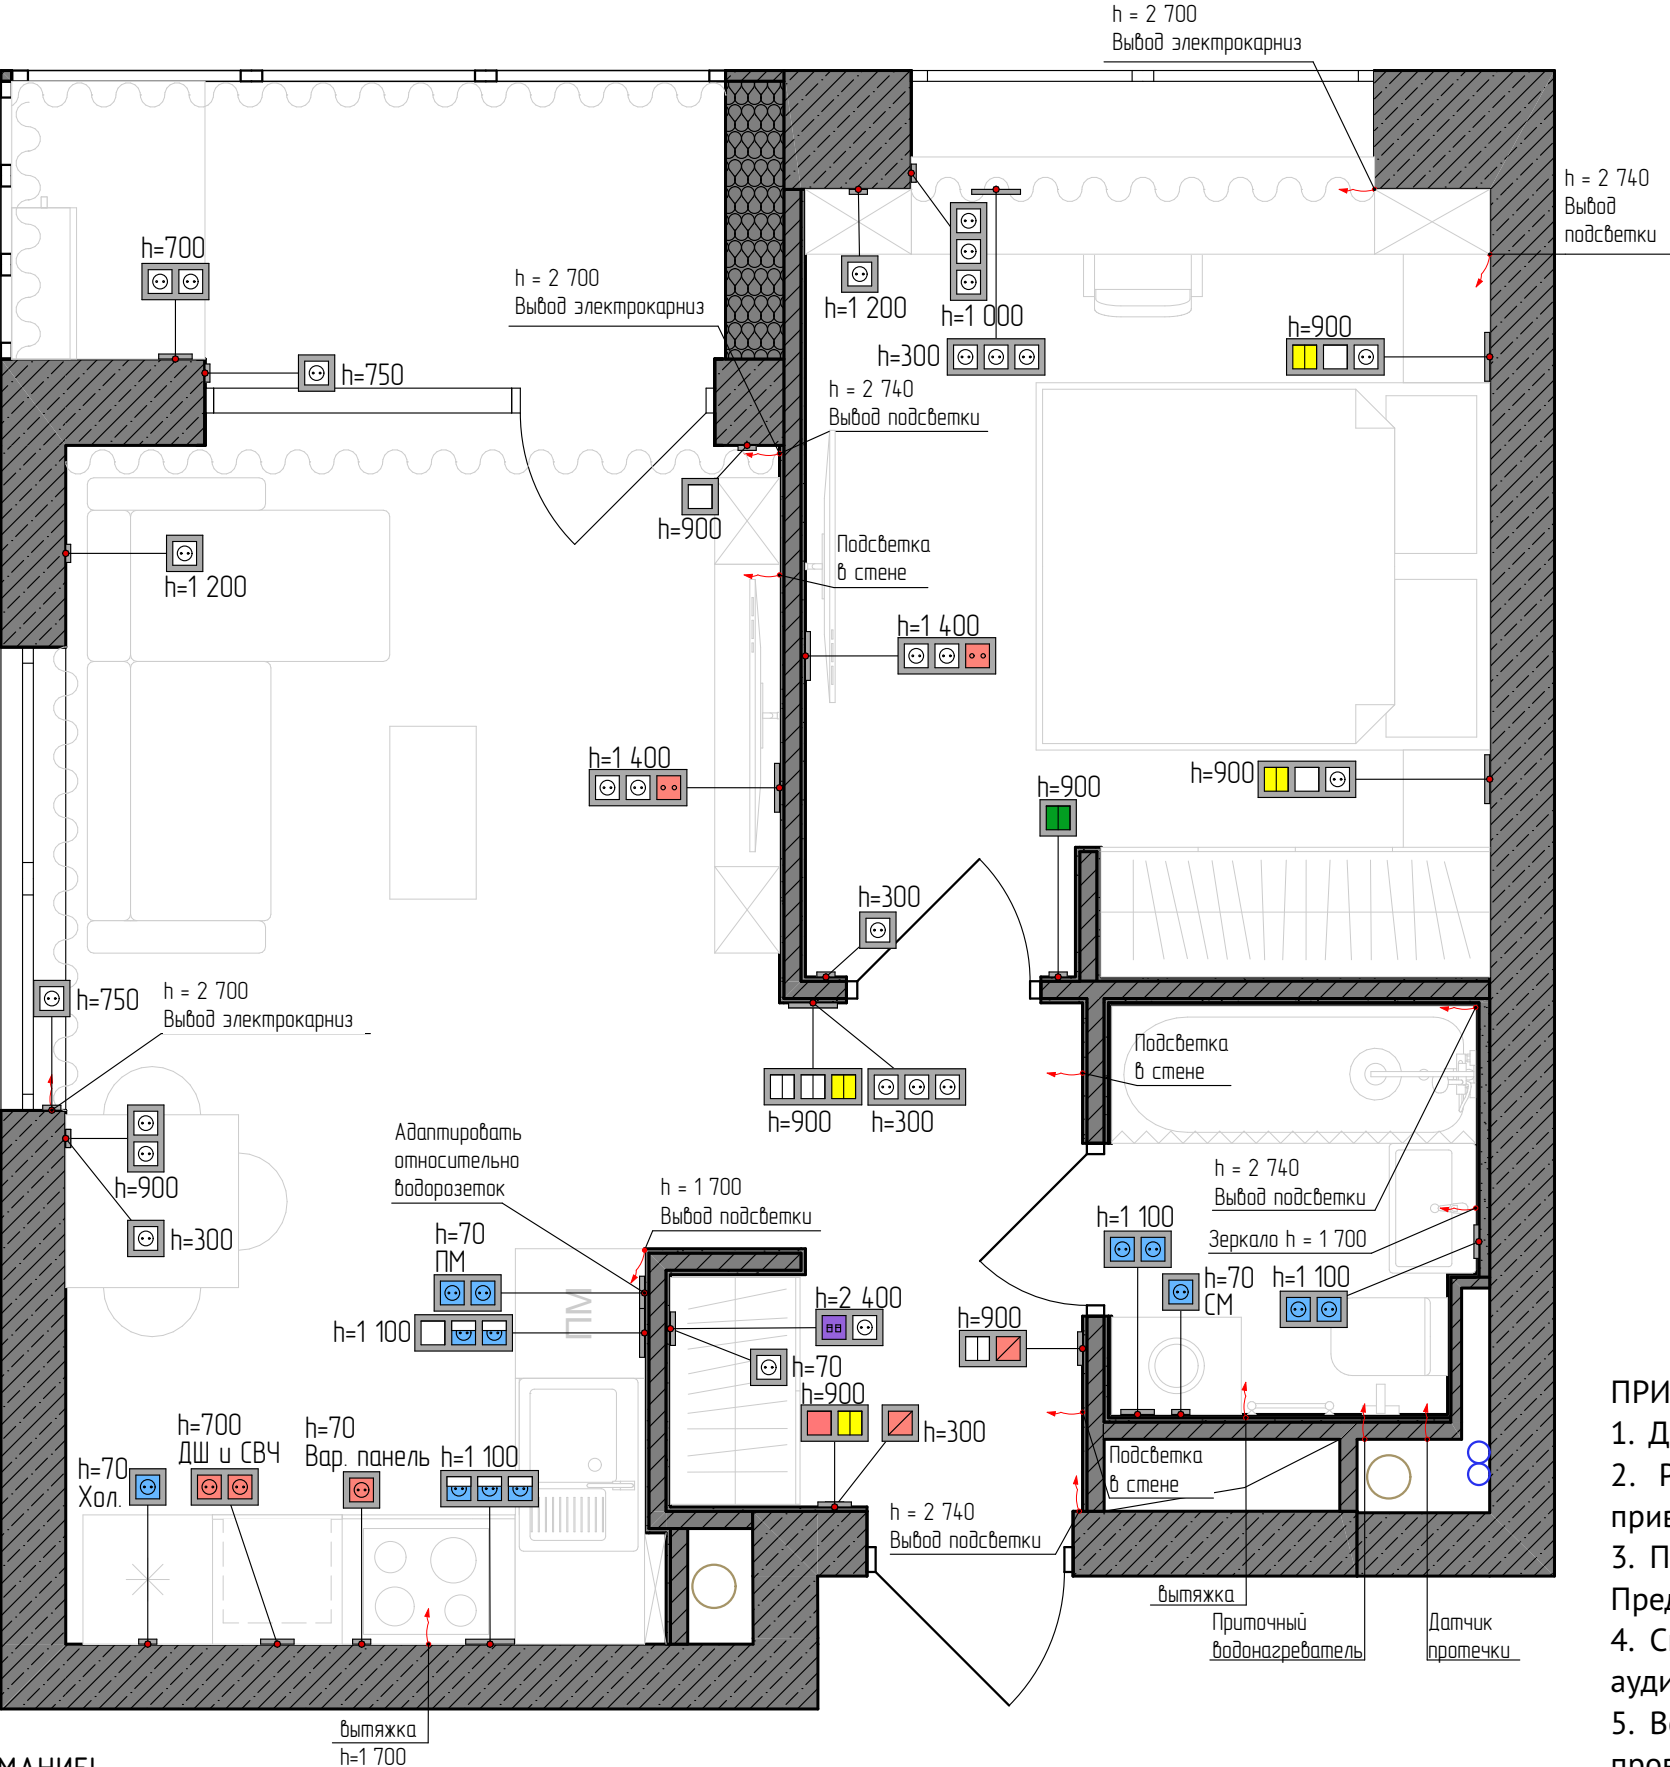

ПРИМЕЧАНИЯ:


1. Данный лист рассматривать совместно с разделом ЭО.
2. Розетки и электровыводы для кухонного оборудования, их количество и привязки согласовать по тех.картам поставщиков при заказе мебели.
3. Пожарная и охранная сигнализация выполняются по отдельным проектам. Предусмотреть питание и сигнальные кабели для датчиков.
4. Спутниковое ТВ, электропитание специальных устройств, бытовой техники, аудиосистем, электроники предусмотреть в соответствии с их особенностями.
5. Все размеры, указанные на чертежах, условны и требуют уточнения после проведения монтажных работ.

ВНИМАНИЕ!

1. При любом несоответствии привязок в натуре (вследствии погрешности в обмерах и строительных работах), по всем вопросам необходимо обратиться к авторам проекта для внесения соответствующих корректировок на месте.

Дизайн проект			Подпись	Дата	Квартира Жк Аквилон beside	ПЛАН РОЗЕТОК И ВЫКЛЮЧАТЕЛЕЙ (ПРИВЯЗКИ)	Стадия	Лист	Масштаб
	Разработал	Соколов Н.Е.					ДП	11	1:40
	Заказчик	Середин Д.П.							

ПЛАН РОЗЕТОК И ВЫКЛЮЧАТЕЛЕЙ (РАЗМЕРЫ)

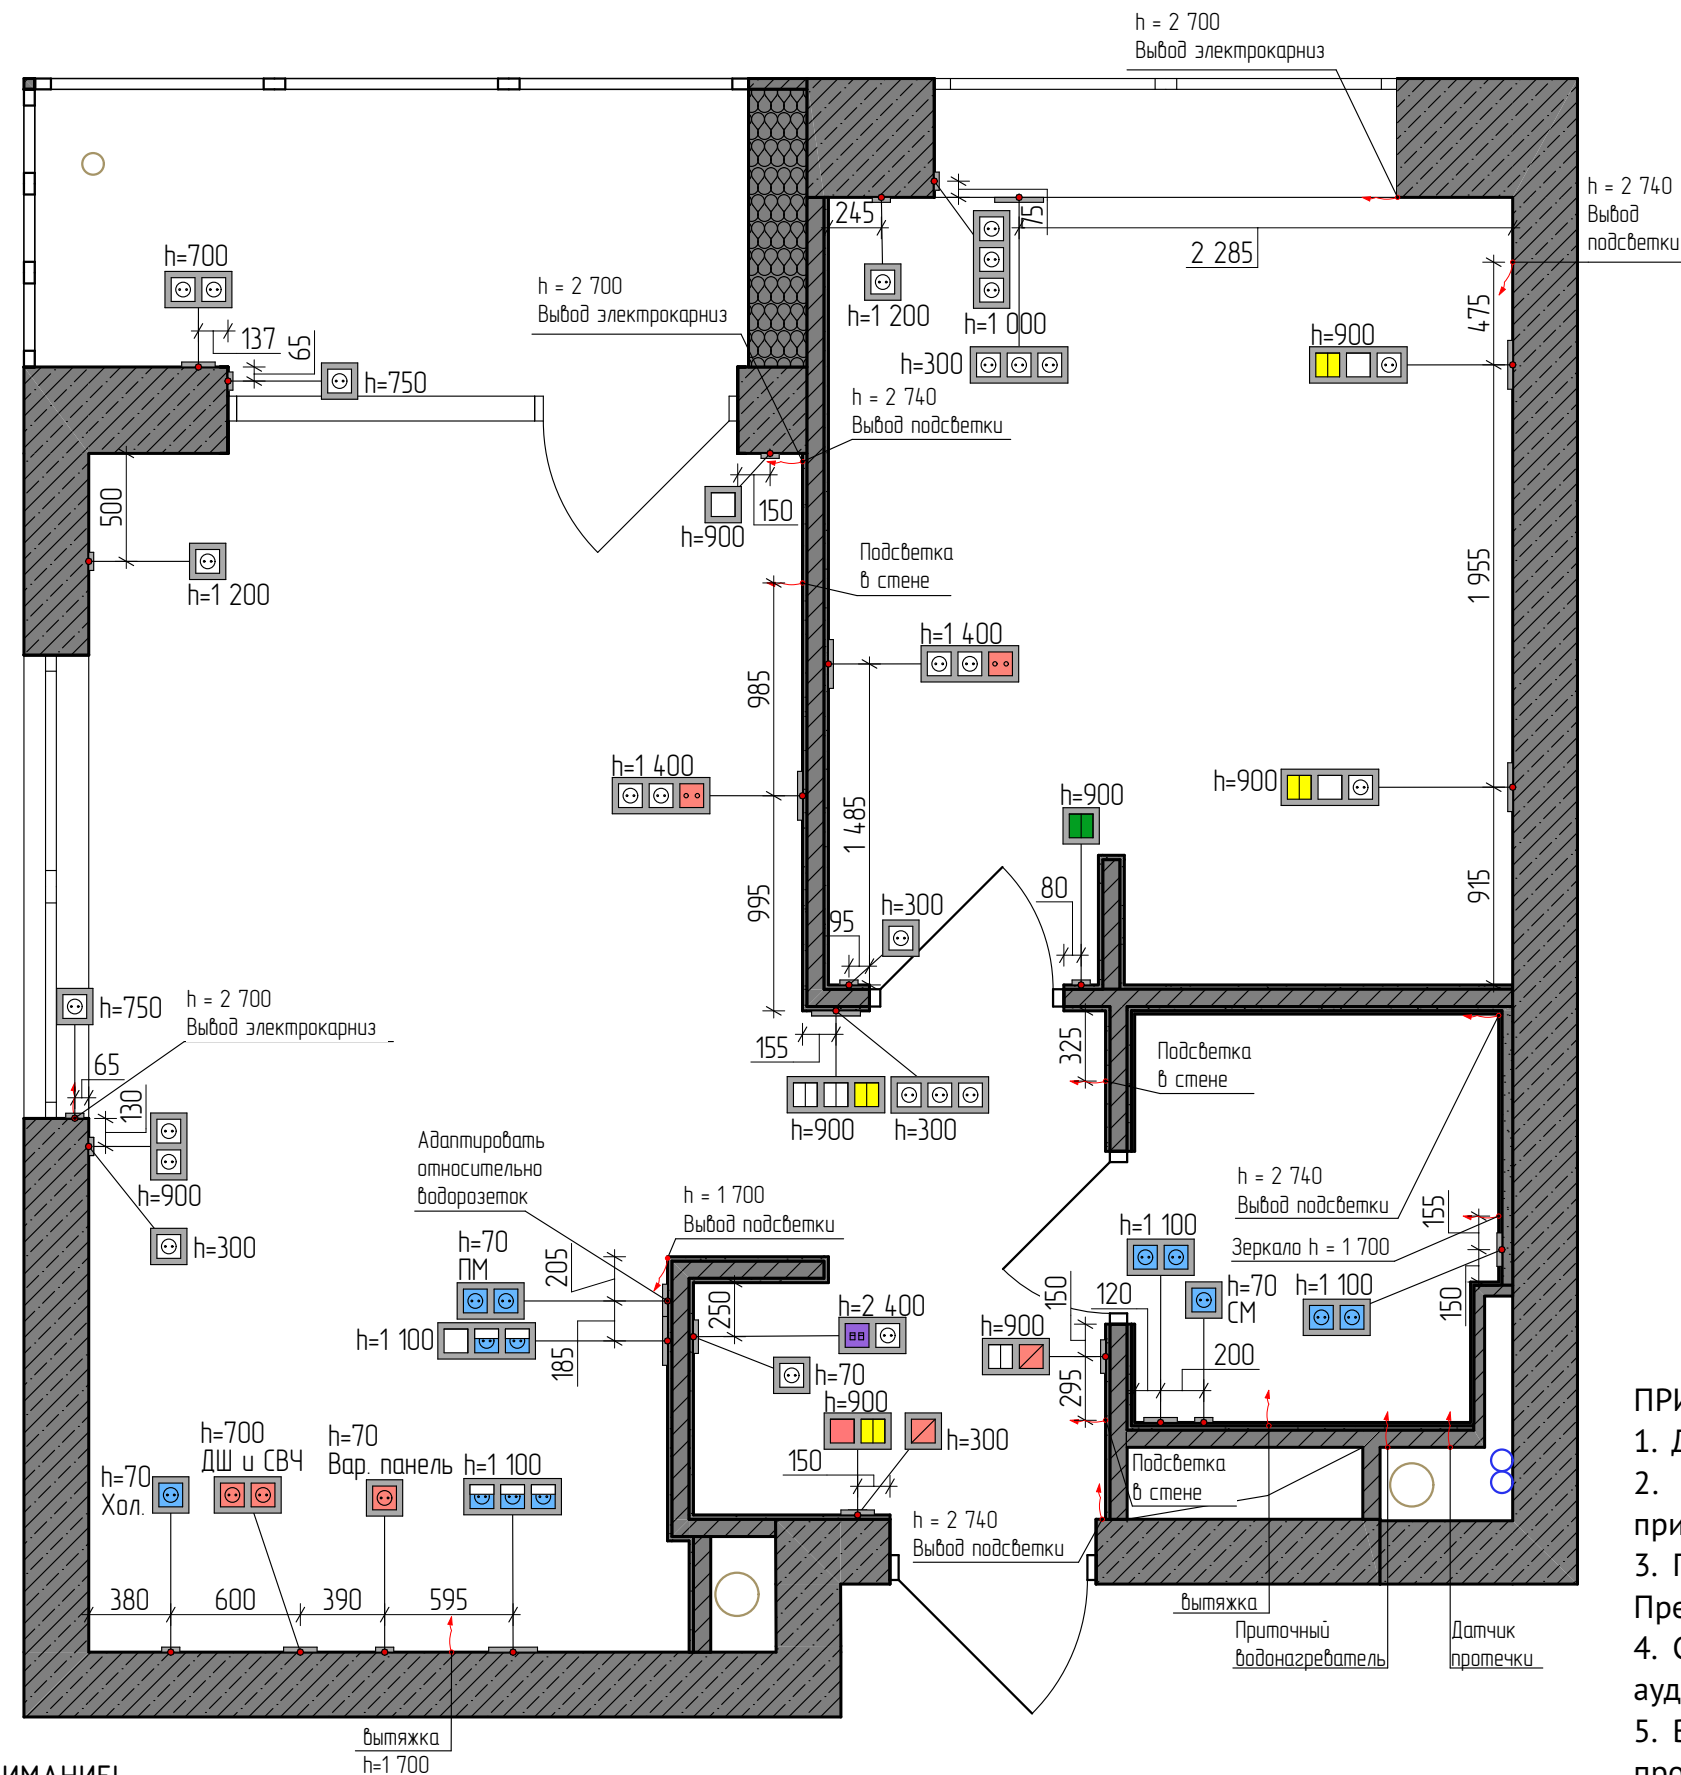

ПРИМЕЧАНИЯ:

1. Данный лист рассматривать совместно с разделом ЭО.
 2. Розетки и электровыводы для кухонного оборудования, их количество и привязки согласовать по тех.картам поставщиков при заказе мебели.
 3. Пожарная и охранный сигнализация выполняются по отдельным проектам.
- Предусмотреть питание и сигнальные кабели для датчиков.
4. Спутниковое ТВ, электропитание специальных устройств, бытовой техники, аудиосистем, электроники предусмотреть в соответствии с их особенностями.
 5. Все размеры, указанные на чертежах, условны и требуют уточнения после проведения монтажных работ.


ВНИМАНИЕ!

1. При любом несоответствии привязок в натуре (вследствии погрешности в обмерах и строительных работах), по всем вопросам необходимо обратиться к авторам проекта для внесения соответствующих корректировок на месте.

Дизайн проект			Подпись	Дата	Квартира	ПЛАН РОЗЕТОК И ВЫКЛЮЧАТЕЛЕЙ (РАЗМЕРЫ)	Стадия	Лист	Масштаб
	Разработал	Соколов Н.Е.			Жк Аквилон beside		ДП	12	1:40
	Заказчик	Середин Д.П.							

2D-символ	Класс защиты	Вставки(Механизмы)					Вставки(Механизмы) - Количество по типам										Кол.
		Поз. 1	Поз. 2	Поз. 3	Поз. 4	Поз. 5	Розетка 220	Выкл 1 кл.	Выкл 2 кл.	Выкл 3 кл.	Светорегулятор	Розетка TV	Розетка тел.	Розетка сетев.	Спец.	Заглушка	
	IP44	Розетка 220V	-	-	-	-	1	0	0	0	0	0	0	0	0	0	1
	IP20	Розетка 220V	Розетка 220V	Розетка телевизионная TV-FM	-	-	2	0	0	0	0	1	0	0	0	0	3
	IP20	Розетка 220V	Розетка 220V	Розетка 220V	-	-	3	0	0	0	0	0	0	0	0	0	3
	IP20	Розетка 220V	-	-	-	-	1	0	0	0	0	0	0	0	0	0	1
	IP20	Спец. - Терморегулятор теплого пола	-	-	-	-	0	0	0	0	0	0	0	0	1	0	1
	IP20	Розетка 220V	Розетка 220V	-	-	-	2	0	0	0	0	0	0	0	0	0	2
	IP44	Розетка 220V	Розетка 220V	-	-	-	2	0	0	0	0	0	0	0	0	0	2
	IP44	Розетка 220V Силавая	Розетка 220V Силавая	-	-	-	2	0	0	0	0	0	0	0	0	0	2
	IP44	Розетка 220V Силавая	-	-	-	-	1	0	0	0	0	0	0	0	0	0	1
	IP44	Розетка 220V с заземляющими контактами с крышкой	Розетка 220V с заземляющими контактами с крышкой	Розетка 220V с заземляющими контактами с крышкой	-	-	3	0	0	0	0	0	0	0	0	0	3
	IP44	Выключатель 1 клавишный	Розетка 220V с заземляющими контактами с крышкой	Розетка 220V с заземляющими контактами с крышкой	-	-	2	1	0	0	0	0	0	0	0	0	3
	IP20	Выключатель 2 клавишный	Терморегулятор теплого пола	-	-	-	0	0	1	0	0	0	0	0	1	0	2
	IP20	Выключатель 1 клавишный Мастер	Выключатель 2 клавишный проходной	-	-	-	0	1	1	0	0	0	0	0	0	0	2
	IP20	Выключатель 2 клавишный (перекрестный)	-	-	-	-	0	0	1	0	0	0	0	0	0	0	1

2D-символ	Класс защиты	Вставки(Механизмы)					Вставки(Механизмы) - Количество по типам										Кол.
		Поз. 1	Поз. 2	Поз. 3	Поз. 4	Поз. 5	Розетка 220	Выкл 1 кл.	Выкл 2 кл.	Выкл 3 кл.	Светорегулятор	Розетка TV	Розетка тел.	Розетка сетев.	Спец.	Заглушка	
	IP20	Выключатель 1 клавишный	-	-	-	-	0	1	0	0	0	0	0	0	0	0	1
	IP20	Розетка сетевая Роутер	Розетка 220V	-	-	-	1	0	0	0	0	0	0	1	0	0	2
	IP20	Выключатель 2 клавишный	Выключатель 2 клавишный	Выключатель 2 клавишный проходной	-	-	0	0	3	0	0	0	0	0	0	0	3
	IP20	Выключатель 2 клавишный проходной	Выключатель 1 клавишный	Розетка 220V	-	-	1	1	1	0	0	0	0	0	0	0	3
	IP20	Розетка 220V	Розетка 220V	Розетка 220V	-	-	3	0	0	0	0	0	0	0	0	0	3
							43	5	8	0	0	2	0	1	2	0	61

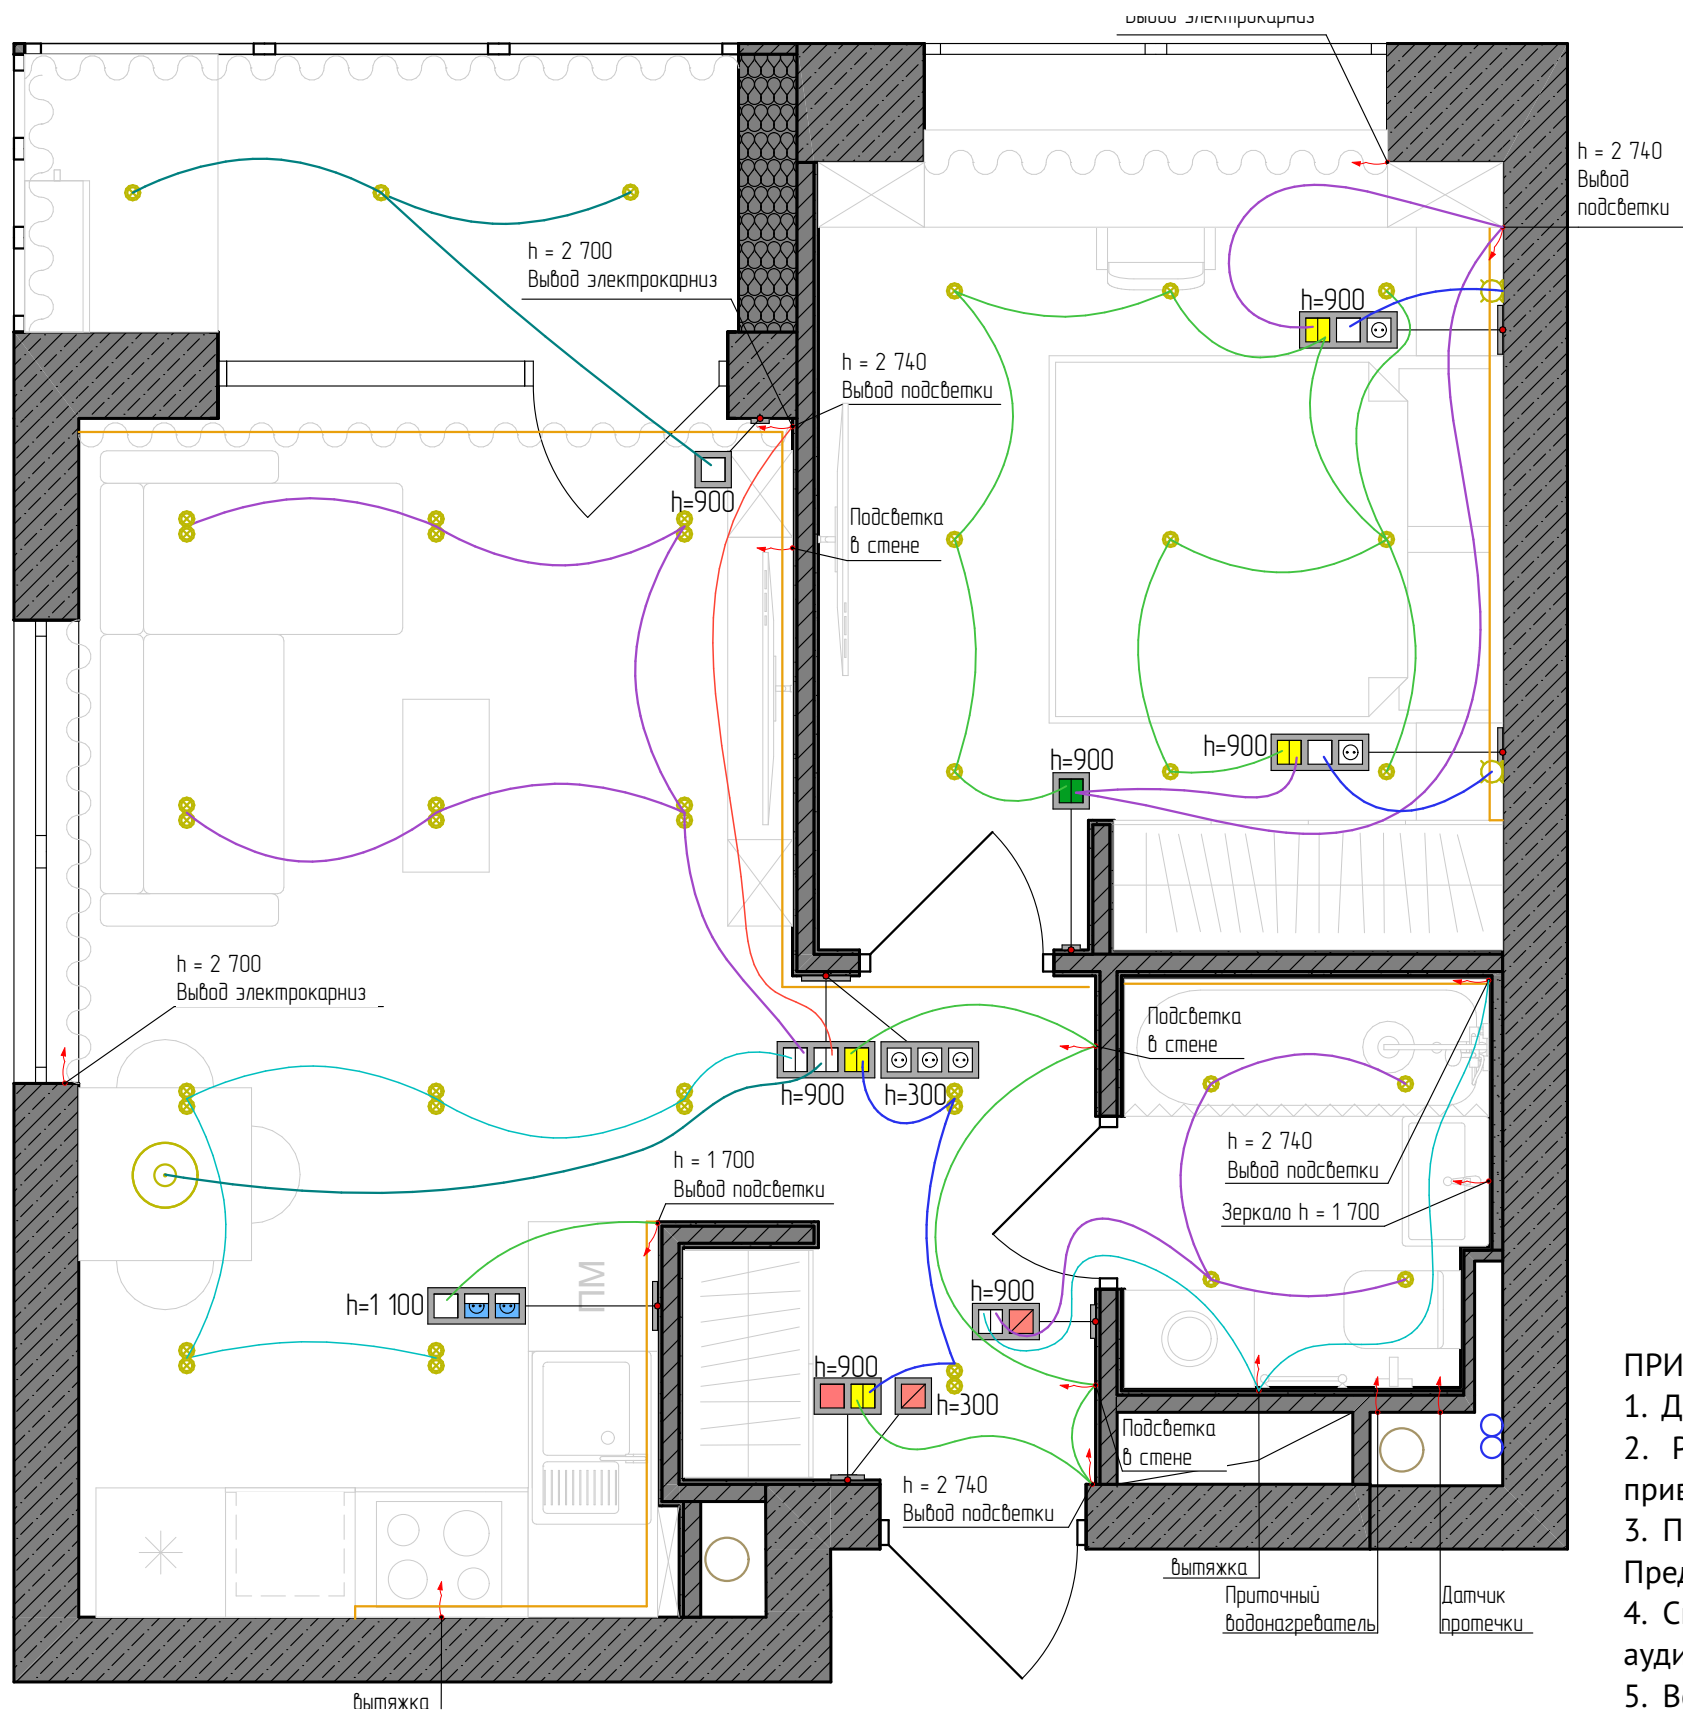

Спецификация освещения

Обозначение на плане	Наименование	Количество
⊗	Точечный светильник	16
⊗⊗	Двойной точечный светильник	13
⊙	Бра	2
—	Встроенная подсветка	15 м

ПРИМЕЧАНИЯ:


- Данный лист рассматривать совместно с разделом ЭО.
- Розетки и электровыводы для кухонного оборудования, их количество и привязки согласовать по тех.картам поставщиков при заказе мебели.
- Пожарная и охранная сигнализация выполняются по отдельным проектам. Предусмотреть питание и сигнальные кабели для датчиков.
- Спутниковое ТВ, электропитание специальных устройств, бытовой техники, аудиосистем, электроники предусмотреть в соответствии с их особенностями.
- Все размеры, указанные на чертежах, условны и требуют уточнения после проведения монтажных работ.

ВНИМАНИЕ!

1. При любом несоответствии привязок в натуре (вследствии погрешности в обмерах и строительных работах), по всем вопросам необходимо обратиться к авторам проекта для внесения соответствующих корректировок на месте.


Экспликация помещений

№	Наименование	Площадь, кв.м.
1	Прихожая	3,97
2	Санузел	3,77
3	Спальня	11,68
4	Кухня – гостиная	17,60
5	Балкон	4,25
		41,27 м²

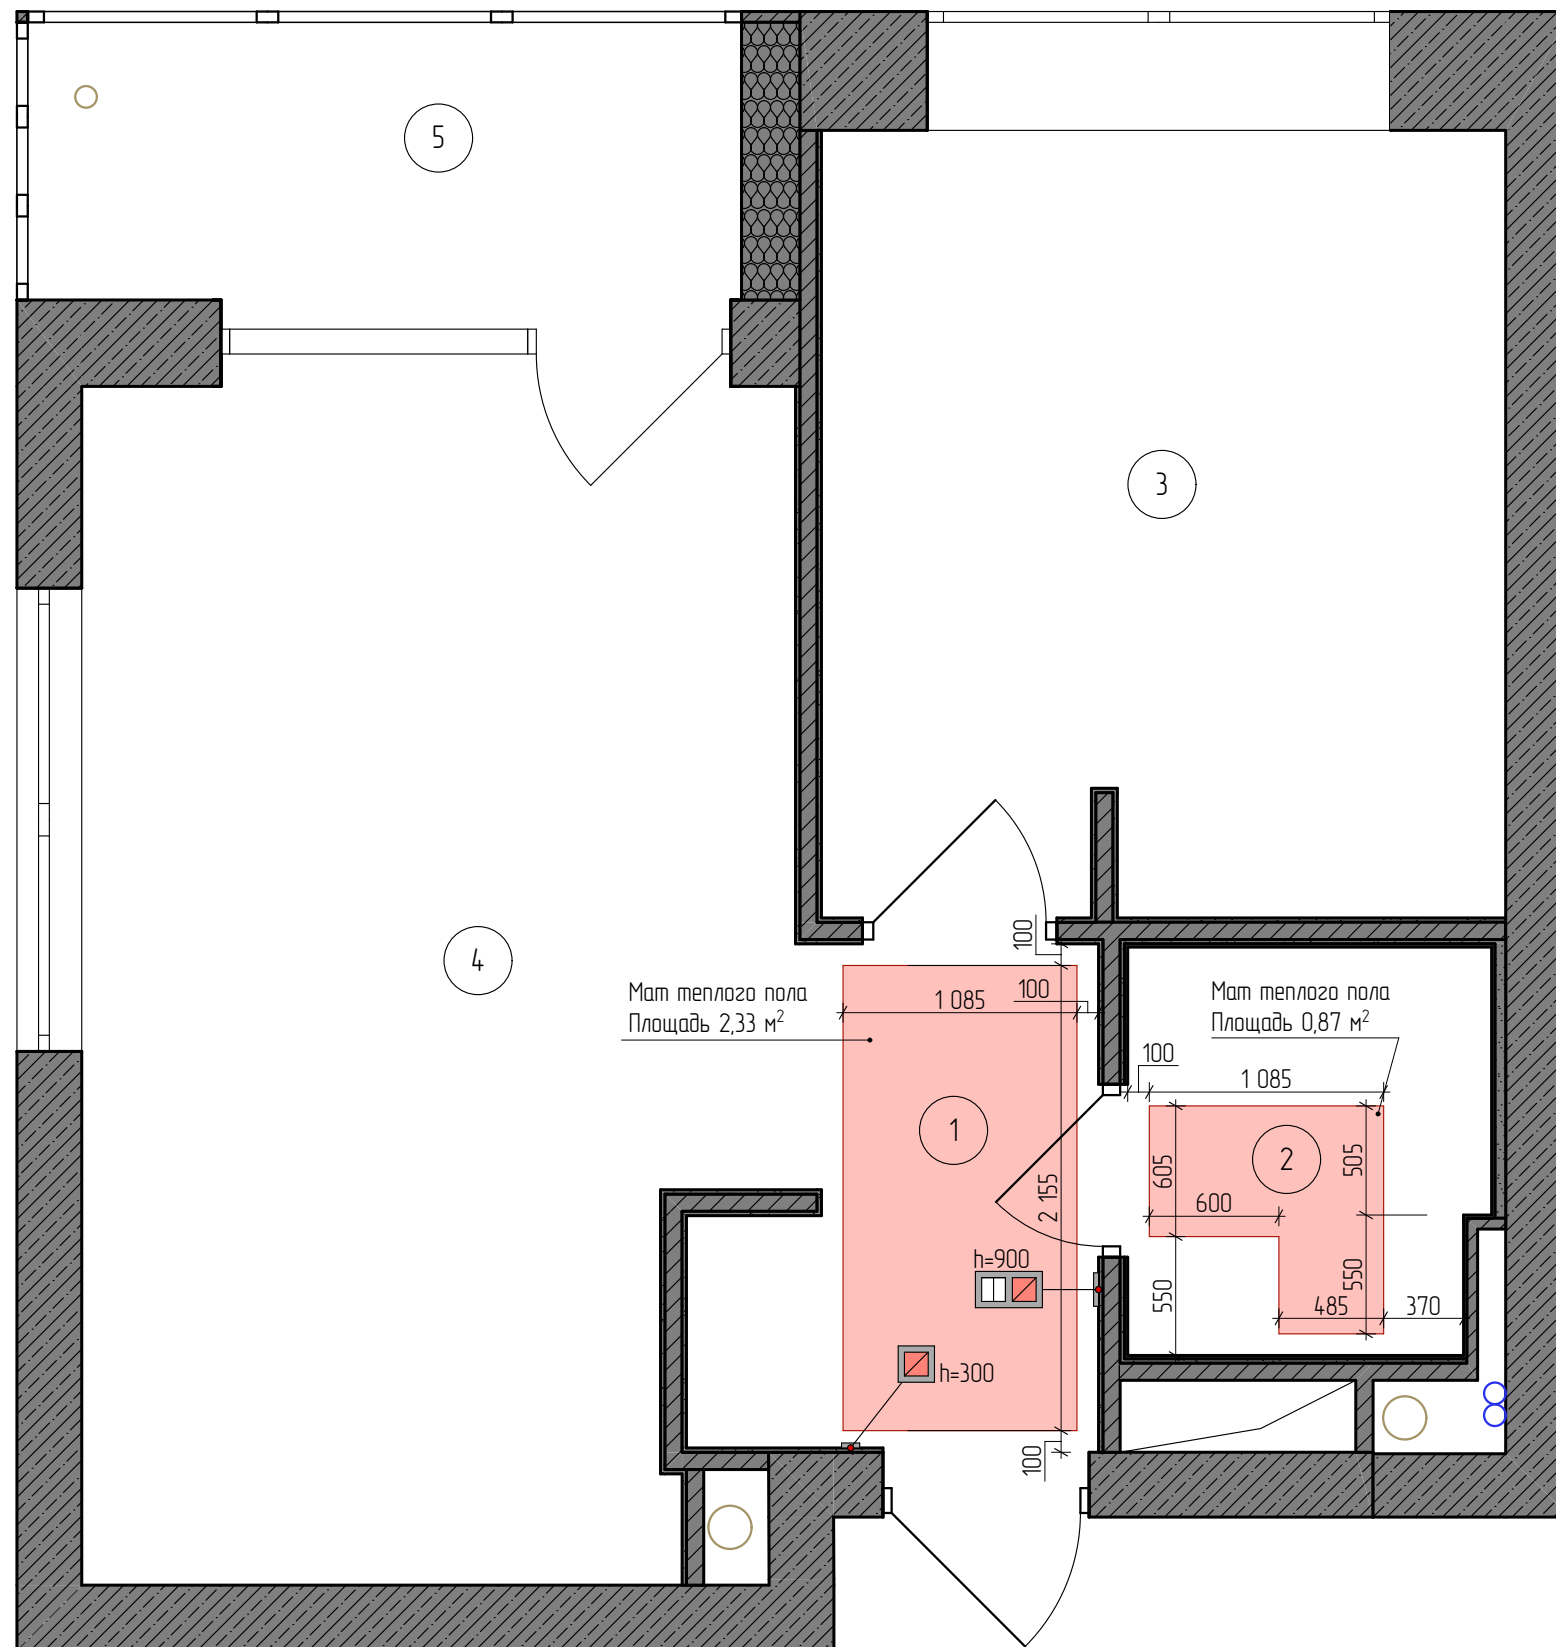

Экспликация помещений

№	Наименование	Площадь, кв.м.
1	Прихожая	3,97
2	Санузел	3,77
3	Спальня	11,68
4	Кухня - гостиная	17,60
5	Балкон	4,25
		41,27 м²

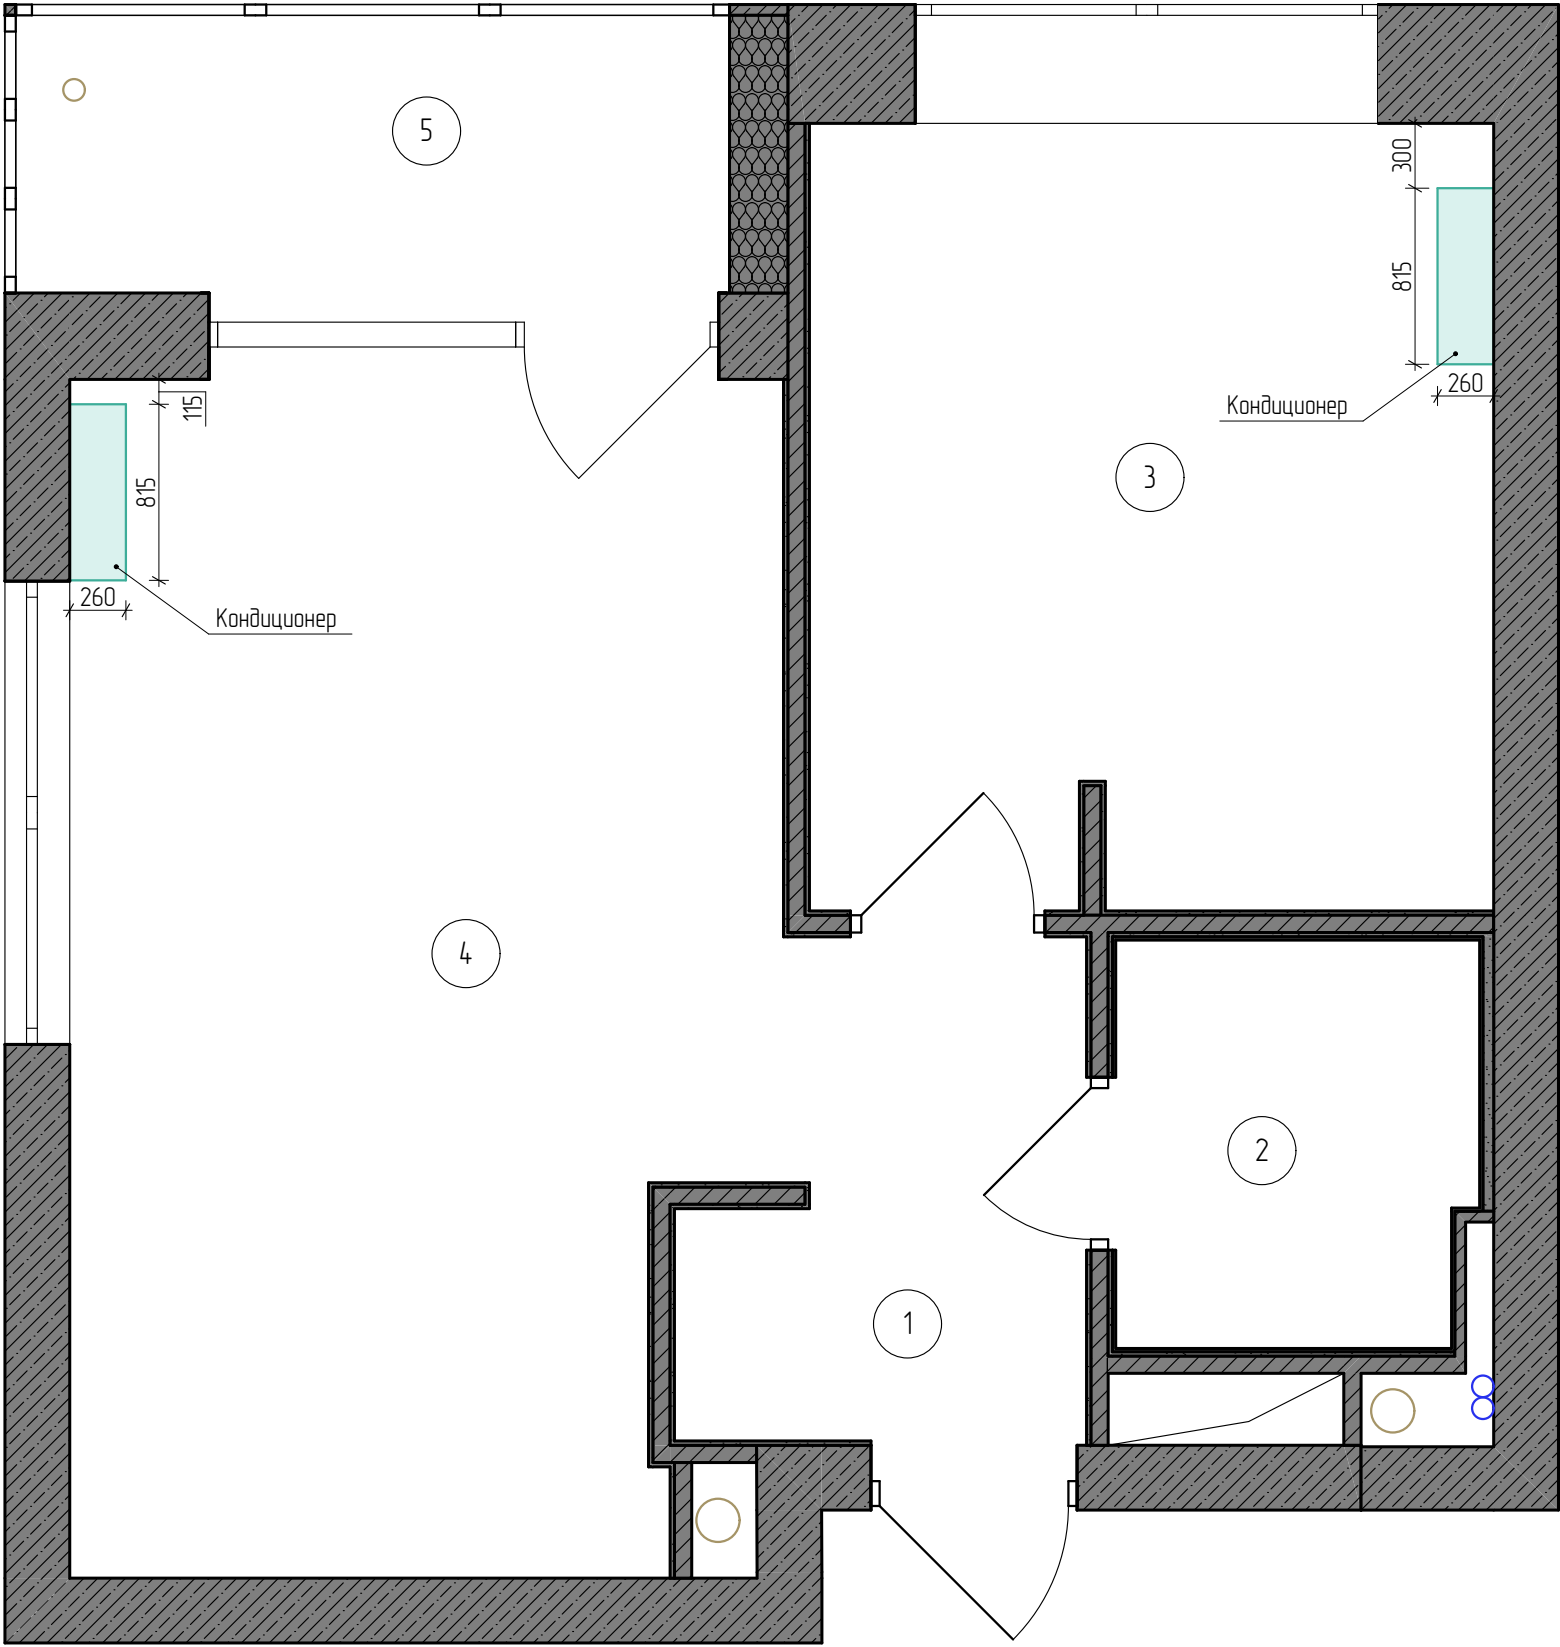

Дизайн проект

Разработал	Соколов Н.Е.	Подпись	Дата	Квартира
Заказчик	Середин Д.П.			Жк Аквилон beside

ПЛАН КОНДИЦИОНИРОВАНИЯ

Стадия	Лист	Масштаб
ДП	17	1:40

ПЛАН ОТДЕЛКИ ПОТОЛКОВ

Экспликация помещений


№	Наименование	Площадь, кв.м.
1	Прихожая	3,97
2	Санузел	3,77
3	Спальня	11,68
4	Кухня - гостиная	17,60
5	Балкон	4,25
		41,27 м²

Спецификация отделки потолка

Условное обозначение	Марка	Тип	Площадь, м²
	П1	Натяжной потолок	37,62

Спецификация потолочных элементов

Условное обозначение	Марка	Наименование	Площадь, м²
	П2	Ниша для штор 150мм	1,65
	П3	Ниша для подсветки 60 мм	0,64

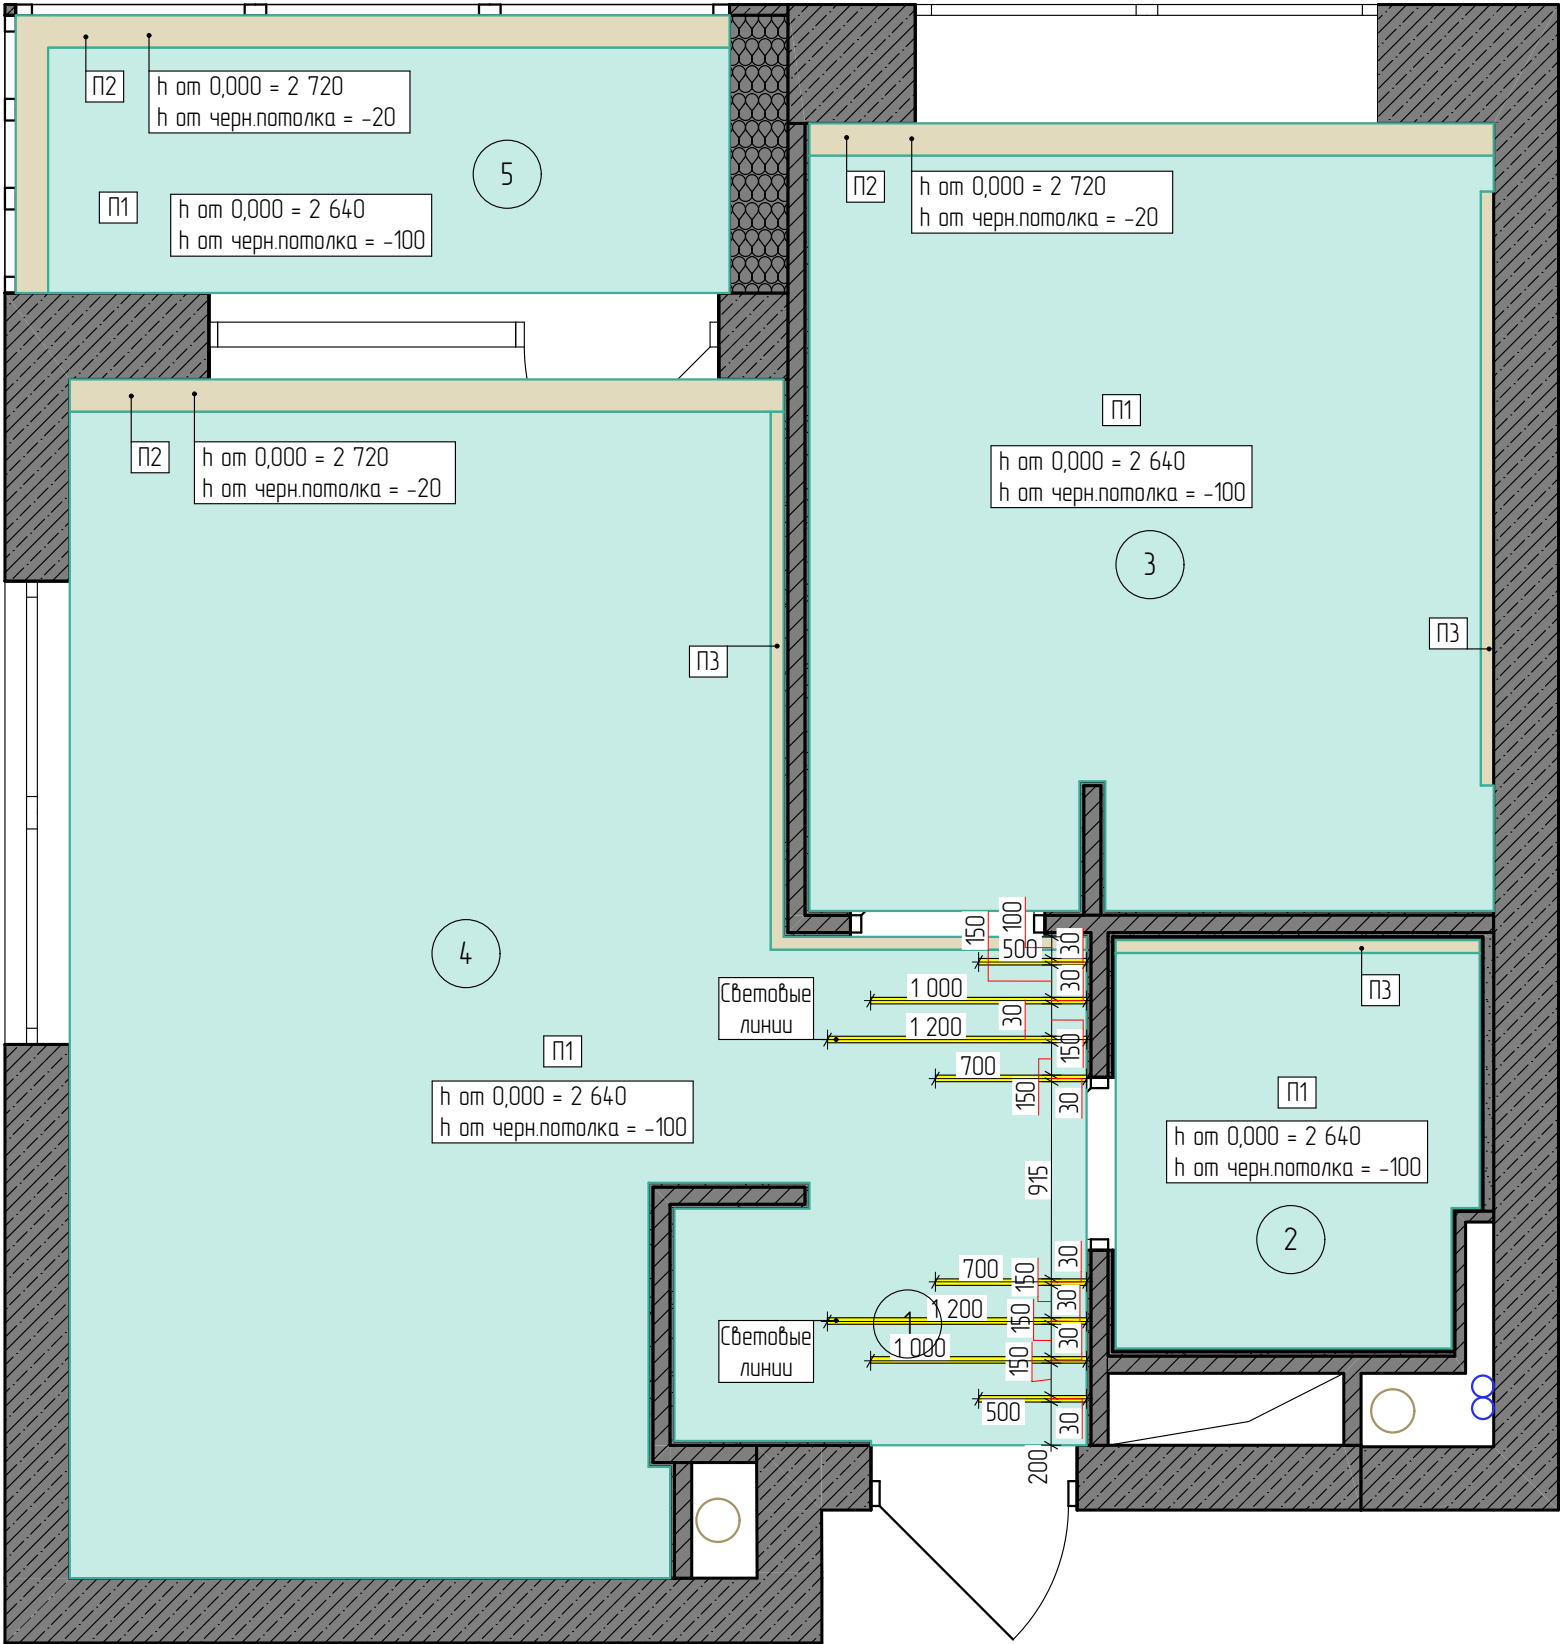


Дизайн проект

		Подпись	Дата	Квартира
Разработал	Соколов Н.Е.			Жк Аквилон beside
Заказчик	Середин Д.П.			

ПЛАН ОТДЕЛКИ ПОТОЛКОВ

Стадия	Лист	Масштаб
ДП	18	1:40

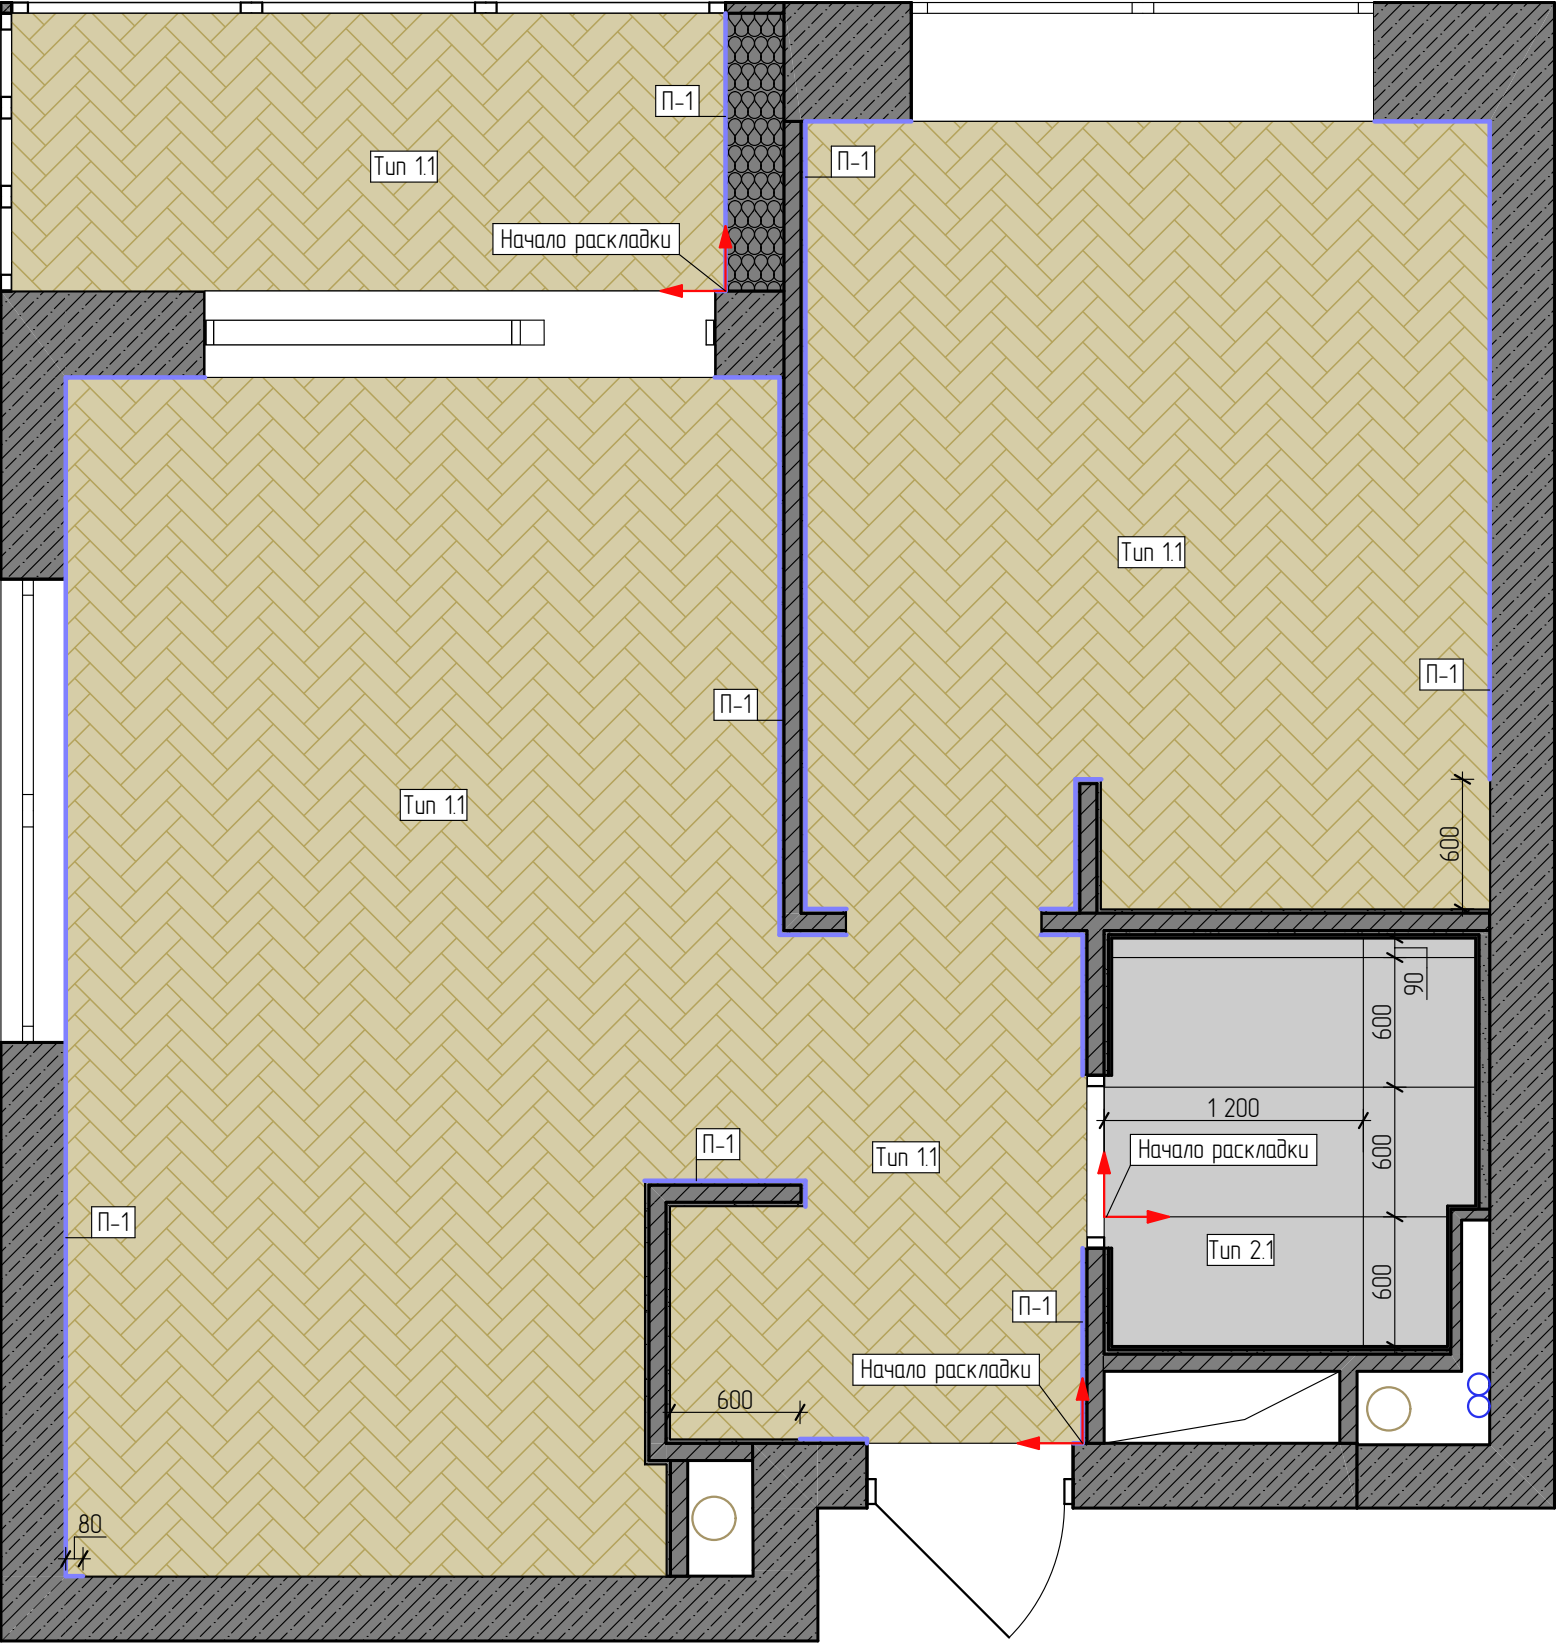

Кол-во плитки

Условное обозначение	Марка	Наименование	Кол-во, мм
	П-1	Плитка	22 580

Напольные покрытия

Условное обозначение	Тип	Наименование	Площадь, м²
	Тип 1.1	Кварцвинил	36,91
	Тип 2.1	Керамогранит 120*60	3,13


ПЛАН ОТДЕЛКИ СТЕН

Экспликация помещений

№	Наименование	Площадь, кв.м.
1	Прихожая	3,97
2	Санузел	3,77
3	Спальня	11,68
4	Кухня - гостиная	17,60
5	Балкон	4,25
		41,27 м²

Спецификация отделки стен

Условное обозначение	Тип	Наименование	Площадь, м²
—	Тип 1	Обои под покраску	95,33
—	Тип 2	Керамогранит 120*60	18,07
—	Тип 3	Керамогранит 120*60	2,01

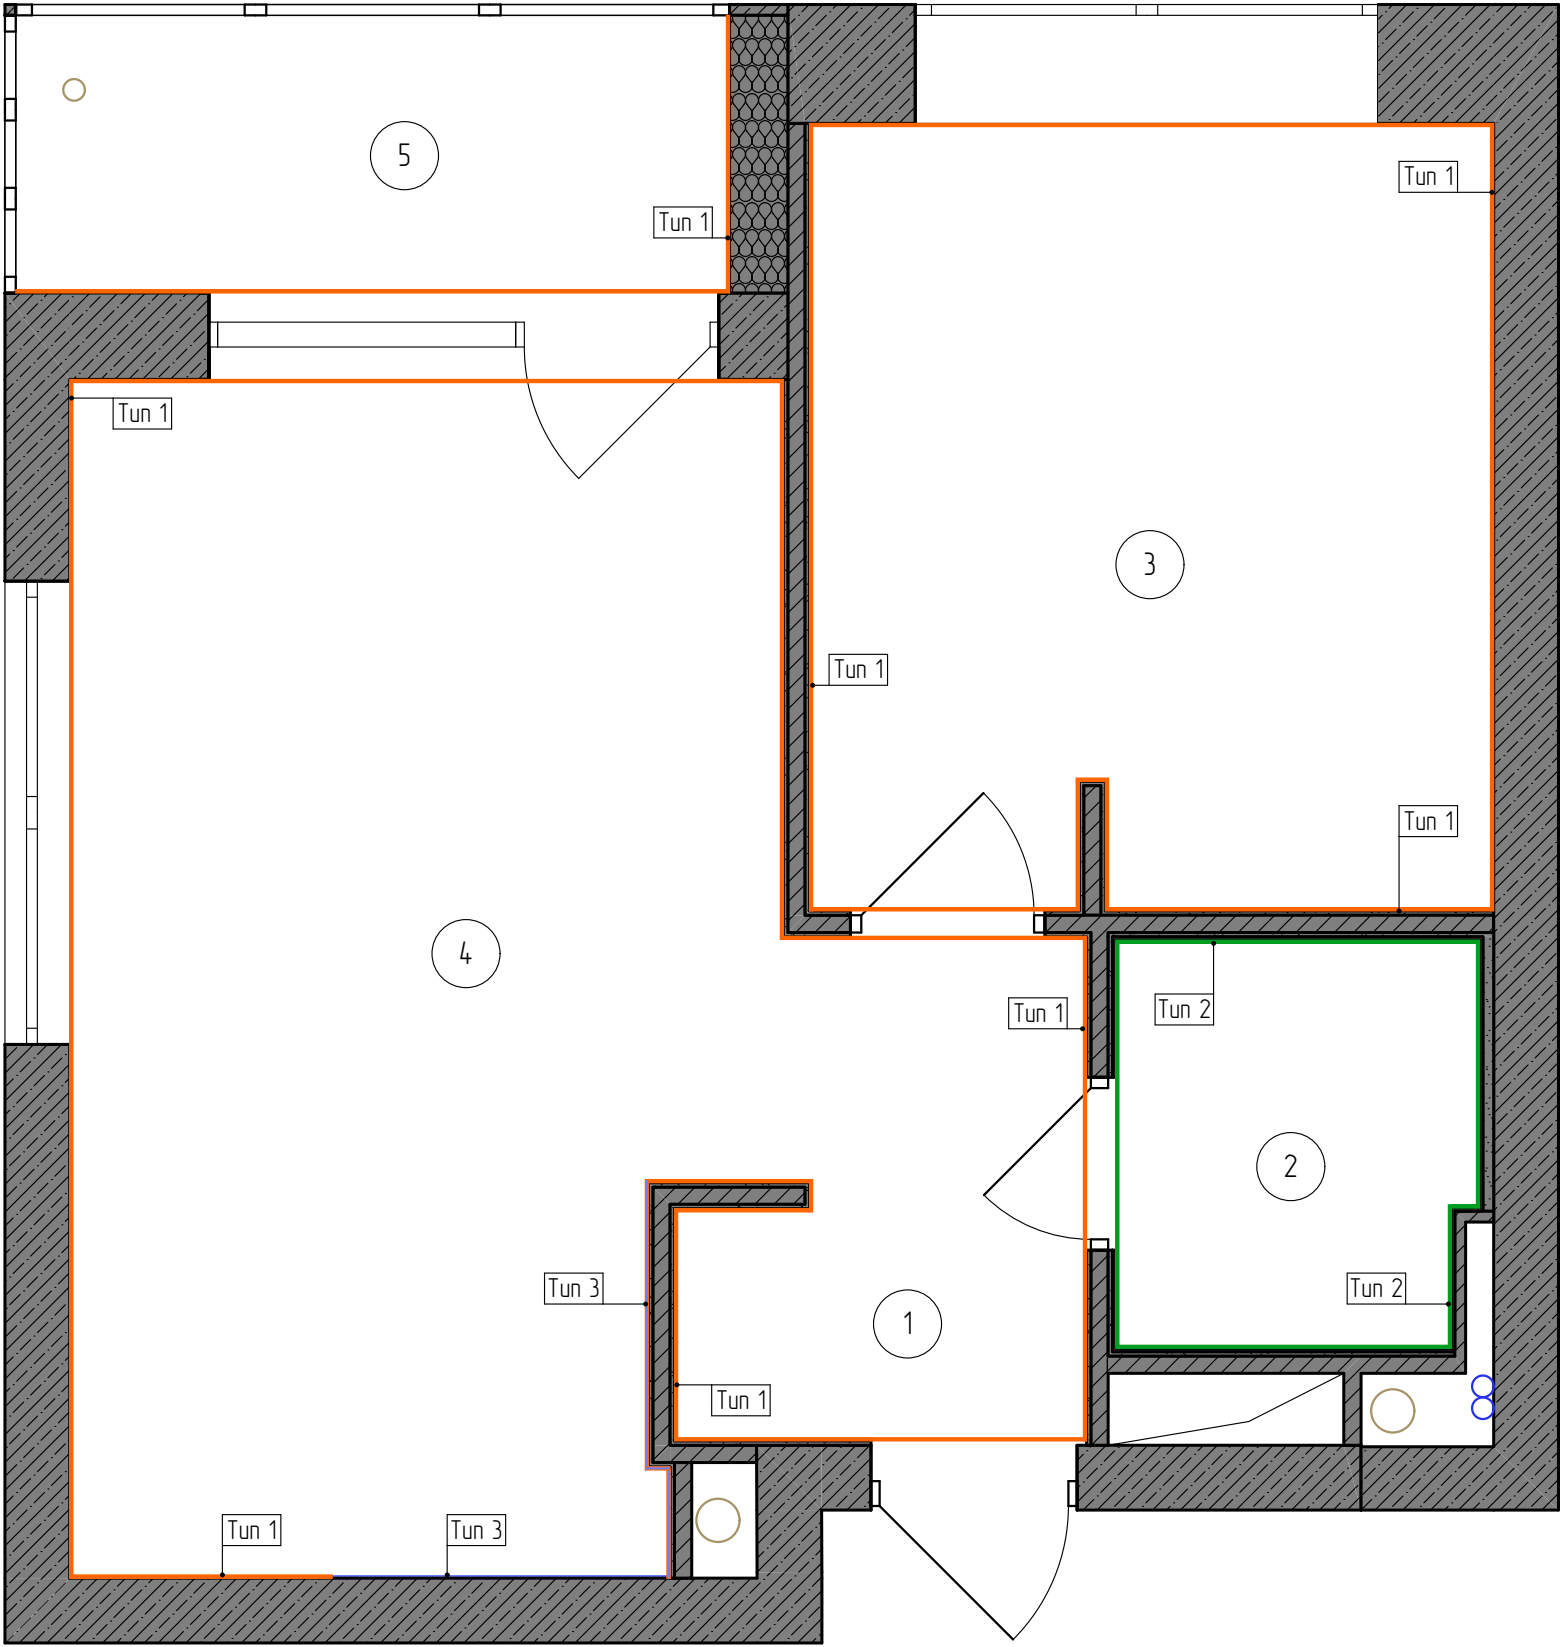

Дизайн проект

Разработал	Соколов Н.Е.	Подпись	Дата	Квартира
Заказчик	Середин Д.П.			Жк Аквилон beside


ПЛАН ОТДЕЛКИ СТЕН

Стадия	Лист	Масштаб
ДП	20	1:40

ПЛАН ОТКРЫВАНИЯ ДВЕРЕЙ

Экспликация помещений

№	Наименование	Площадь, кв.м.
1	Прихожая	3,97
2	Санузел	3,77
3	Спальня	11,68
4	Кухня - гостиная	17,60
5	Балкон	4,25
		41,27 м²

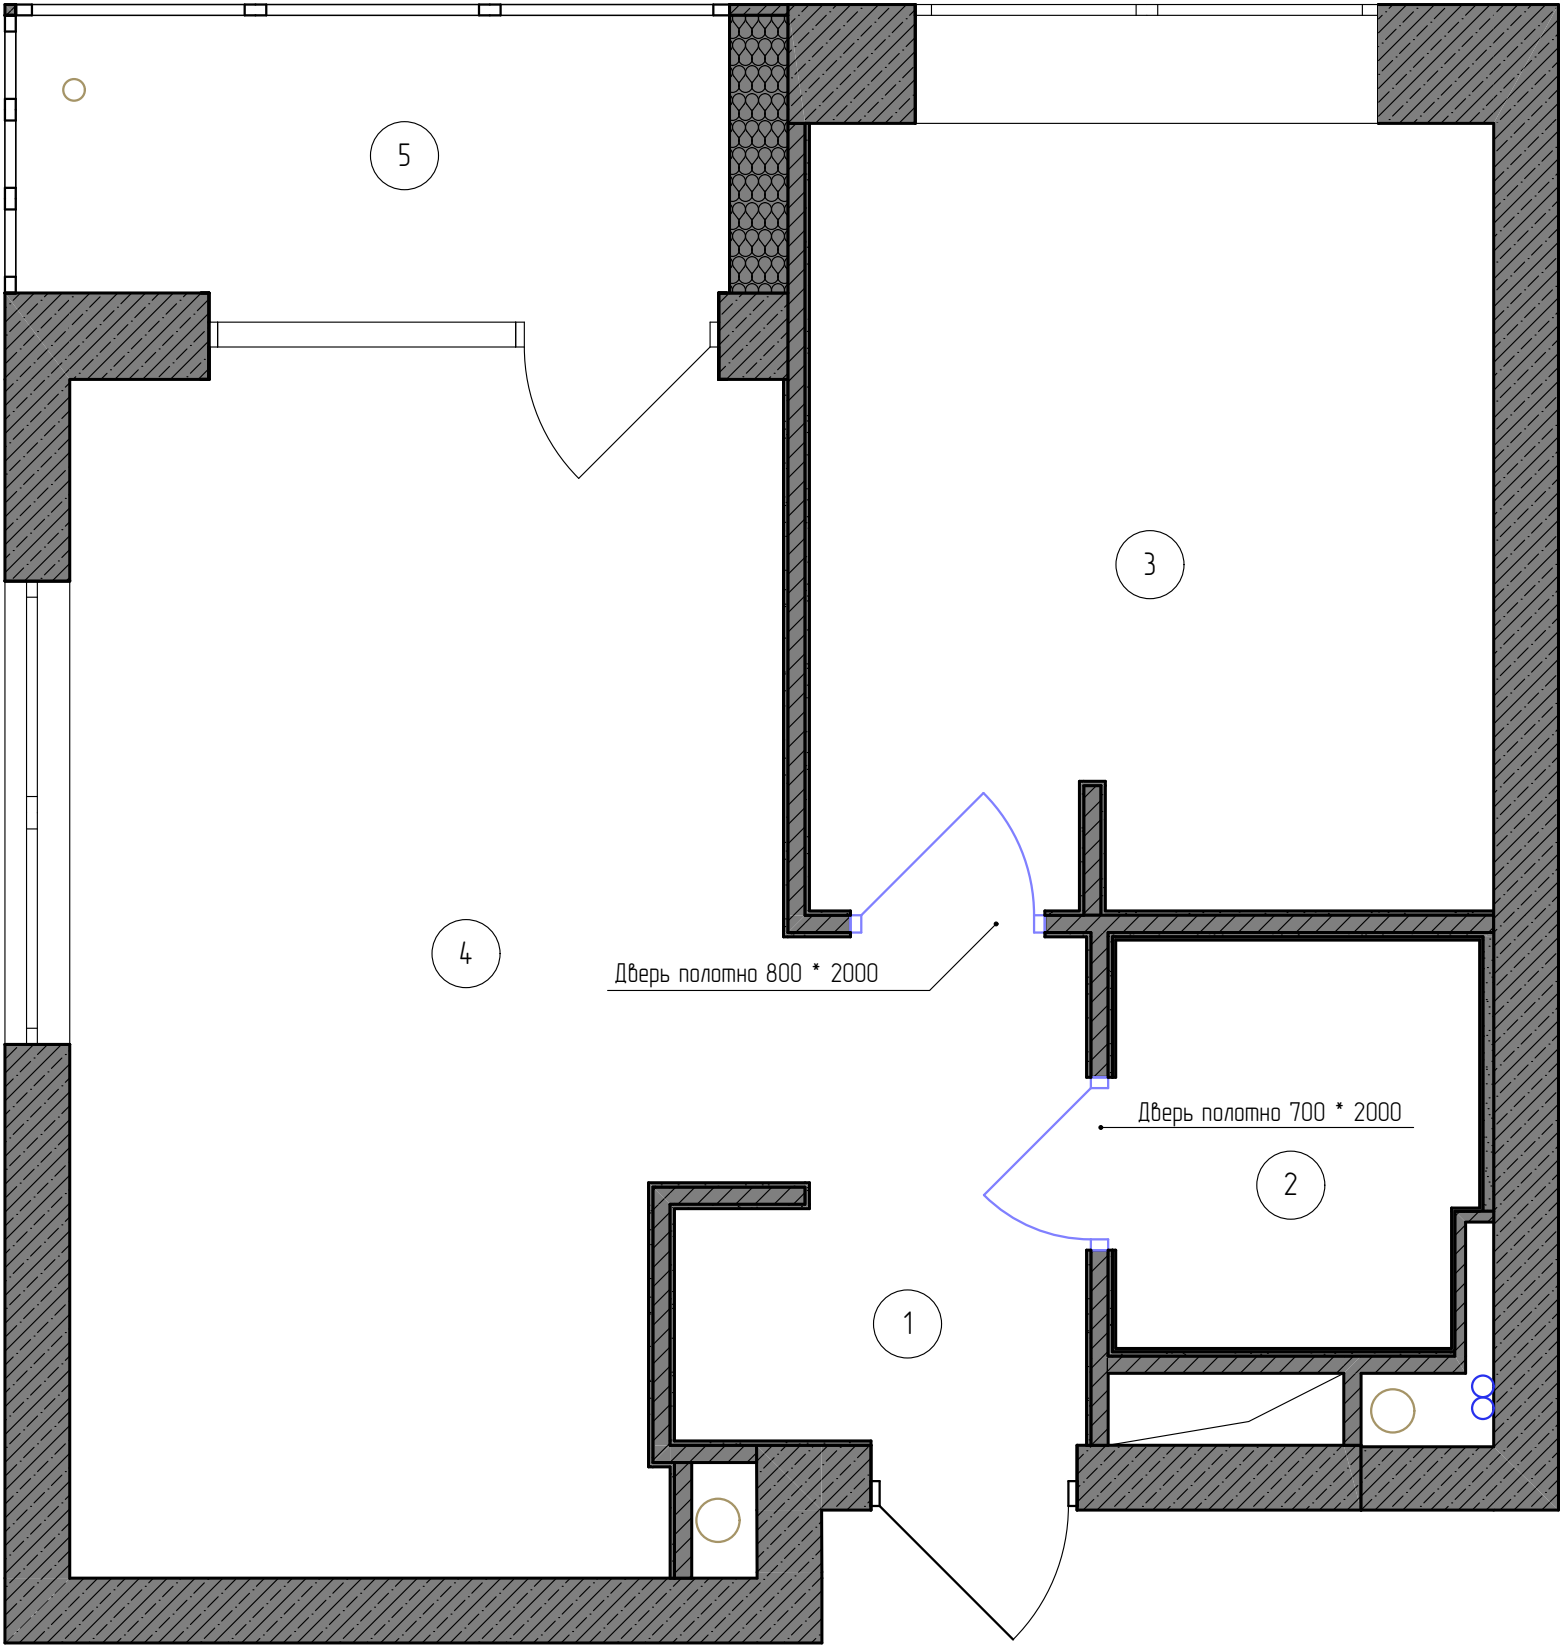



Дизайн проект

		Подпись	Дата	Квартира Жк Аквилон beside
Разработал	Соколов Н.Е.			
Заказчик	Середин Д.П.			

ПЛАН ОТКРЫВАНИЯ ДВЕРЕЙ

Стадия	Лист	Масштаб
ДП	21	1:40

РАЗВЕРТКИ ПРИХОЖЕЙ

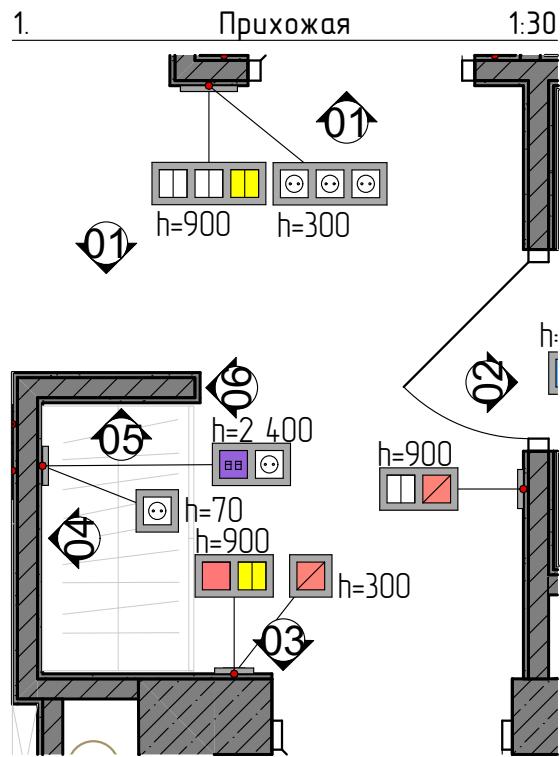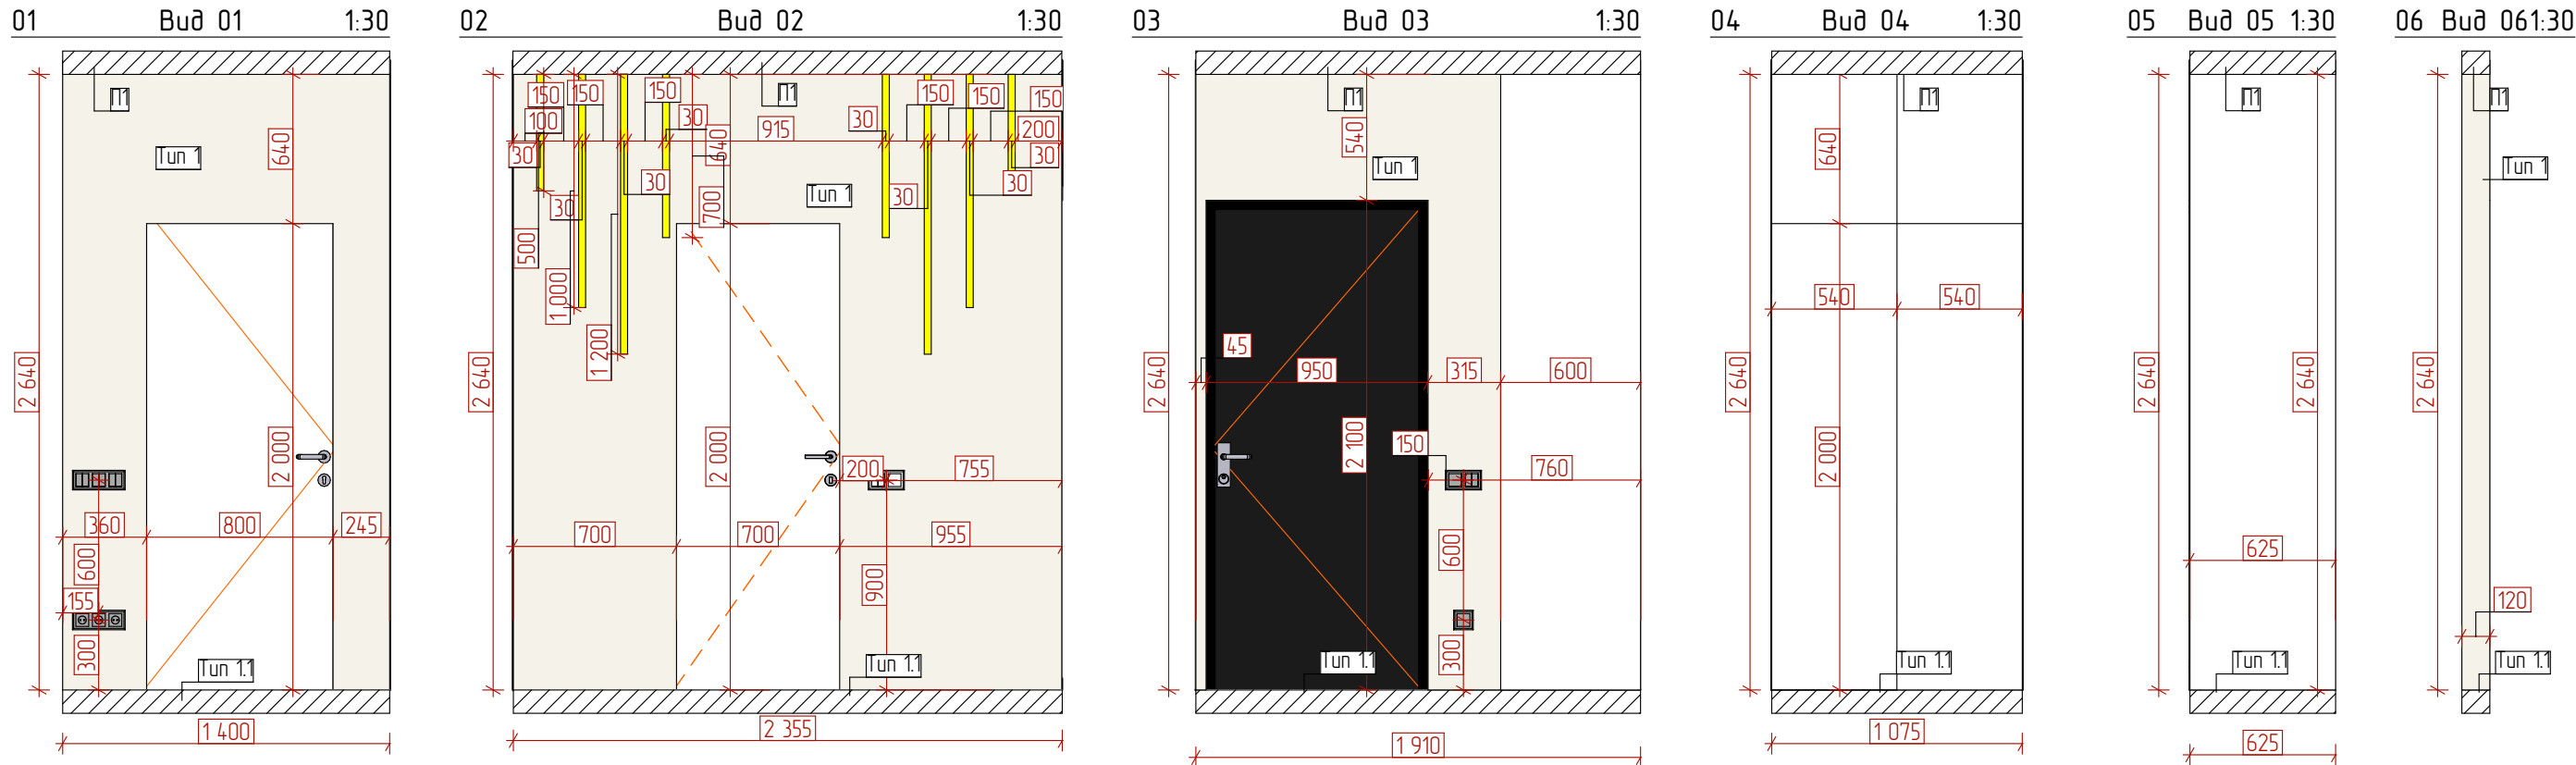

Дизайн проект

Разработал Заказчик	Соколов Н.Е. Середин Д.П.	Подпись	Дата	Квартира Жк Аквилон beside

РАЗВЕРТКИ ПРИХОЖЕЙ

Стадия	Лист	Масштаб
ДП	22	1:40



Дизайн проект			Подпись	Дата	Квартира Жк Аквилон beside	ВИЗУАЛИЗАЦИИ ПРИХОЖЕЙ	Стадия	Лист	Масштаб
	Разработал	Соколов Н.Е.					ДП	23	1:40
	Заказчик	Середин Д.П.							



Дизайн проект

		Підпись	Дата	Квартира Жк Аквилон beside
Разроботал	Соколов Н.Е.			
Заказчик	Середин Д.П.			

ВИЗУАЛІЗАЦІЇ ПРИХОЖЕЙ

Стадия	Лист	Масштаб
ДП	24	1:40

Дизайн проект

		Подпись	Дата
Разработал	Соколов Н.Е.		
Заказчик	Середин Д.П.		

Квартира
Жк Аквилон beside

РАЗВЕРТКИ САНУЗЛА

Стадия	Лист	Масштаб
ДП	25	1:40



Дизайн проект

		Подпись	Дата	Квартира Жк Аквилон beside
Разработал	Соколов Н.Е.			
Заказчик	Середин Д.П.			

ВИЗУАЛИЗАЦИИ САНУЗЛА

Стадия	Лист	Масштаб
ДП	26	1:40












Дизайн проект

		Подпись	Дата	Квартира Жк Аквилон beside
Разработал	Соколов Н.Е.			
Заказчик	Середин Д.П.			

ВИЗУАЛИЗАЦИИ САНУЗЛА

Стадия	Лист	Масштаб
ДП	27	1:40

РАЗВЕРТКИ СПАЛЬНИ

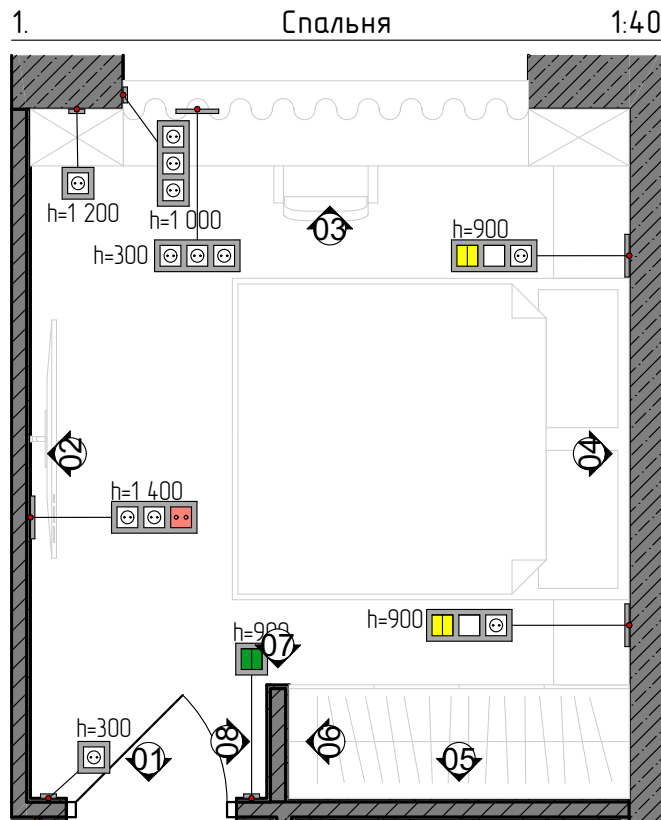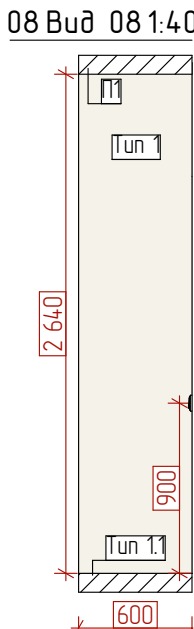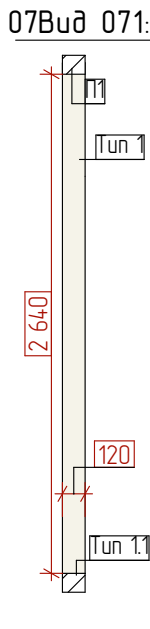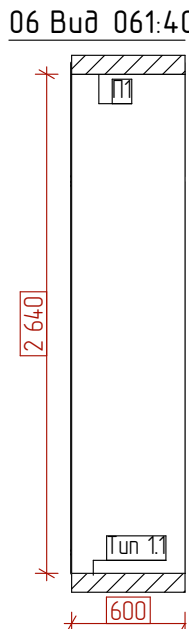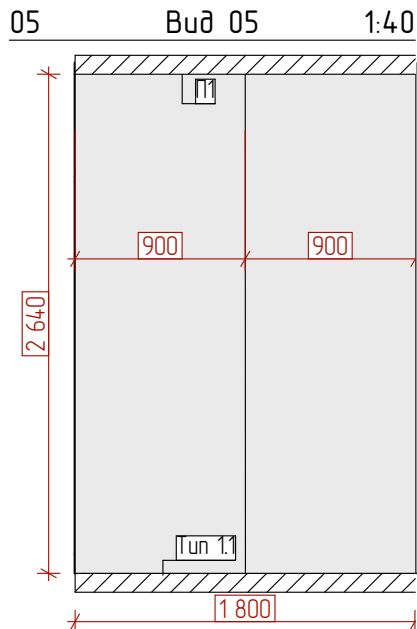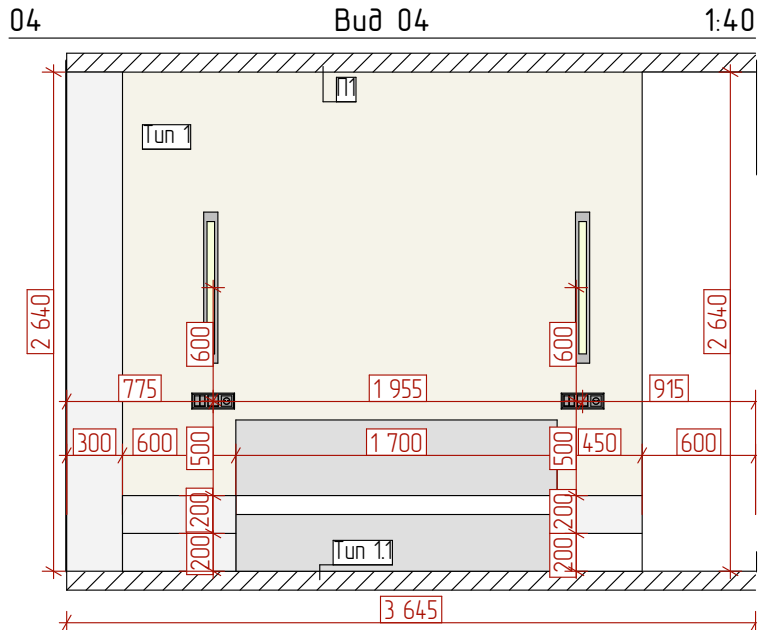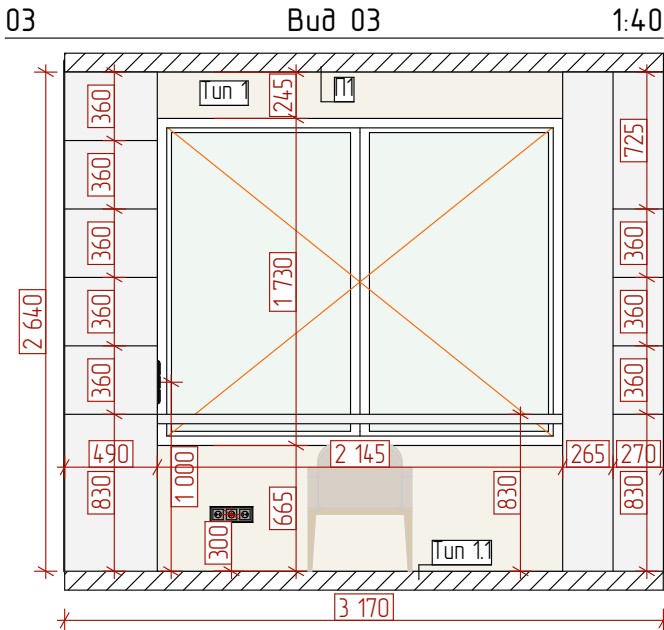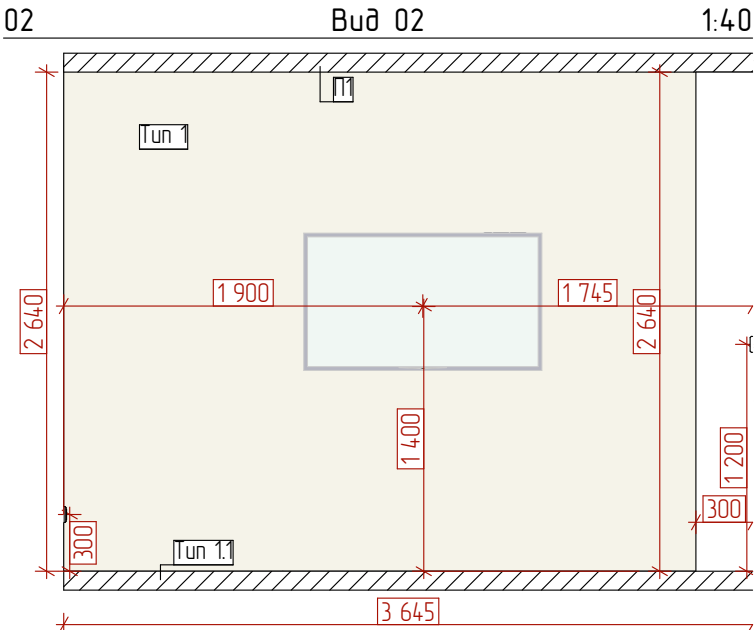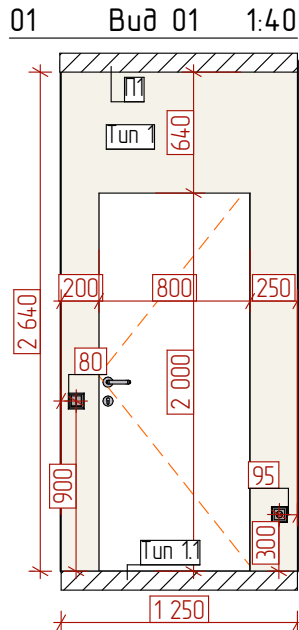



Дизайн проект

		Подпись	Дата	Квартира Жк Аквилон beside
Разработал	Соколов Н.Е.			
Заказчик	Середин Д.П.			

ВИЗУАЛИЗАЦИИ СПАЛЬНИ

Стадия	Лист	Масштаб
ДП	29	1:40



Дизайн проект


		Подпись	Дата	Квартира Жк Аквилон beside
Разработал	Соколов Н.Е.			
Заказчик	Середин Д.П.			

ВИЗУАЛИЗАЦИИ СПАЛЬНИ


Стадия	Лист	Масштаб
ДП	30	1:40

РАЗВЕРТКИ КУХНИ-ГОСТИНОЙ


01 Вид 01:40

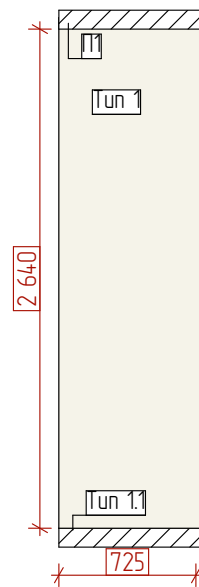


02 Вид 02 1:40

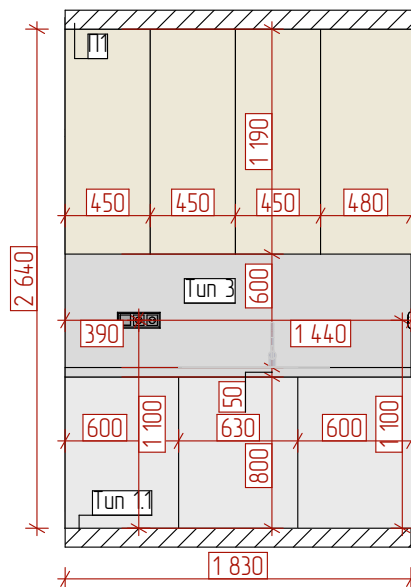


03 Вид 03 1:40

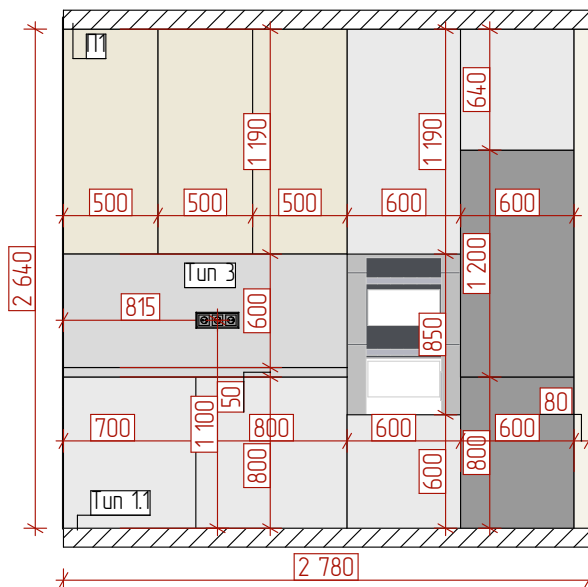


04 Вид 04 1:40

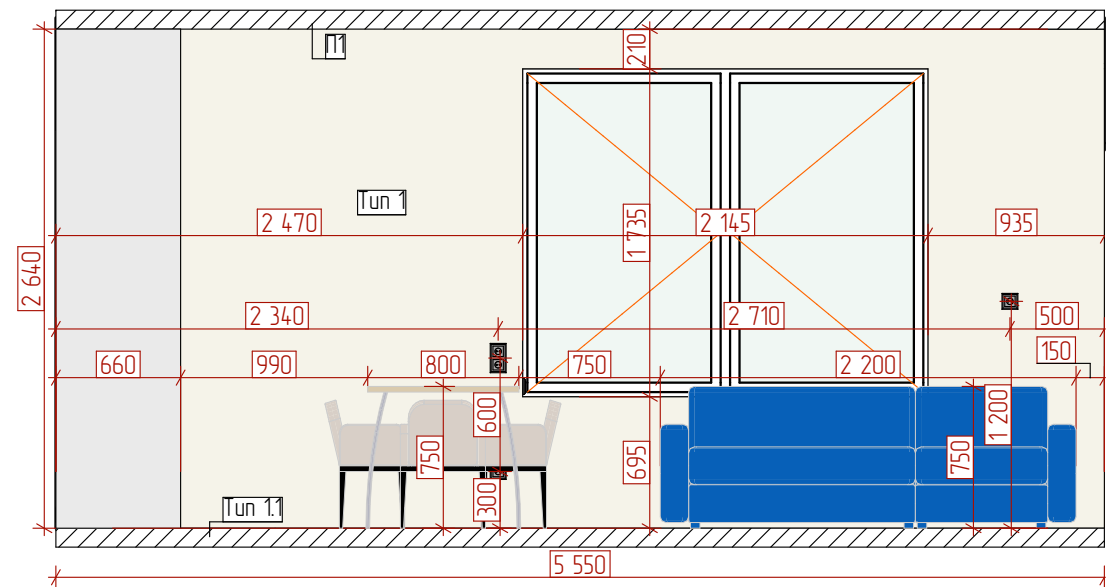


05 Вид 05 1:40

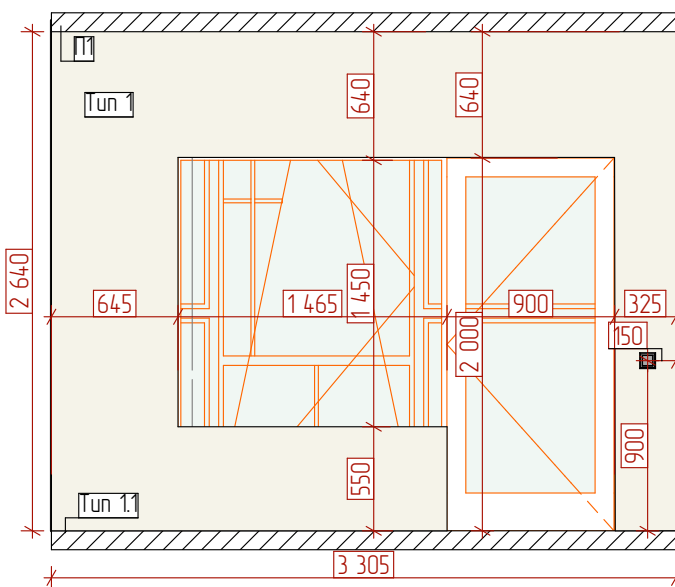

06 Вид 06 1:40

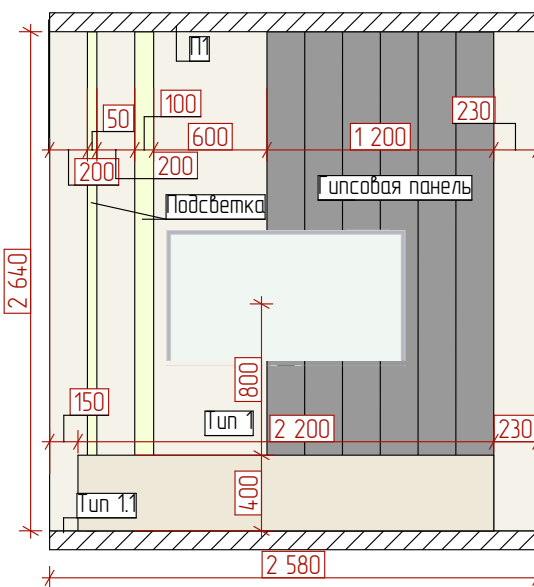

1. Кухня - гостиная 1:60

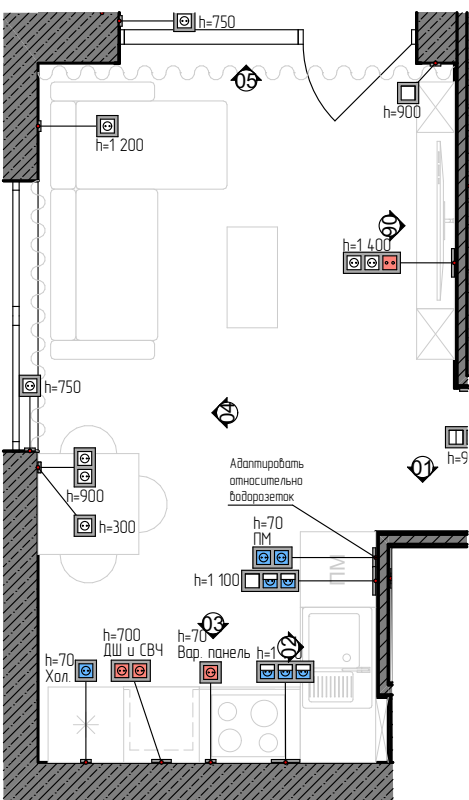

Дизайн проект

Разработал
Заказчик

Подпись

Дата

Квартира
Жк Аквилон beside

РАЗВЕРТКИ КУХНИ-ГОСТИНОЙ

Стадия

ДП

Лист

31

Масштаб

1:40



Дизайн проект

		Подпись	Дата	Квартира Жк Аквилон beside
Разработал	Соколов Н.Е.			
Заказчик	Середин Д.П.			

ВИЗУАЛИЗАЦИИ КУХНИ-ГОСТИНОЙ

Стадия	Лист	Масштаб
ДП	32	1:40



Дизайн проект

		Подпись	Дата	Квартира Жк Аквилон beside
Разработал	Соколов Н.Е.			
Заказчик	Середин Д.П.			

ВИЗУАЛИЗАЦИИ КУХНИ-ГОСТИНОЙ

Стадия	Лист	Масштаб
ДП	33	1:40



Дизайн проект

		Подпись	Дата	Квартира Жк Аквилон beside
Разработал	Соколов Н.Е.			
Заказчик	Середин Д.П.			

ВИЗУАЛИЗАЦИИ КУХНИ-ГОСТИНОЙ

Стадия	Лист	Масштаб
ДП	34	1:40



Дизайн проект

		Подпись	Дата	Квартира Жк Аквилон beside
Разработал	Соколов Н.Е.			
Заказчик	Середин Д.П.			

ВИЗУАЛИЗАЦИИ КУХНИ-ГОСТИНОЙ

Стадия	Лист	Масштаб
ДП	35	1:40







Дизайн проект

		Подпись	Дата	Квартира Жк Аквилон beside
Разработал	Соколов Н.Е.			
Заказчик	Середин Д.П.			

ВИЗУАЛИЗАЦИИ КУХНИ-ГОСТИНОЙ

Стадия	Лист	Масштаб
ДП	36	1:40

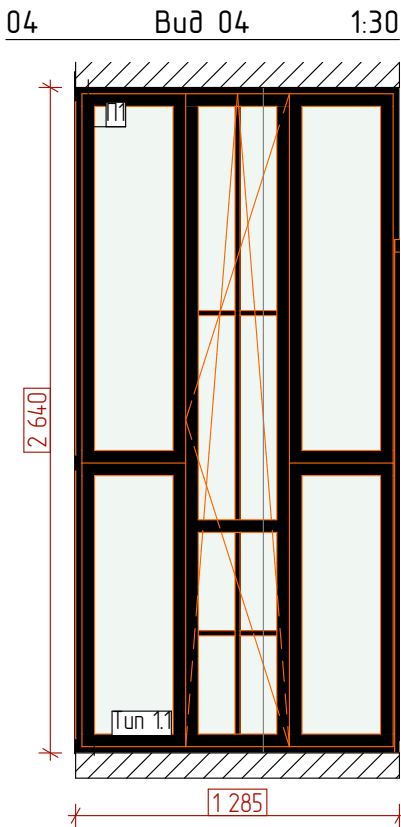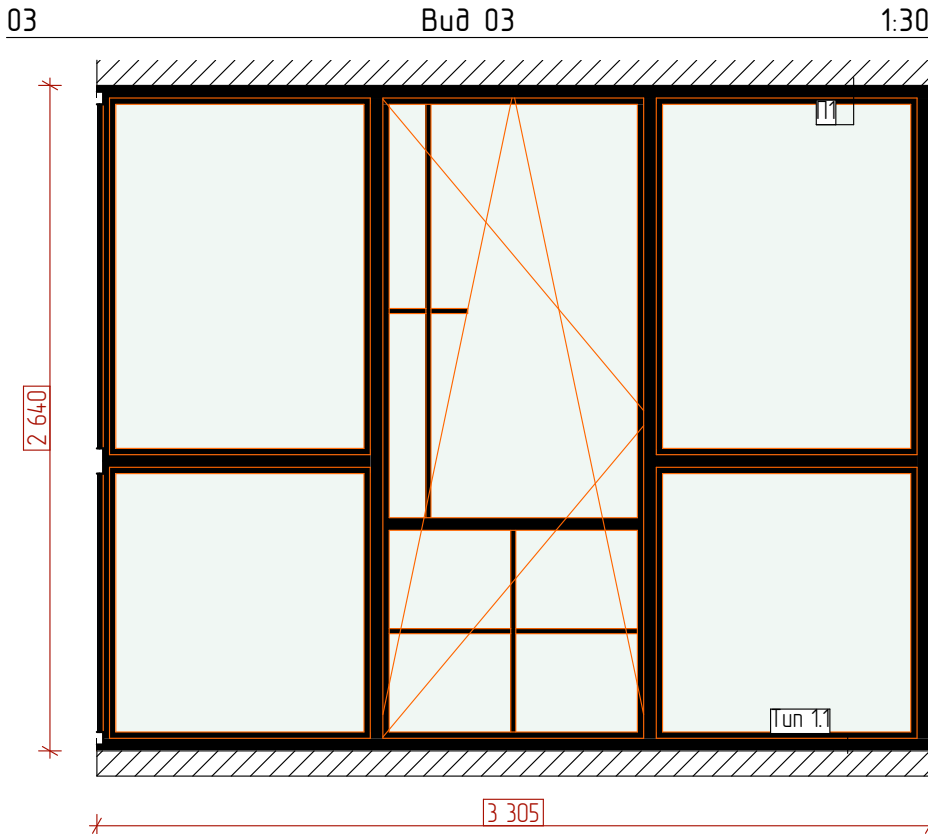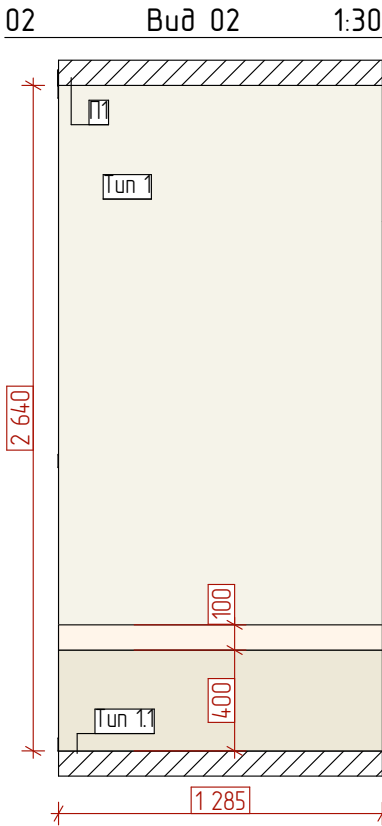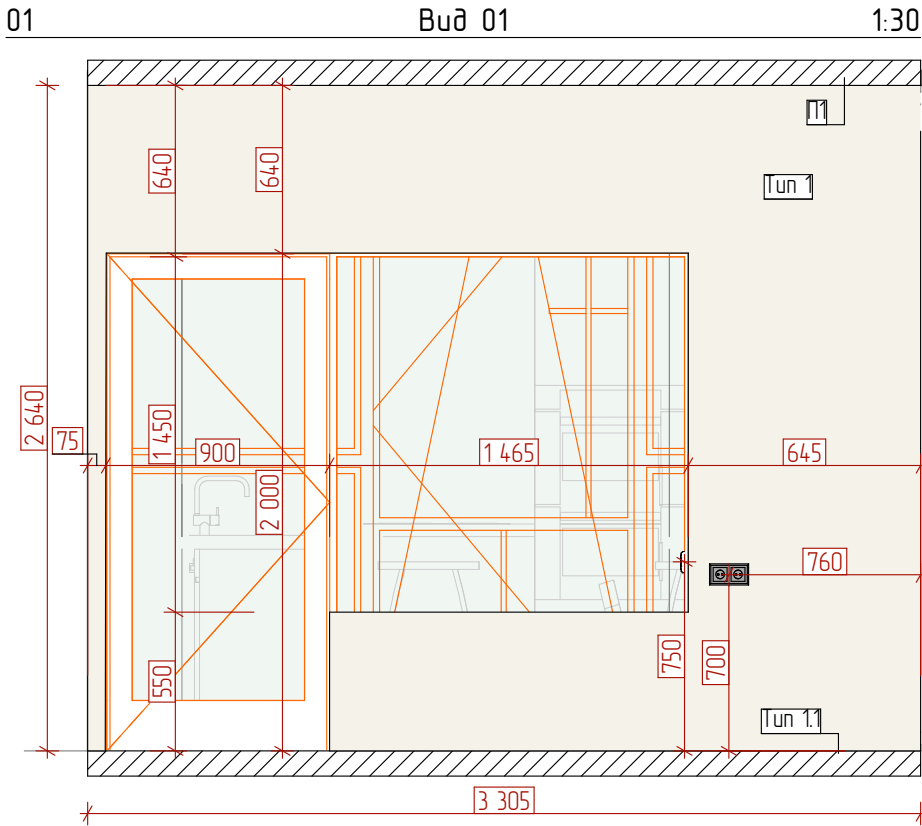

Дизайн проект

Разработал	Соколов Н.Е.	Подпись	Дата	Квартира
Заказчик	Середин Д.П.			Жк Аквилон beside

РАЗВЕРТКИ БАЛКОНА

Стадия	Лист	Масштаб
ДП	37	1:40



Дизайн проект

		Підпись	Дата	Квартира Жк Аквилон beside
Розроботал	Соколов Н.Е.			
Заказчик	Середин Д.П.			

ВИЗУАЛІЗАЦІ БАЛКОНА

Стадия	Лист	Масштаб
ДП	38	1:40