

ДИЗЙН ПРОЕКТ

АВТОРСКИЙ

ЖК КИНЕТИК
ДМИТРОВСКОЕ ШОССЕ
Д. 75/77, КВ. 205



Лист	Наименование	Примечание
01	ОБЛОЖКА	
02	ВЕДОМОСТЬ ЧЕРТЕЖЕЙ	
03	ПОЯСНИТЕЛЬНАЯ ЗАПИСКА	
04	ОБМЕРНЫЙ ПЛАН	
05	ДЕМОНТАЖНЫЙ ПЛАН	
06	МОНТАЖНЫЙ ПЛАН	
07	ПЛАН ПОСЛЕ ПЕРЕПЛАНИРОВКИ	
08	ПЛАН РАССТАНОВКИ МЕБЕЛИ И ОБОРУДОВАИЯ	
09	ПЛАН РАССТАНОВКИ МЕБЕЛИ И ОБОРУДОВАИЯ (РАЗМЕРЫ)	
10	СХЕМА УКАЗАНИЯ ПОДКЛЮЧЕНИЯ САНТЕХНИКИ	
11	ПЛАН РОЗЕТОК И ВЫКЛЮЧАТЕЛЕЙ (ПРИВЯЗКИ)	
12	ПЛАН РОЗЕТОК И ВЫКЛЮЧАТЕЛЕЙ (РАЗМЕРЫ)	
13	СПЕЦИФИКАЦИЯ ЭЛЕКТРООБОРУДОВАНИЯ	
14	ПЛАН РАССТАНОВКИ СВЕТИЛЬНИКОВ	
15	ПЛАН УПРАВЛЕНИЯ ОСВЕЩЕНИЕМ	
16	ПЛАН ТЕПЛОГО ПОЛА	
17	СХЕМА КОНДИЦИОНИРОВАНИЯ	
18	ПЛАН ОТДЕЛКИ ПОТОЛКОВ	
19	ПЛАН НАПОЛЬНЫХ ПОКРЫТИЙ	
20	ПЛАН ОТДЕЛКИ СТЕН	
21	ПЛАН ОТКРЫВАНИЯ ДВЕРЕЙ	
22	РАЗВЕРТКИ ПРИХОЖЕЙ	
23	ВИЗУАЛИЗАЦИЯ ПРИХОЖЕЙ	
24	РАЗВЕРТКИ САНУЗЛА	
25	ВИЗУАЛИЗАЦИЯ САНУЗЛА	
26	ВИЗУАЛИЗАЦИЯ САНУЗЛА	
27	РАЗВЕРТКИ КУХНИ	
28	ВИЗУАЛИЗАЦИЯ КУХНИ	

Лист	Наименование	Примечание
29	ВИЗУАЛИЗАЦИЯ КУХНИ	
30	РАЗВЕРТКИ ГОСТИНОЙ	
31	ВИЗУАЛИЗАЦИЯ ГОСТИНОЙ	
32	ВИЗУАЛИЗАЦИЯ ГОСТИНОЙ	
33	ВИЗУАЛИЗАЦИЯ СТОЛОВОЙ	
34	РАЗВЕРТКИ МАСТЕР СПАЛЬНИ	
35	ВИЗУАЛИЗАЦИЯ МАСТЕР СПАЛЬНИ	
36	ВИЗУАЛИЗАЦИЯ МАСТЕР СПАЛЬНИ	
37	РАЗВЕРТКИ МАСТЕР САНУЗЛА	
38	ВИЗУАЛИЗАЦИЯ МАСТЕР САНУЗЛА	
39	РАЗВЕРТКИ ДЕТСКОЙ 1	
40	ВИЗУАЛИЗАЦИЯ ДЕТСКОЙ 1	
41	ВИЗУАЛИЗАЦИЯ ДЕТСКОЙ 1	
42	РАЗВЕРТКИ ДЕТСКОЙ 2	
43	ВИЗУАЛИЗАЦИЯ ДЕТСКОЙ 2	
44	ВИЗУАЛИЗАЦИЯ ДЕТСКОЙ 2	

Существующее положение:

Объект строительства - квартира площадью 66.38 м² (на основании обмеров).

Монтажные работы осуществить согласно плана монтажа.

Сантехническое оборудование - разводку воды и канализации осуществить согласно инженерным проектам и техническим картам производителей на сантехоборудование.

Отделка выполняется согласно дизайн проекта с соблюдением технических условий при работе с каждым отделочным покрытием.

Замена относительно проекта строительных материалов, осветительных и сантехнических приборов влечет за собой изменения размеров, привязок и корректировки рабочей документации.

Фактические размеры могут отличаться от проектных.

За относительную отметку ±0,000 принят уровень чистого пола.

Привязки сантехнического оборудования даны от чистовой поверхности стен с учетом отделки.


Смотреть технические схемы оборудования, а также совместно с листами "Развертки стен санузла".

Расположение и привязки бытовой техники на кухне согласовать с изготовителями кухонной мебели.

Предусмотреть доступ к инженерным коммуникациям посредством лючков или другим способом.

Дизайн проект			Подпись	Дата	Квартира Жк Кинетик	ПОЯСНИТЕЛЬНАЯ ЗАПИСКА	Стадия	Лист	Масштаб
	Разработал	Соколов Н.Е.					ДП	03	1:40
	Заказчик	Шуфалова Е.Е.							

ОБМЕРНЫЙ ПЛАН

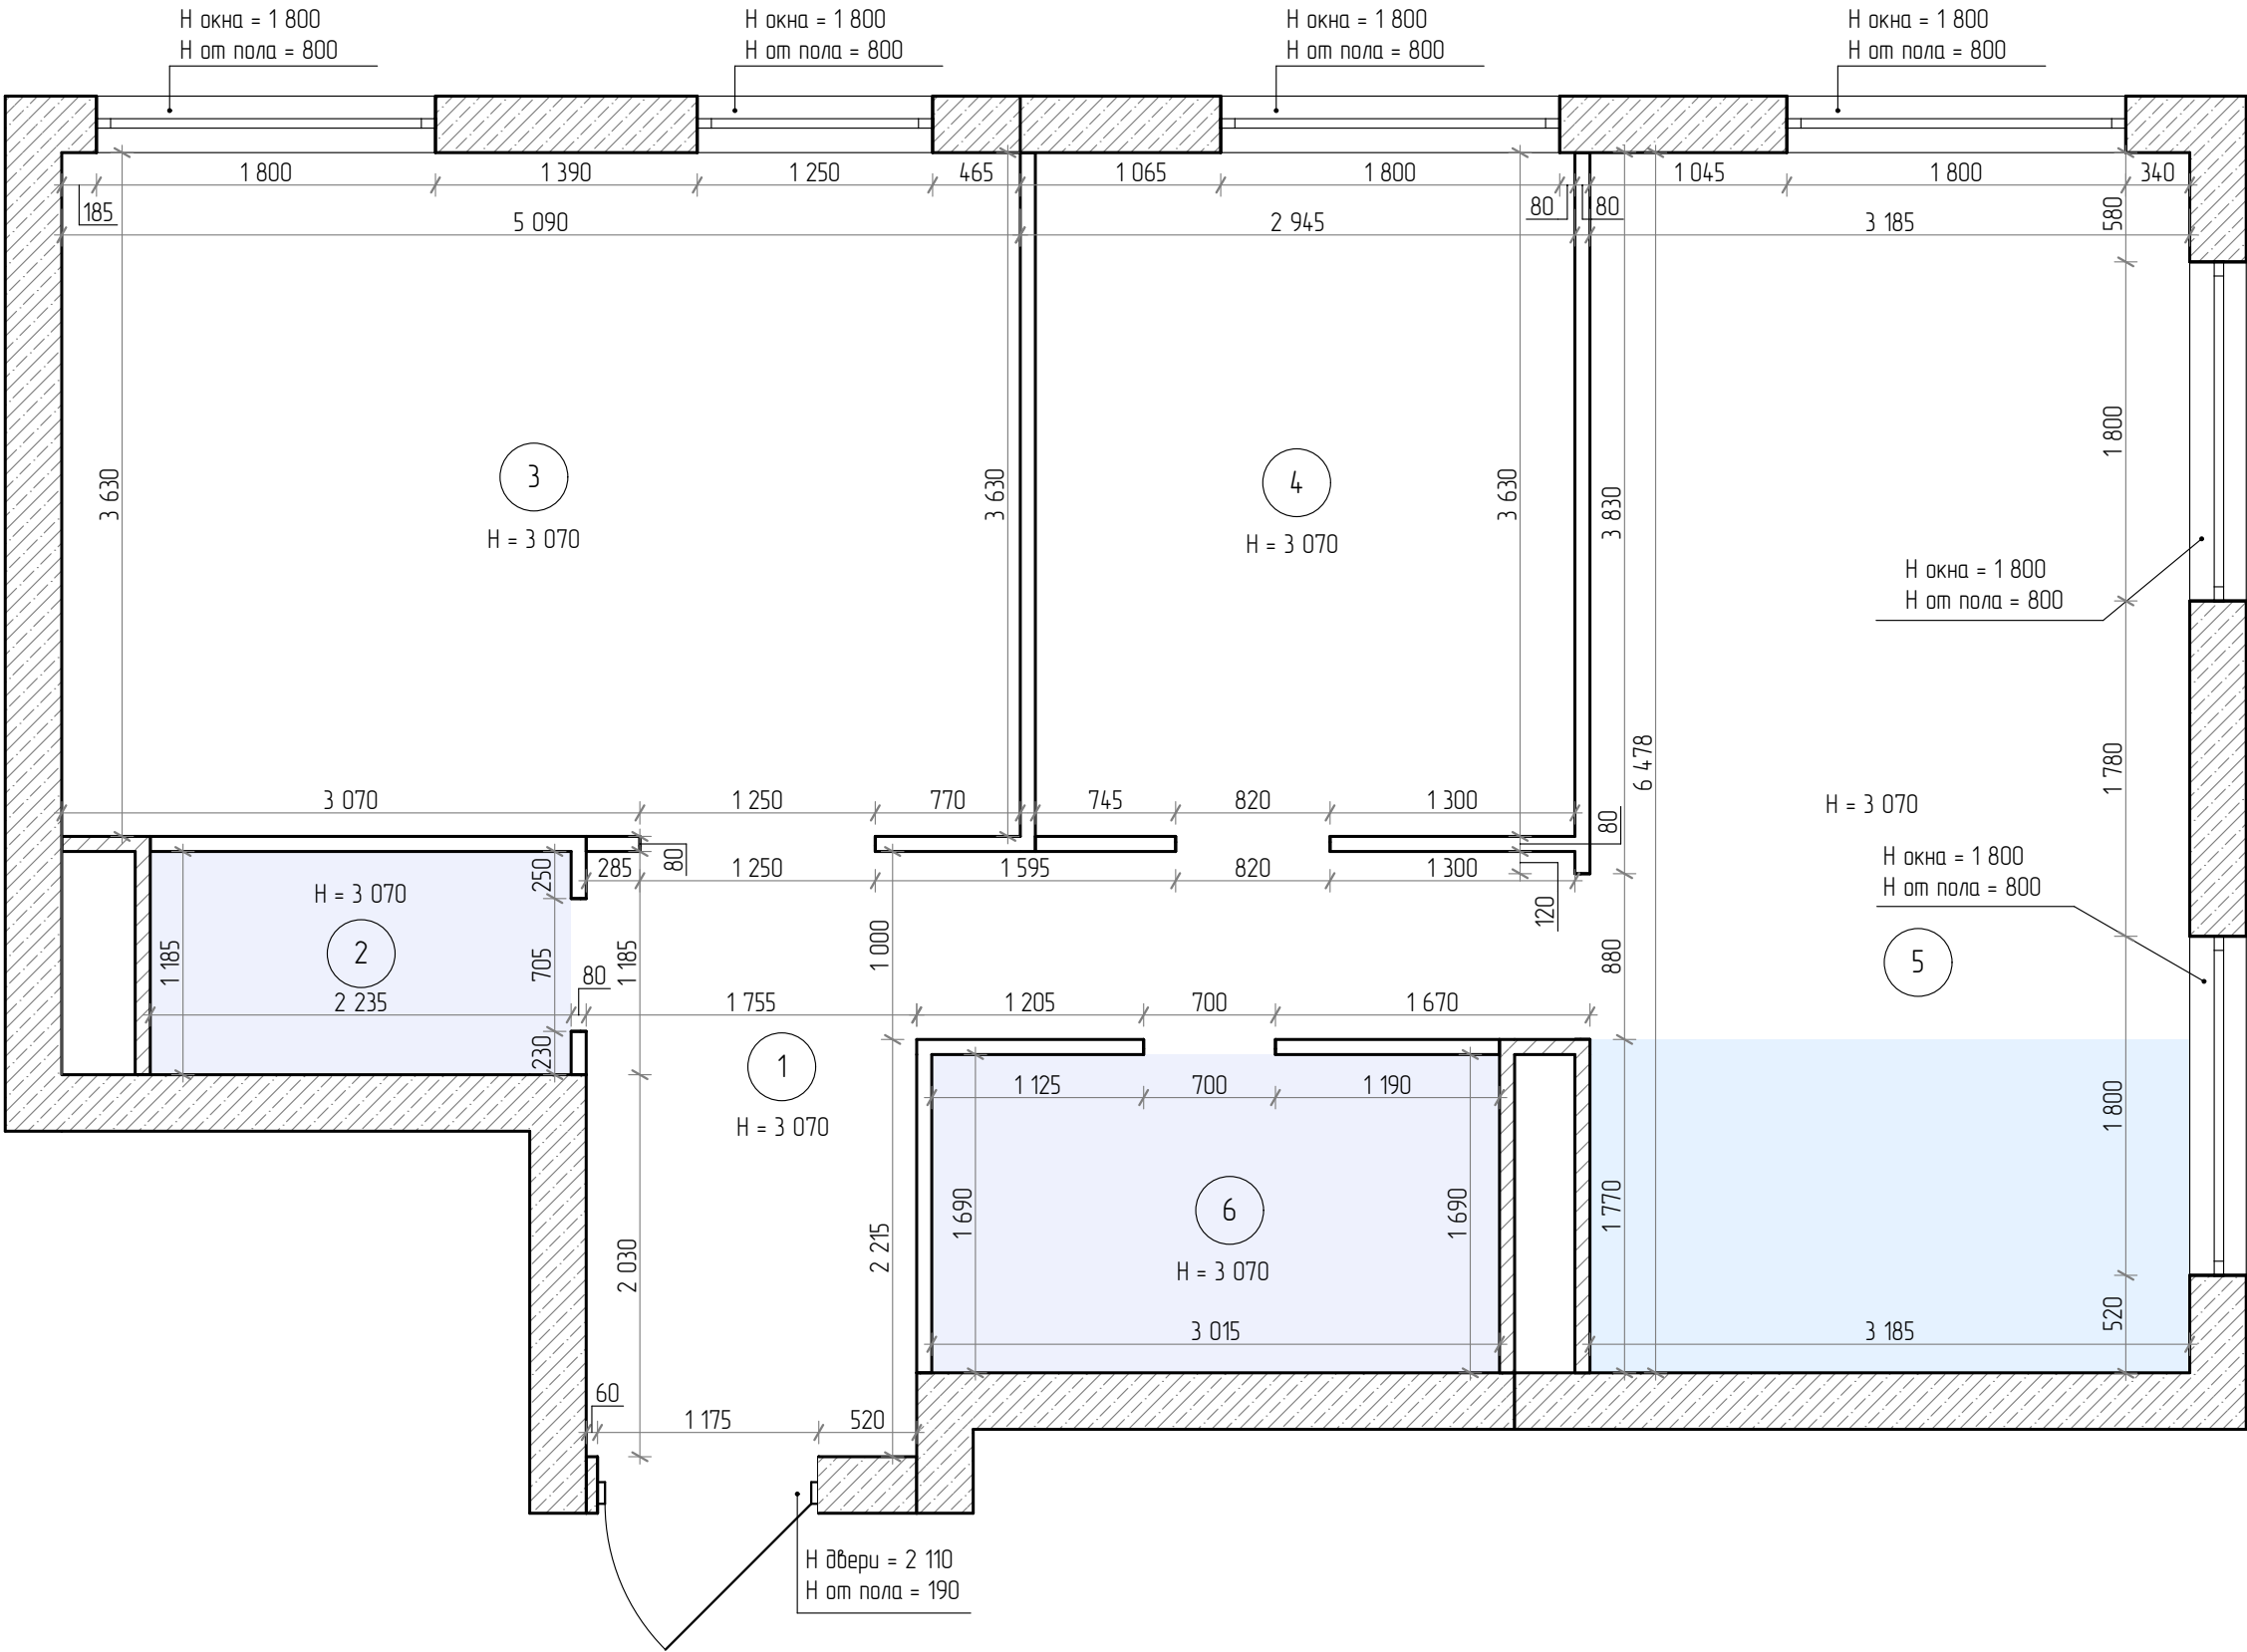

Экспликация помещений

№	Наименование	Площадь, кв.м.
1	Прихожая	9,13
2	Санузел гостевой	2,65
3	Мастер спальня	18,48
4	Спальня	10,40
5	Кухня	20,63
6	Санузел	5,09
		66,38 м²

Условные обозначения

Обозначение на плане	Наименование
	Стена - бетонный блок
	Несущая стена - бетон
	Кладка в один блок
	Жилые помещения
	Мокрая зона кухни
	Мокрая зона санузлов

Дизайн проект

Разработал	Соколов Н.Е.	Подпись	Дата	Квартира
Заказчик	Шувалова Е.Е.			Жк Кинетик

ОБМЕРНЫЙ ПЛАН


Стадия	Лист	Масштаб
ДП	04	1:40


ДЕМОНТАЖНЫЙ ПЛАН

Экспликация помещений

№	Наименование	Площадь, кв.м.
1	Прихожая	9,13
2	Санузел гостевой	2,65
3	Мастер спальня	18,48
4	Спальня	10,40
5	Кухня	20,63
6	Санузел	5,09
		66,38 м²

Условные обозначения

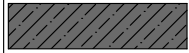Обозначение на плане	Наименование
	Стена - бетонный блок
	Несущая стена - бетон
	Демонтируемые элементы

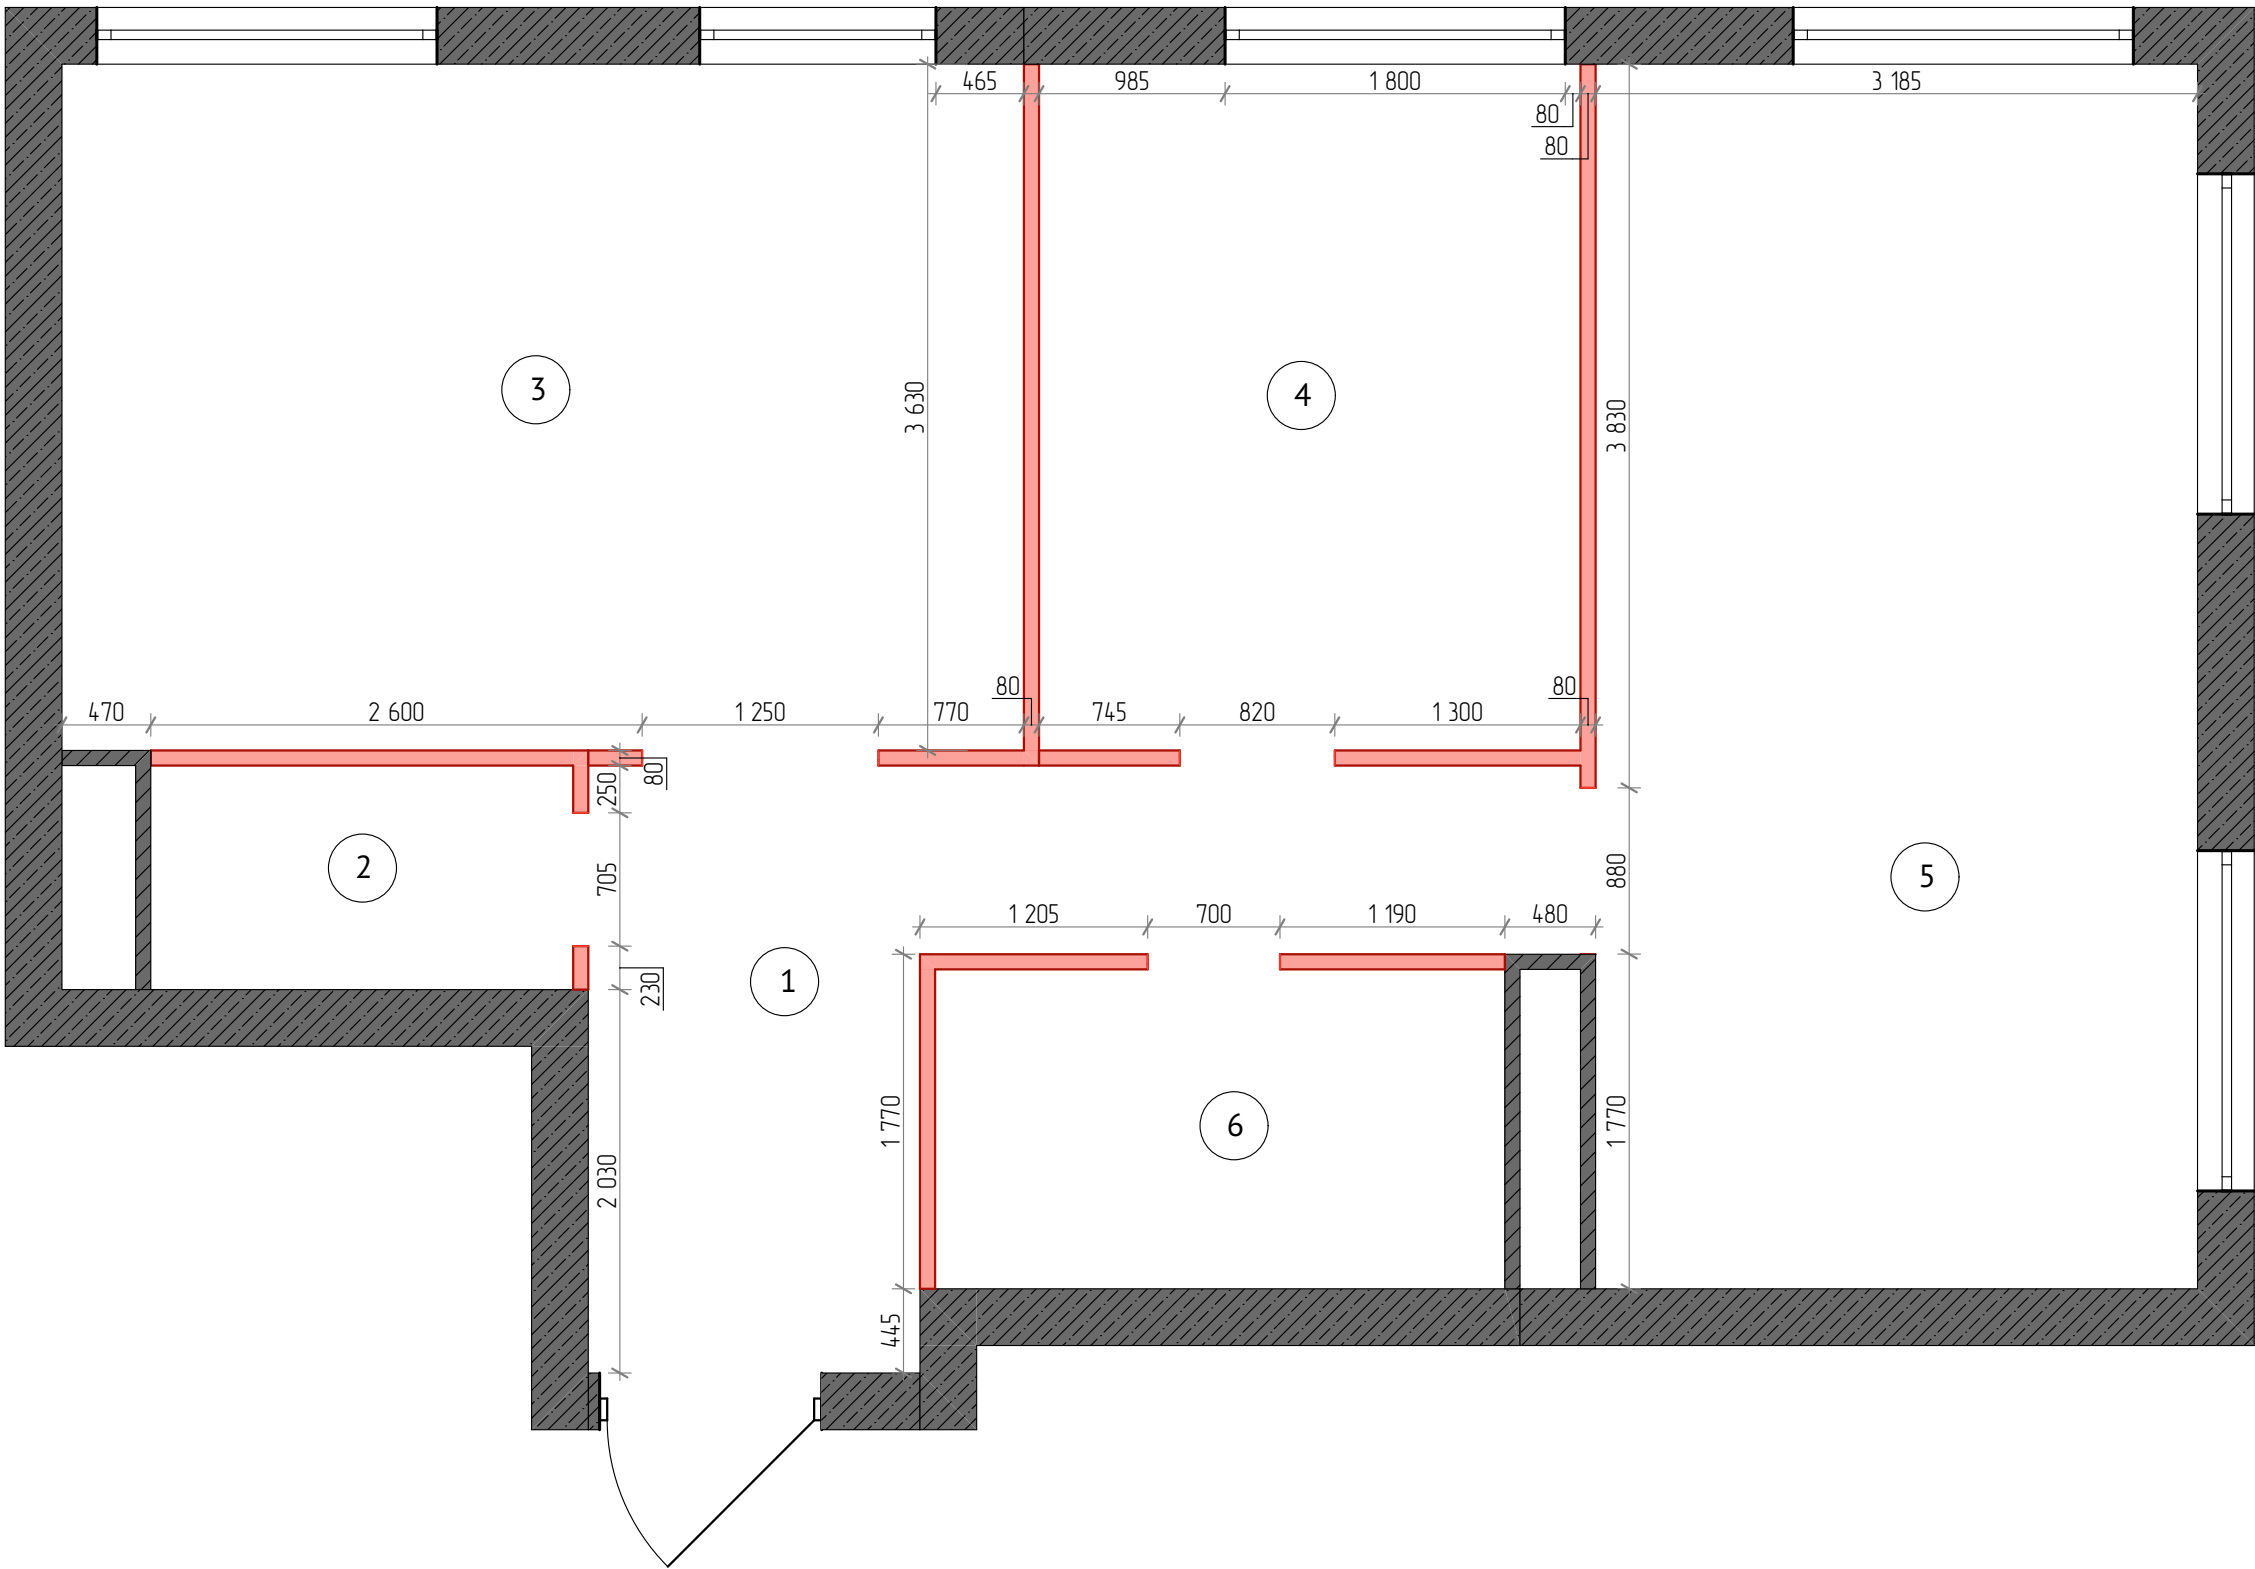

Дизайн проект

Разработал	Соколов Н.Е.	Подпись	Дата	Квартира Жк Кинетик
Заказчик	Шувалова Е.Е.			

ДЕМОНТАЖНЫЙ ПЛАН

Стадия	Лист	Масштаб
ДП	05	1:40


МОНТАЖНЫЙ ПЛАН

Экспликация помещений

№	Наименование	Площадь, кв.м.
1	Прихожая	3,77
2	Санузел	4,59
3	Кухня-Гостиная	22,73
4	Мастер спальня	8,69
5	Гардеробная	2,19
6	Мастер санузел	2,34
7	Детская 1	9,94
8	Детская 2	10,09
		64,34 м²

Условные обозначения

Обозначение на плане	Наименование
	Стена - бетонный блок
	Несущая стена - железобетон
	Штукатурка
	Керамогранит
	Возводимые перегородки из
	Возводимые перегородки бл

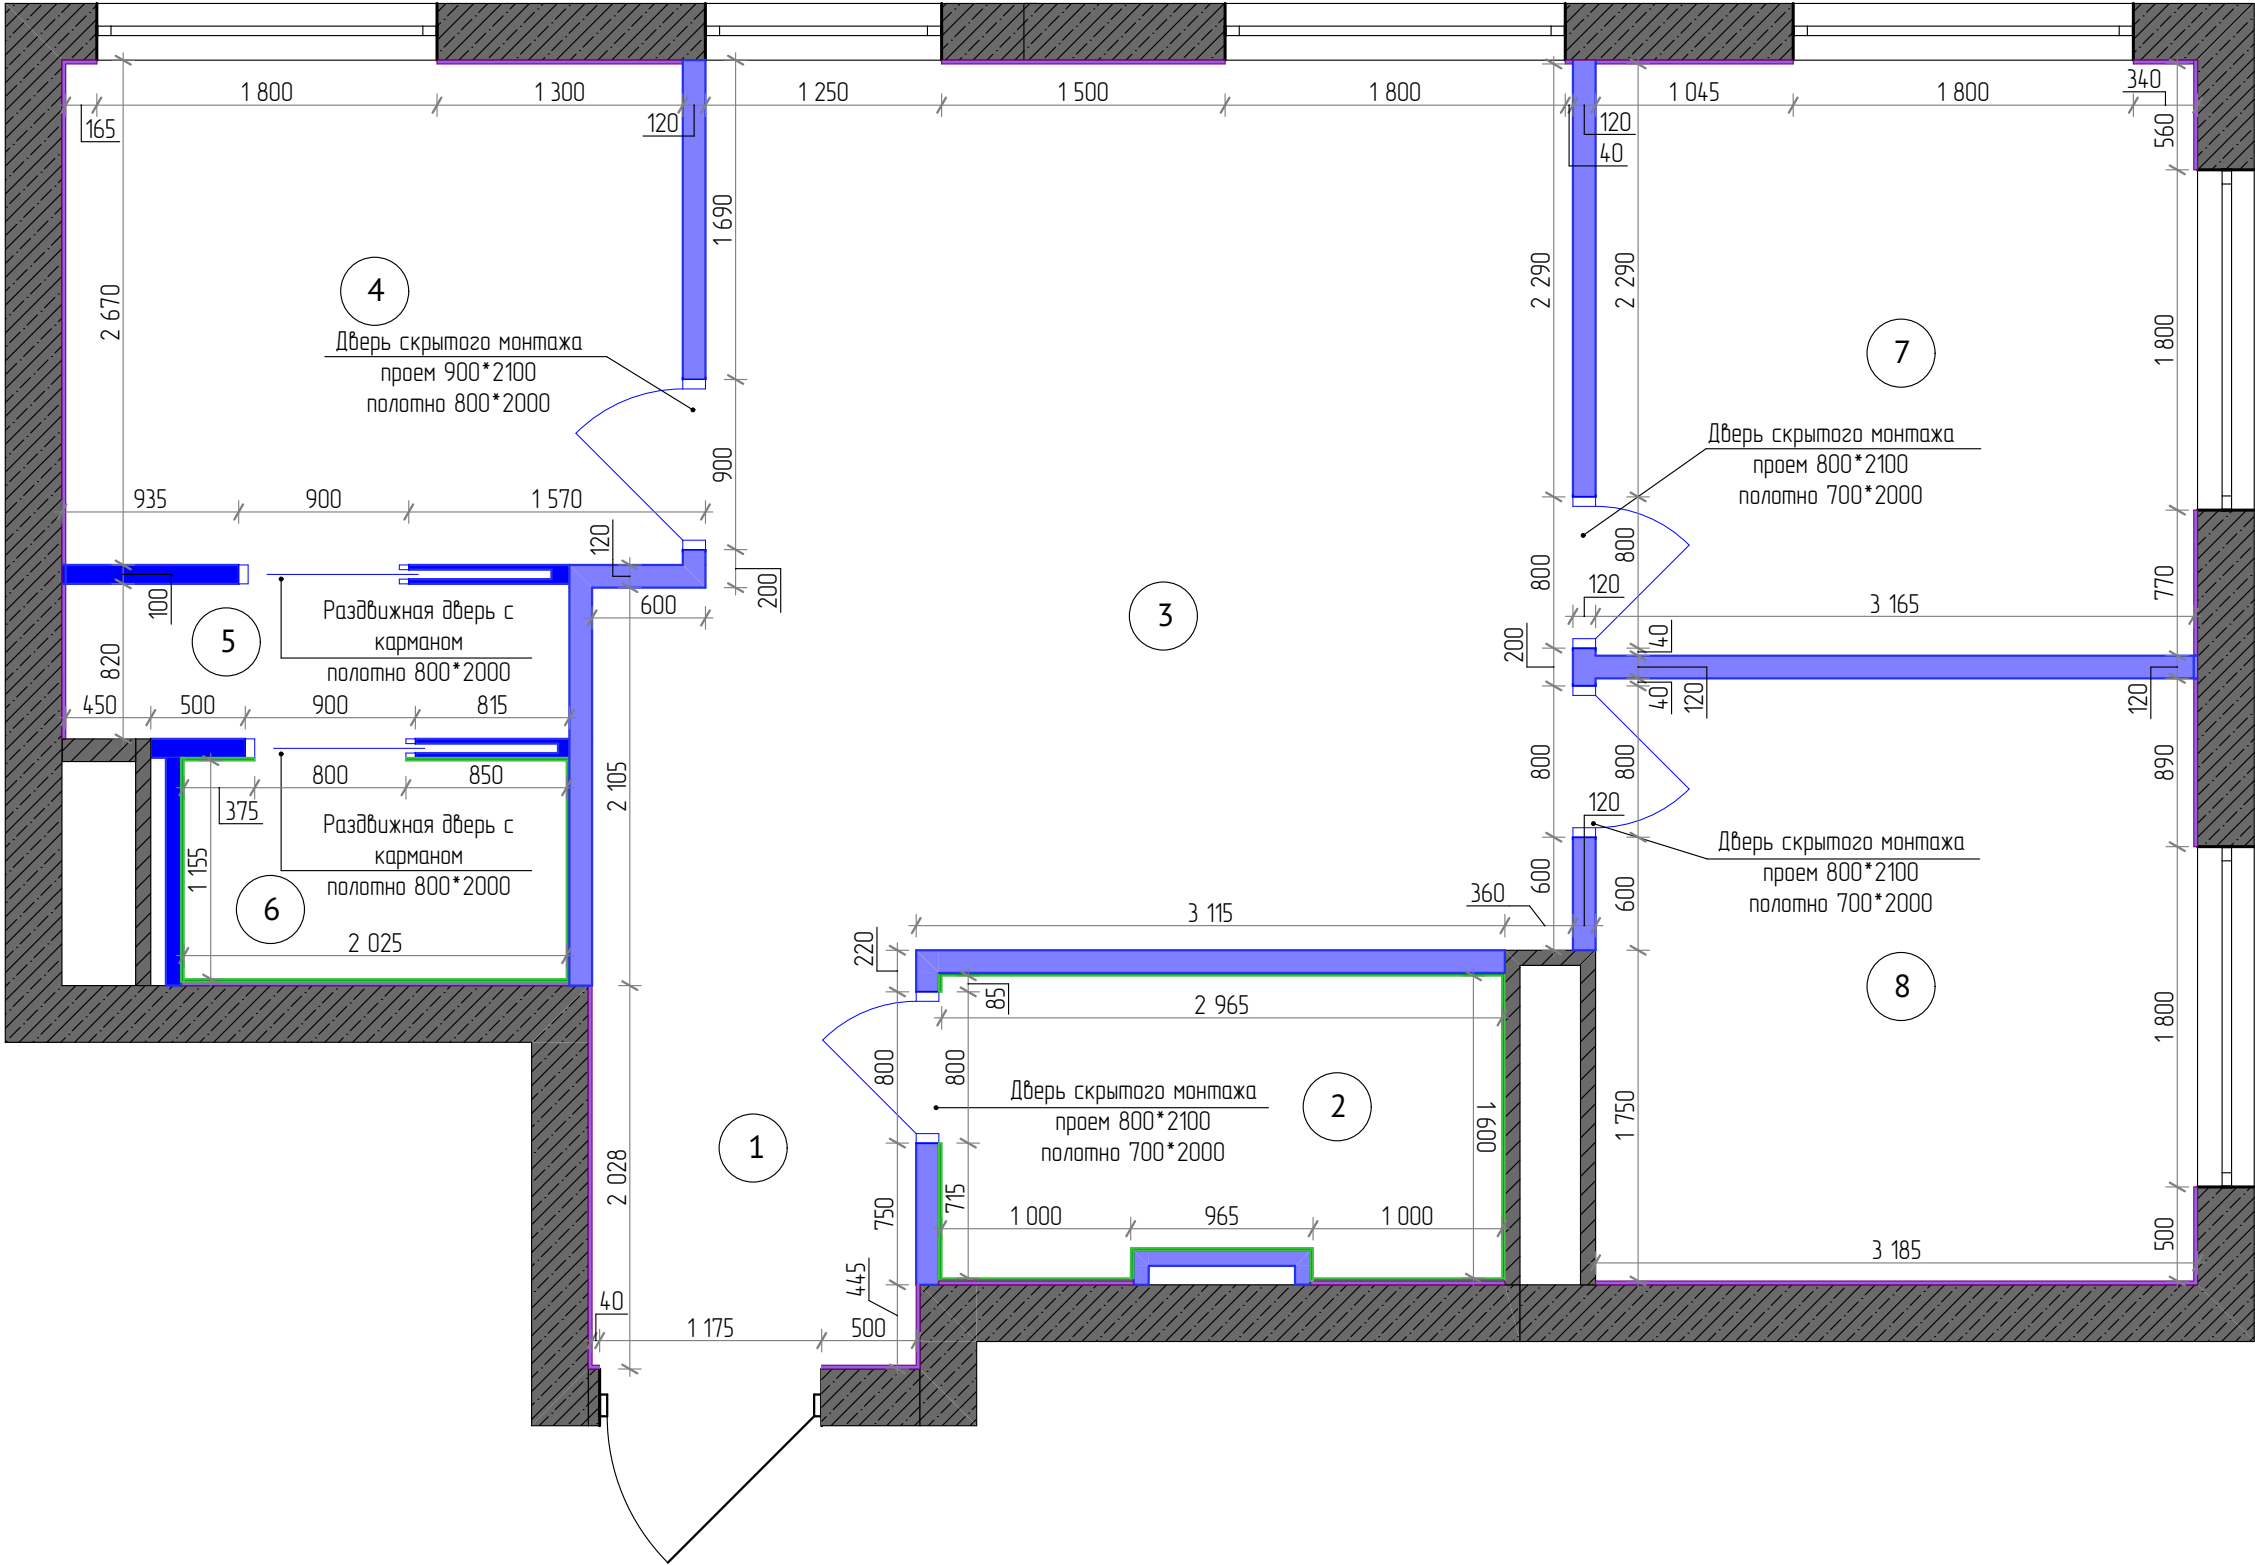

Дизайн проект


Разработал	Соколов Н.Е.	Подпись	Дата	Квартира
Заказчик	Шубалова Е.Е.			Жк Кинетик

МОНТАЖНЫЙ ПЛАН


Стадия	Лист	Масштаб
ДП	06	1:40

Экспликация помещений

№	Наименование	Площадь, кв.м.
1	Прихожая	3,77
2	Санузел	4,59
3	Кухня-Гостиная	22,73
4	Мастер спальня	8,69
5	Гардеробная	2,19
6	Мастер санузел	2,34
7	Детская 1	9,94
8	Детская 2	10,09
		64,34 м²

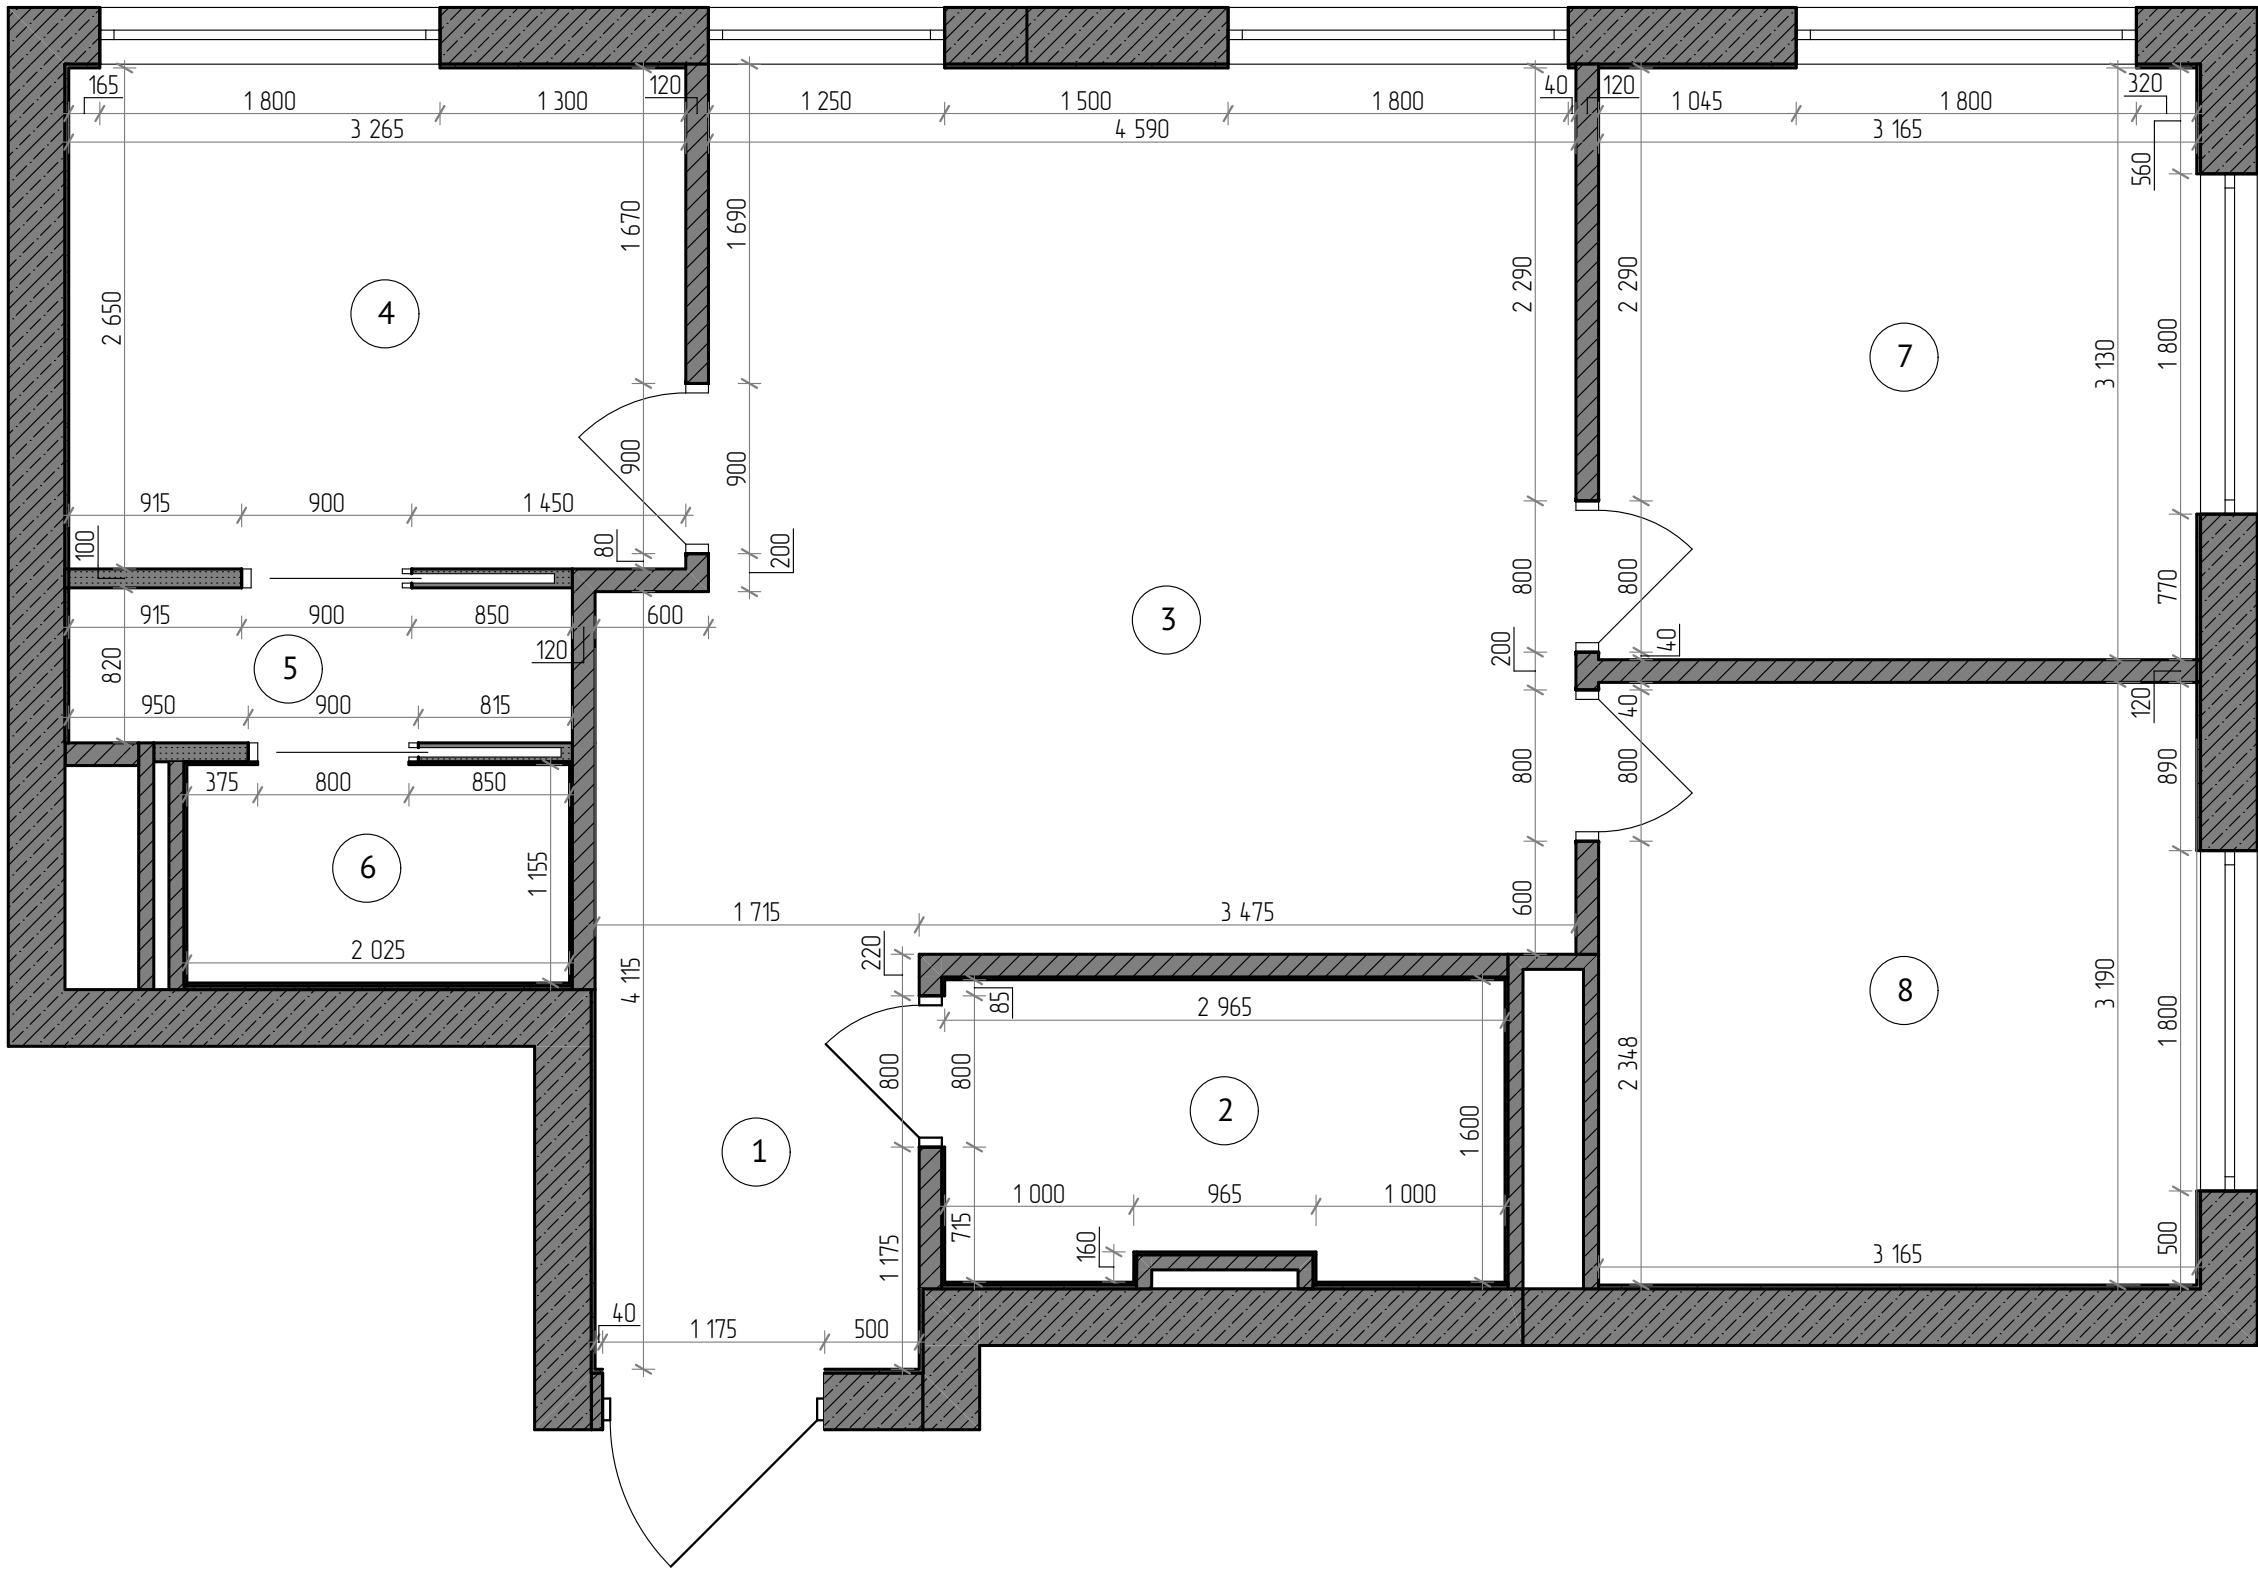

ПЛАН РАССТАНОВКИ МЕБЕЛИ И ОБОРУДОВАНИЯ

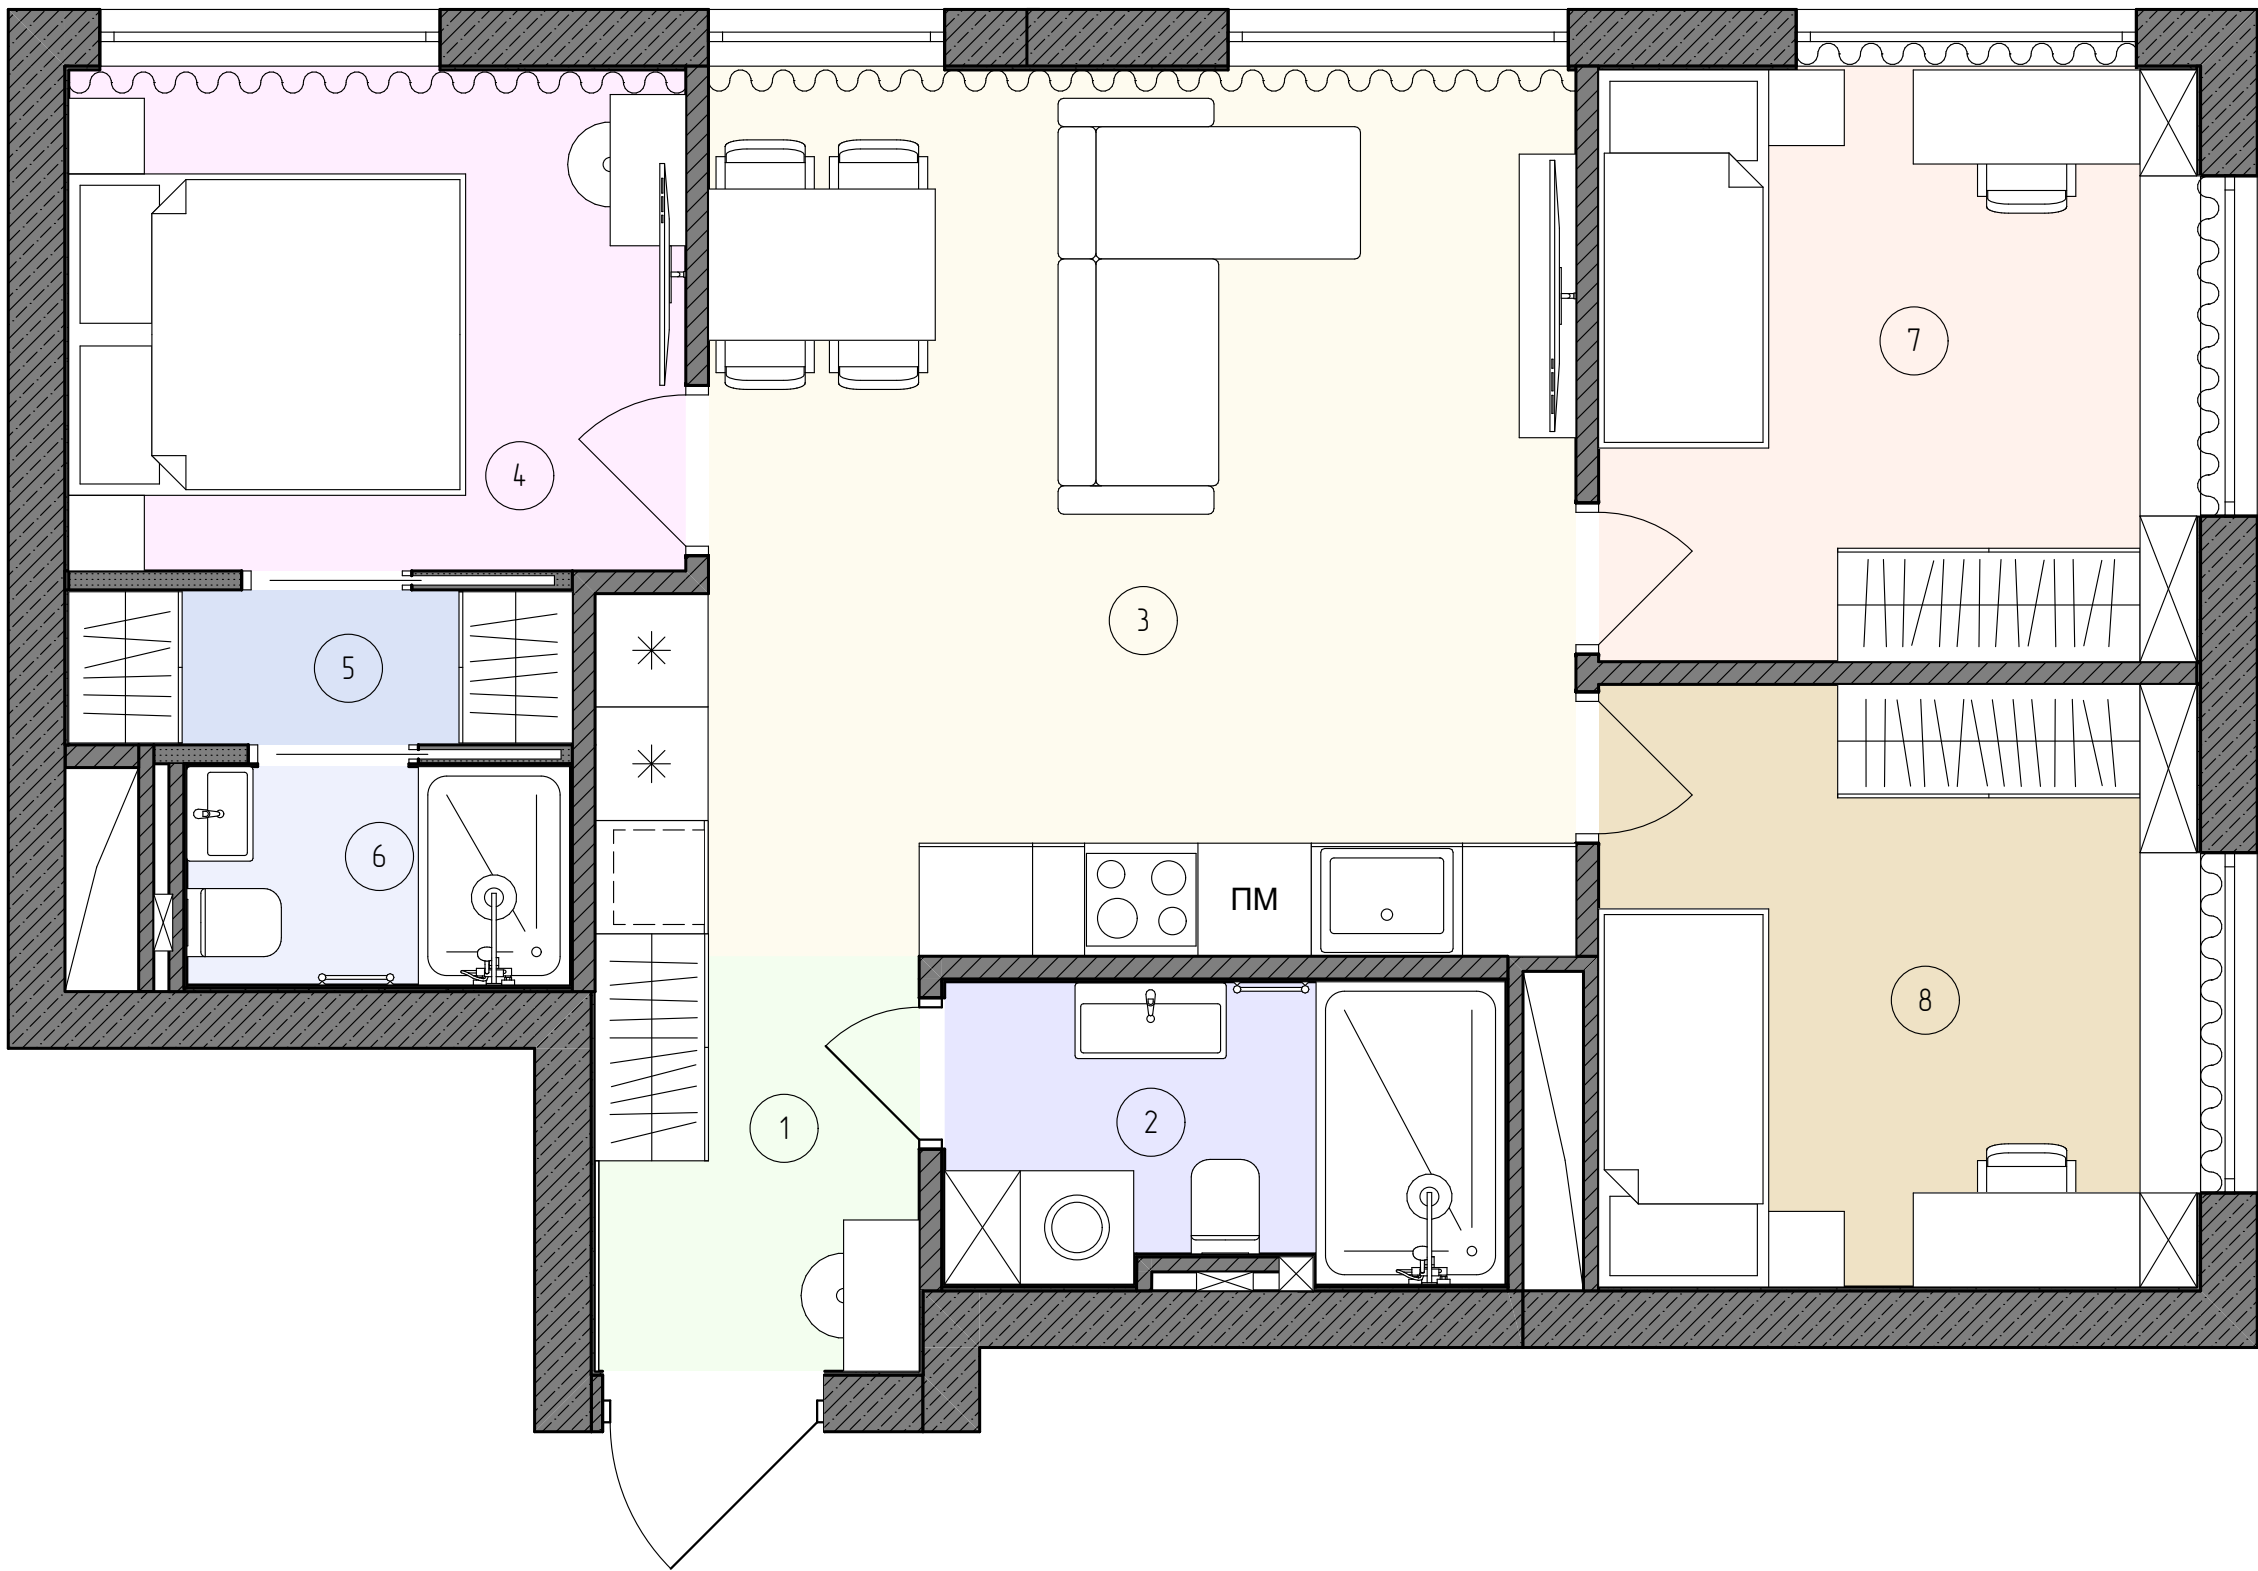

Экспликация помещений

№	Наименование	Площадь, кв.м.
1	Прихожая	3,77
2	Санузел	4,59
3	Кухня-Гостиная	22,73
4	Мастер спальня	8,69
5	Гардеробная	2,19
6	Мастер санузел	2,34
7	Детская 1	9,94
8	Детская 2	10,09
		64,34 м²


Дизайн проект

Разработал	Соколов Н.Е.	Подпись	Дата	Квартира
Заказчик	Шувалова Е.Е.			Жк Кинетик

ПЛАН РАССТАНОВКИ МЕБЕЛИ И ОБОРУДОВАНИЯ

Стадия	Лист	Масштаб
ДП	08	1:40

ПЛАН РАССТАНОВКИ МЕБЕЛИ И ОБОРУДОВАНИЯ (РАЗМЕРЫ)

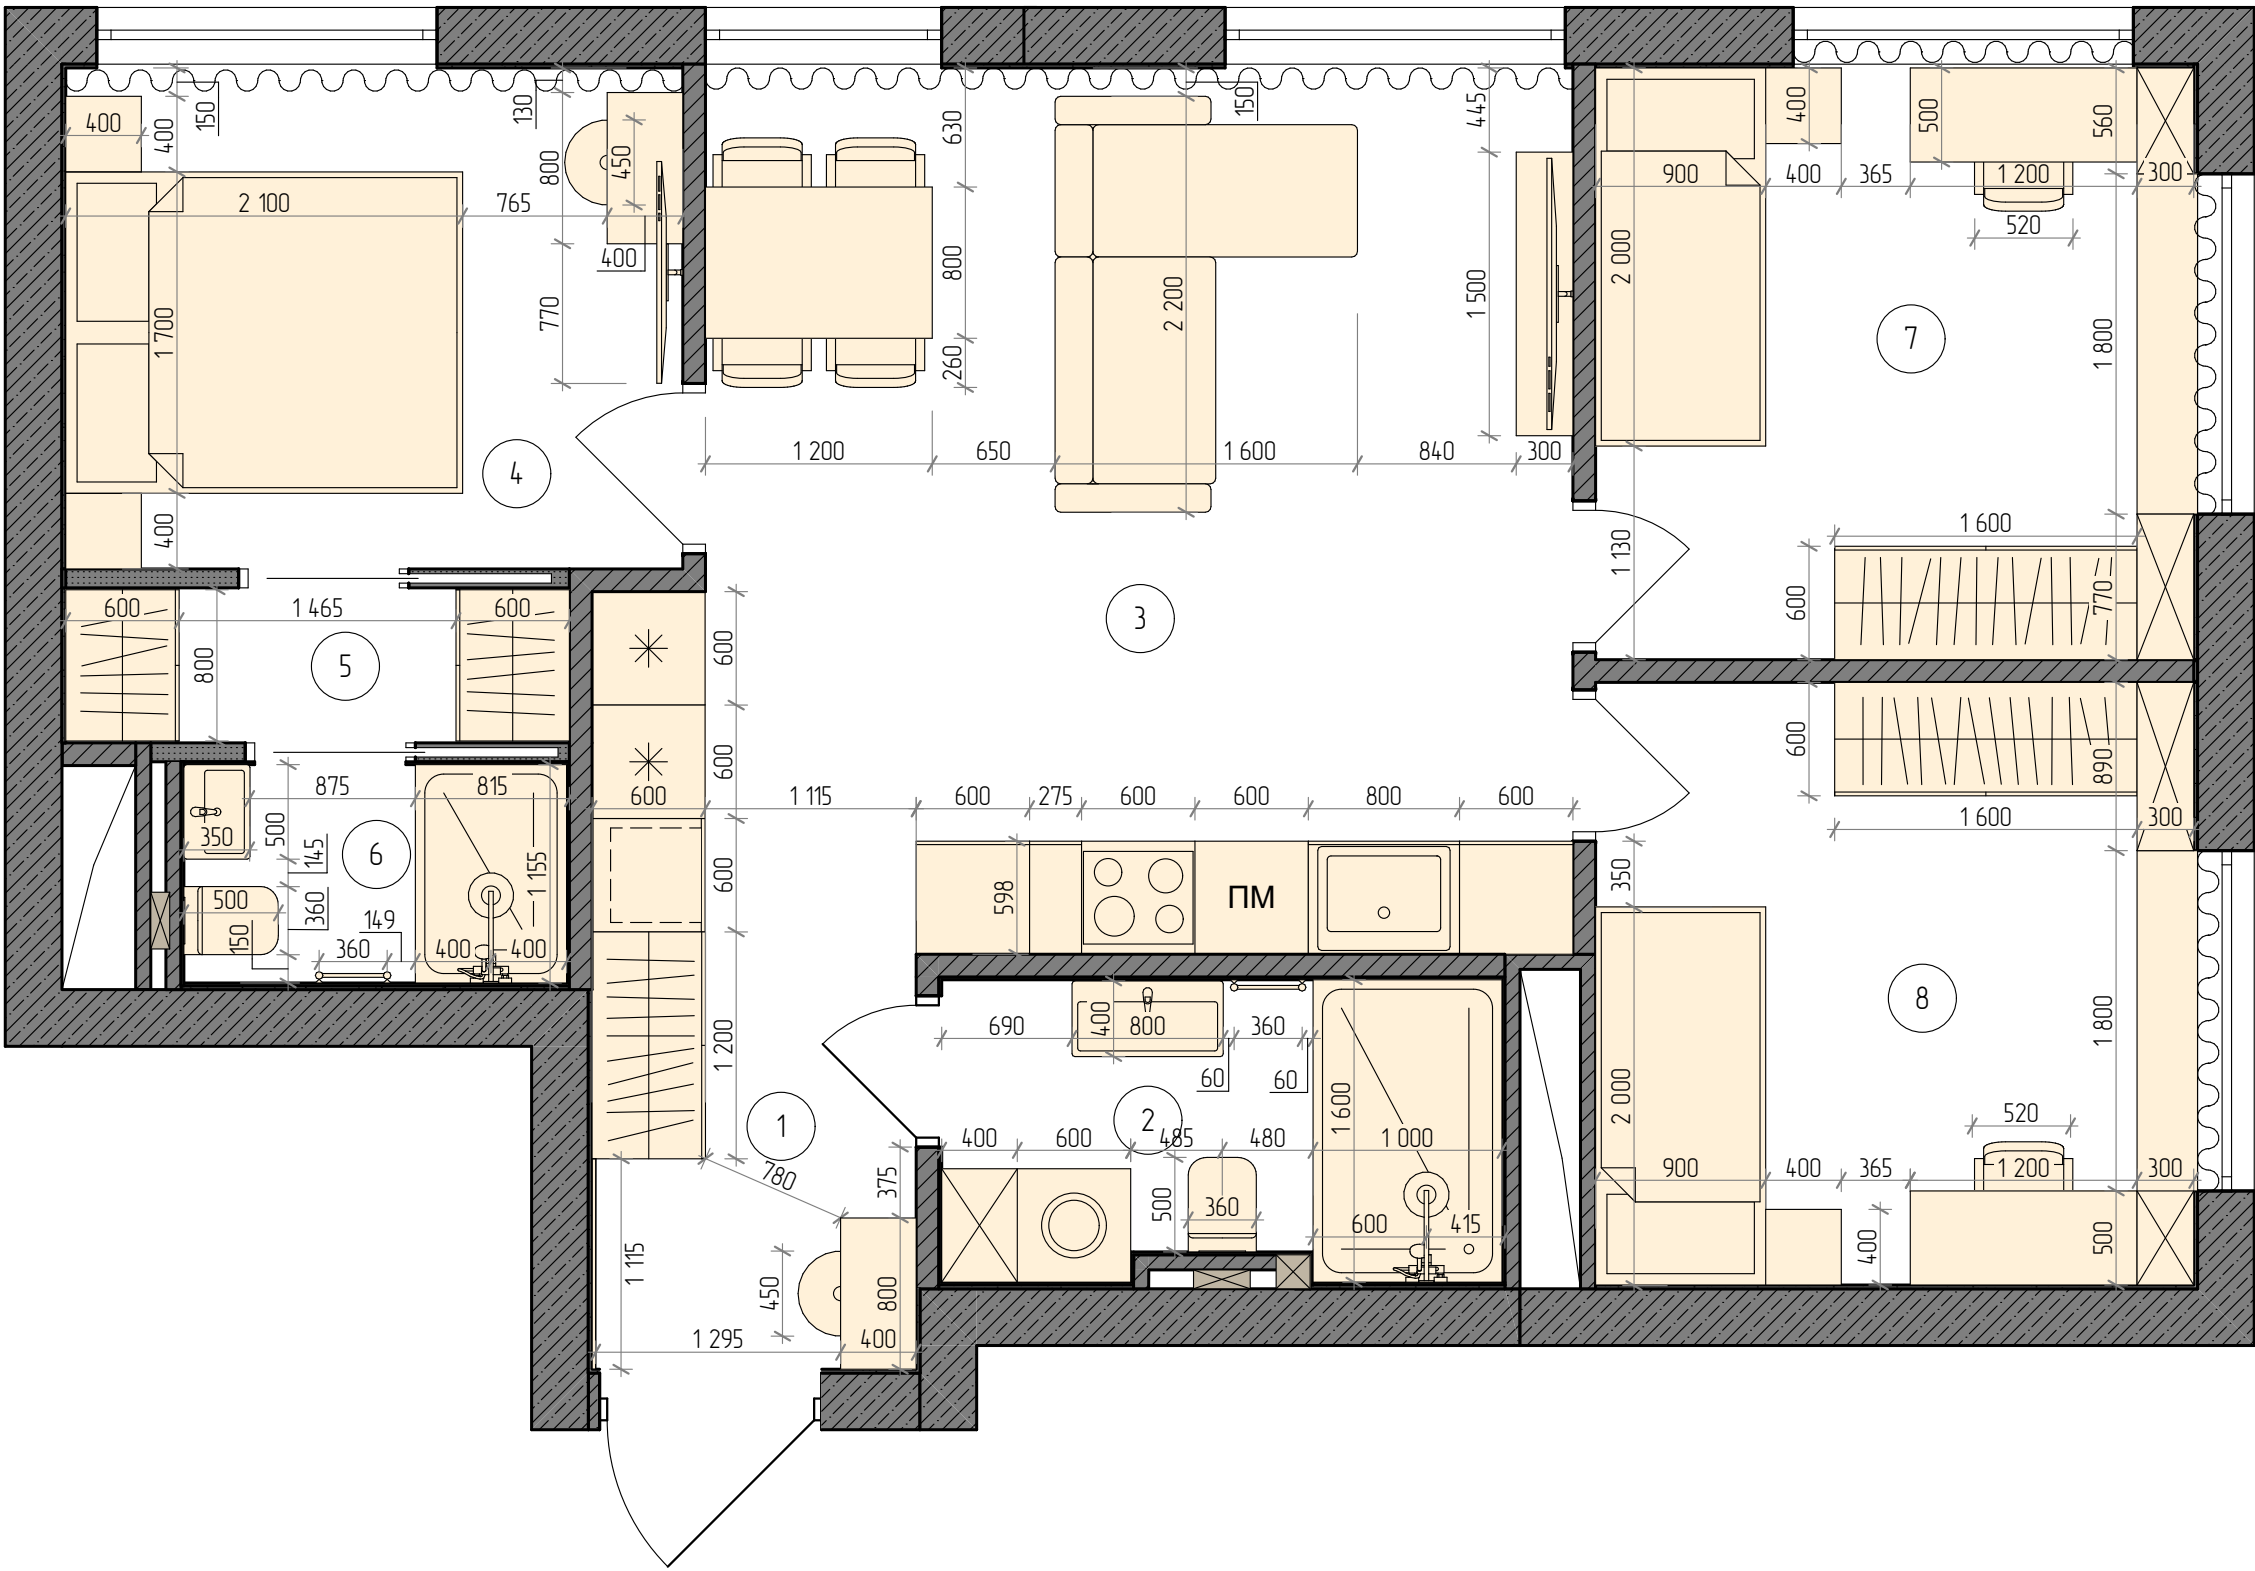

Экспликация помещений


№	Наименование	Площадь, кв.м.
1	Прихожая	3,77
2	Санузел	4,59
3	Кухня-Гостиная	22,73
4	Мастер спальня	8,69
5	Гардеробная	2,19
6	Мастер санузел	2,34
7	Детская 1	9,94
8	Детская 2	10,09
		64,34 м²

Дизайн проект

Разработал	Соколов Н.Е.	Подпись	Дата	Квартира
Заказчик	Шуфалова Е.Е.			Жк Кинетик

ПЛАН РАССТАНОВКИ МЕБЕЛИ И ОБОРУДОВАНИЯ (РАЗМЕРЫ)

Стадия	Лист	Масштаб
ДП	09	1:40

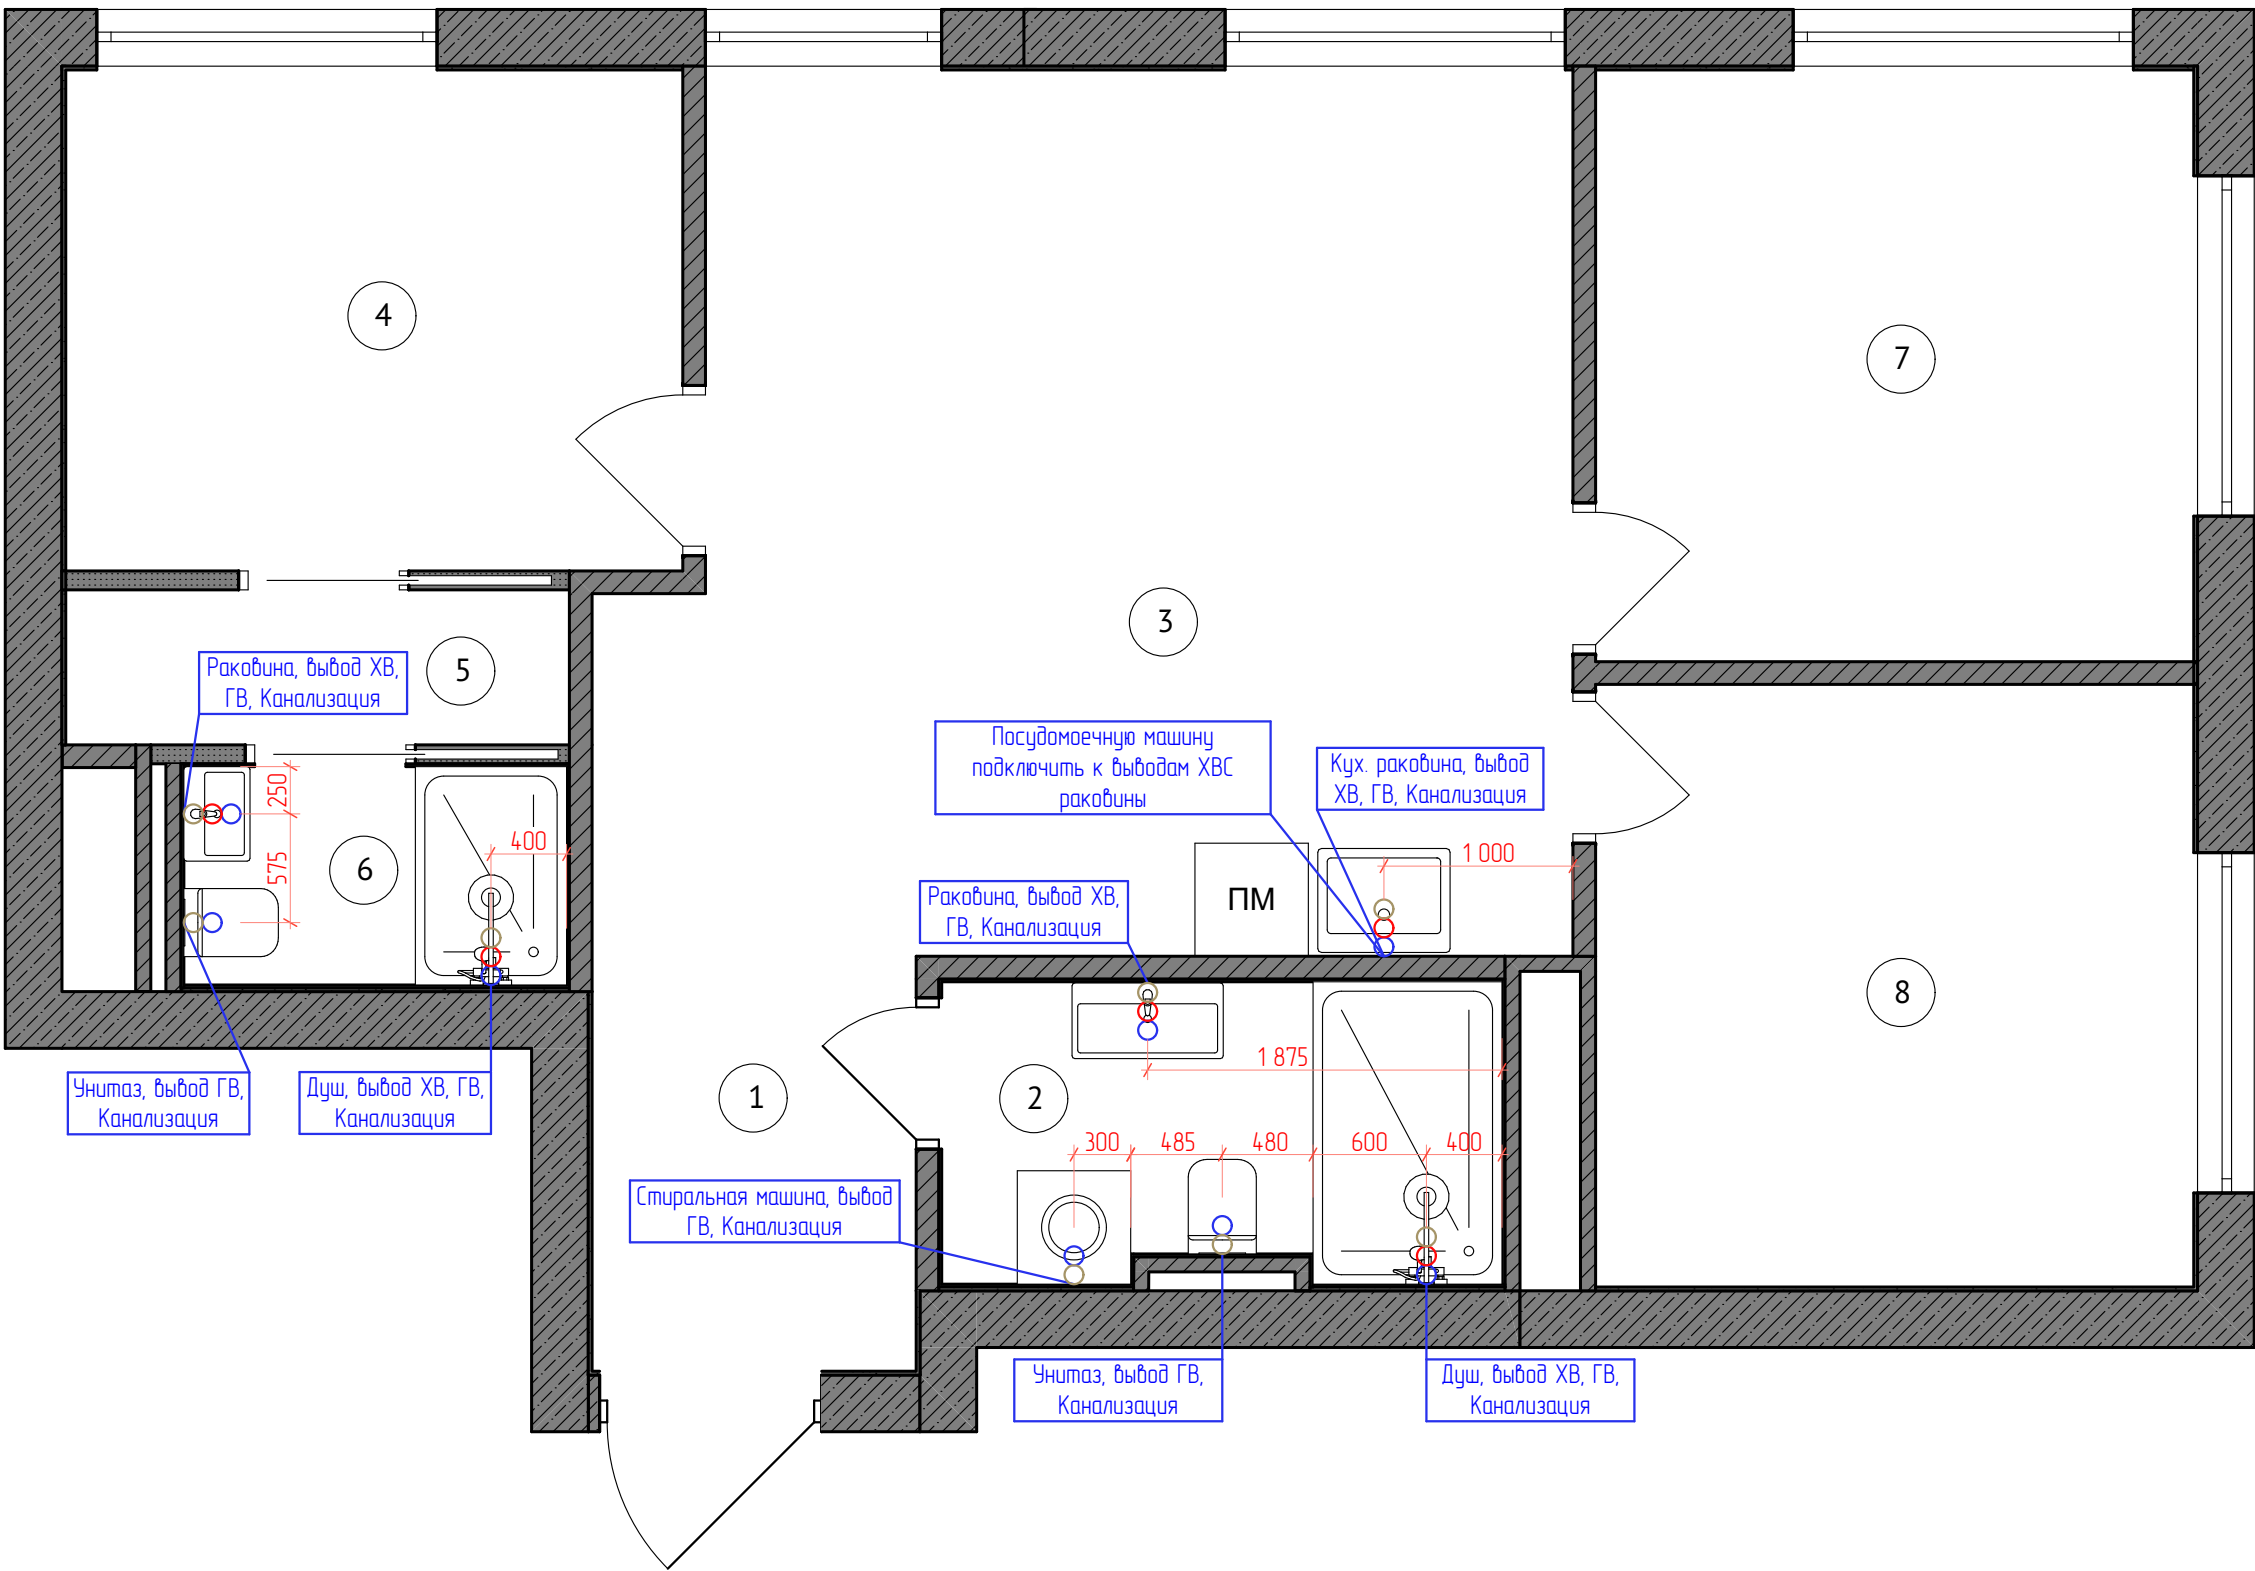

Экспликация помещений

№	Наименование	Площадь, кв.м.
1	Прихожая	3,77
2	Санузел	4,59
3	Кухня-Гостиная	22,73
4	Мастер спальня	8,69
5	Гардеробная	2,19
6	Мастер санузел	2,34
7	Детская 1	9,94
8	Детская 2	10,09
		64,34 м²

ВНИМАНИЕ!

1. При любом несоответствии привязок в натуре (вследствии погрешности в обмерах и строительных работах), по всем вопросам необходимо обратиться к авторам проекта для внесения соответствующих корректировок на месте.

Дизайн проект

Разработал	Соколов Н.Е.
Заказчик	Шуфалова Е.Е.


Подпись

Дата

Квартира
Жк Кинетик

СХЕМА УКАЗАНИЯ ПОДКЛЮЧЕНИЯ САНТЕХНИКИ

Стадия	Лист	Масштаб
ДП	10	1:40

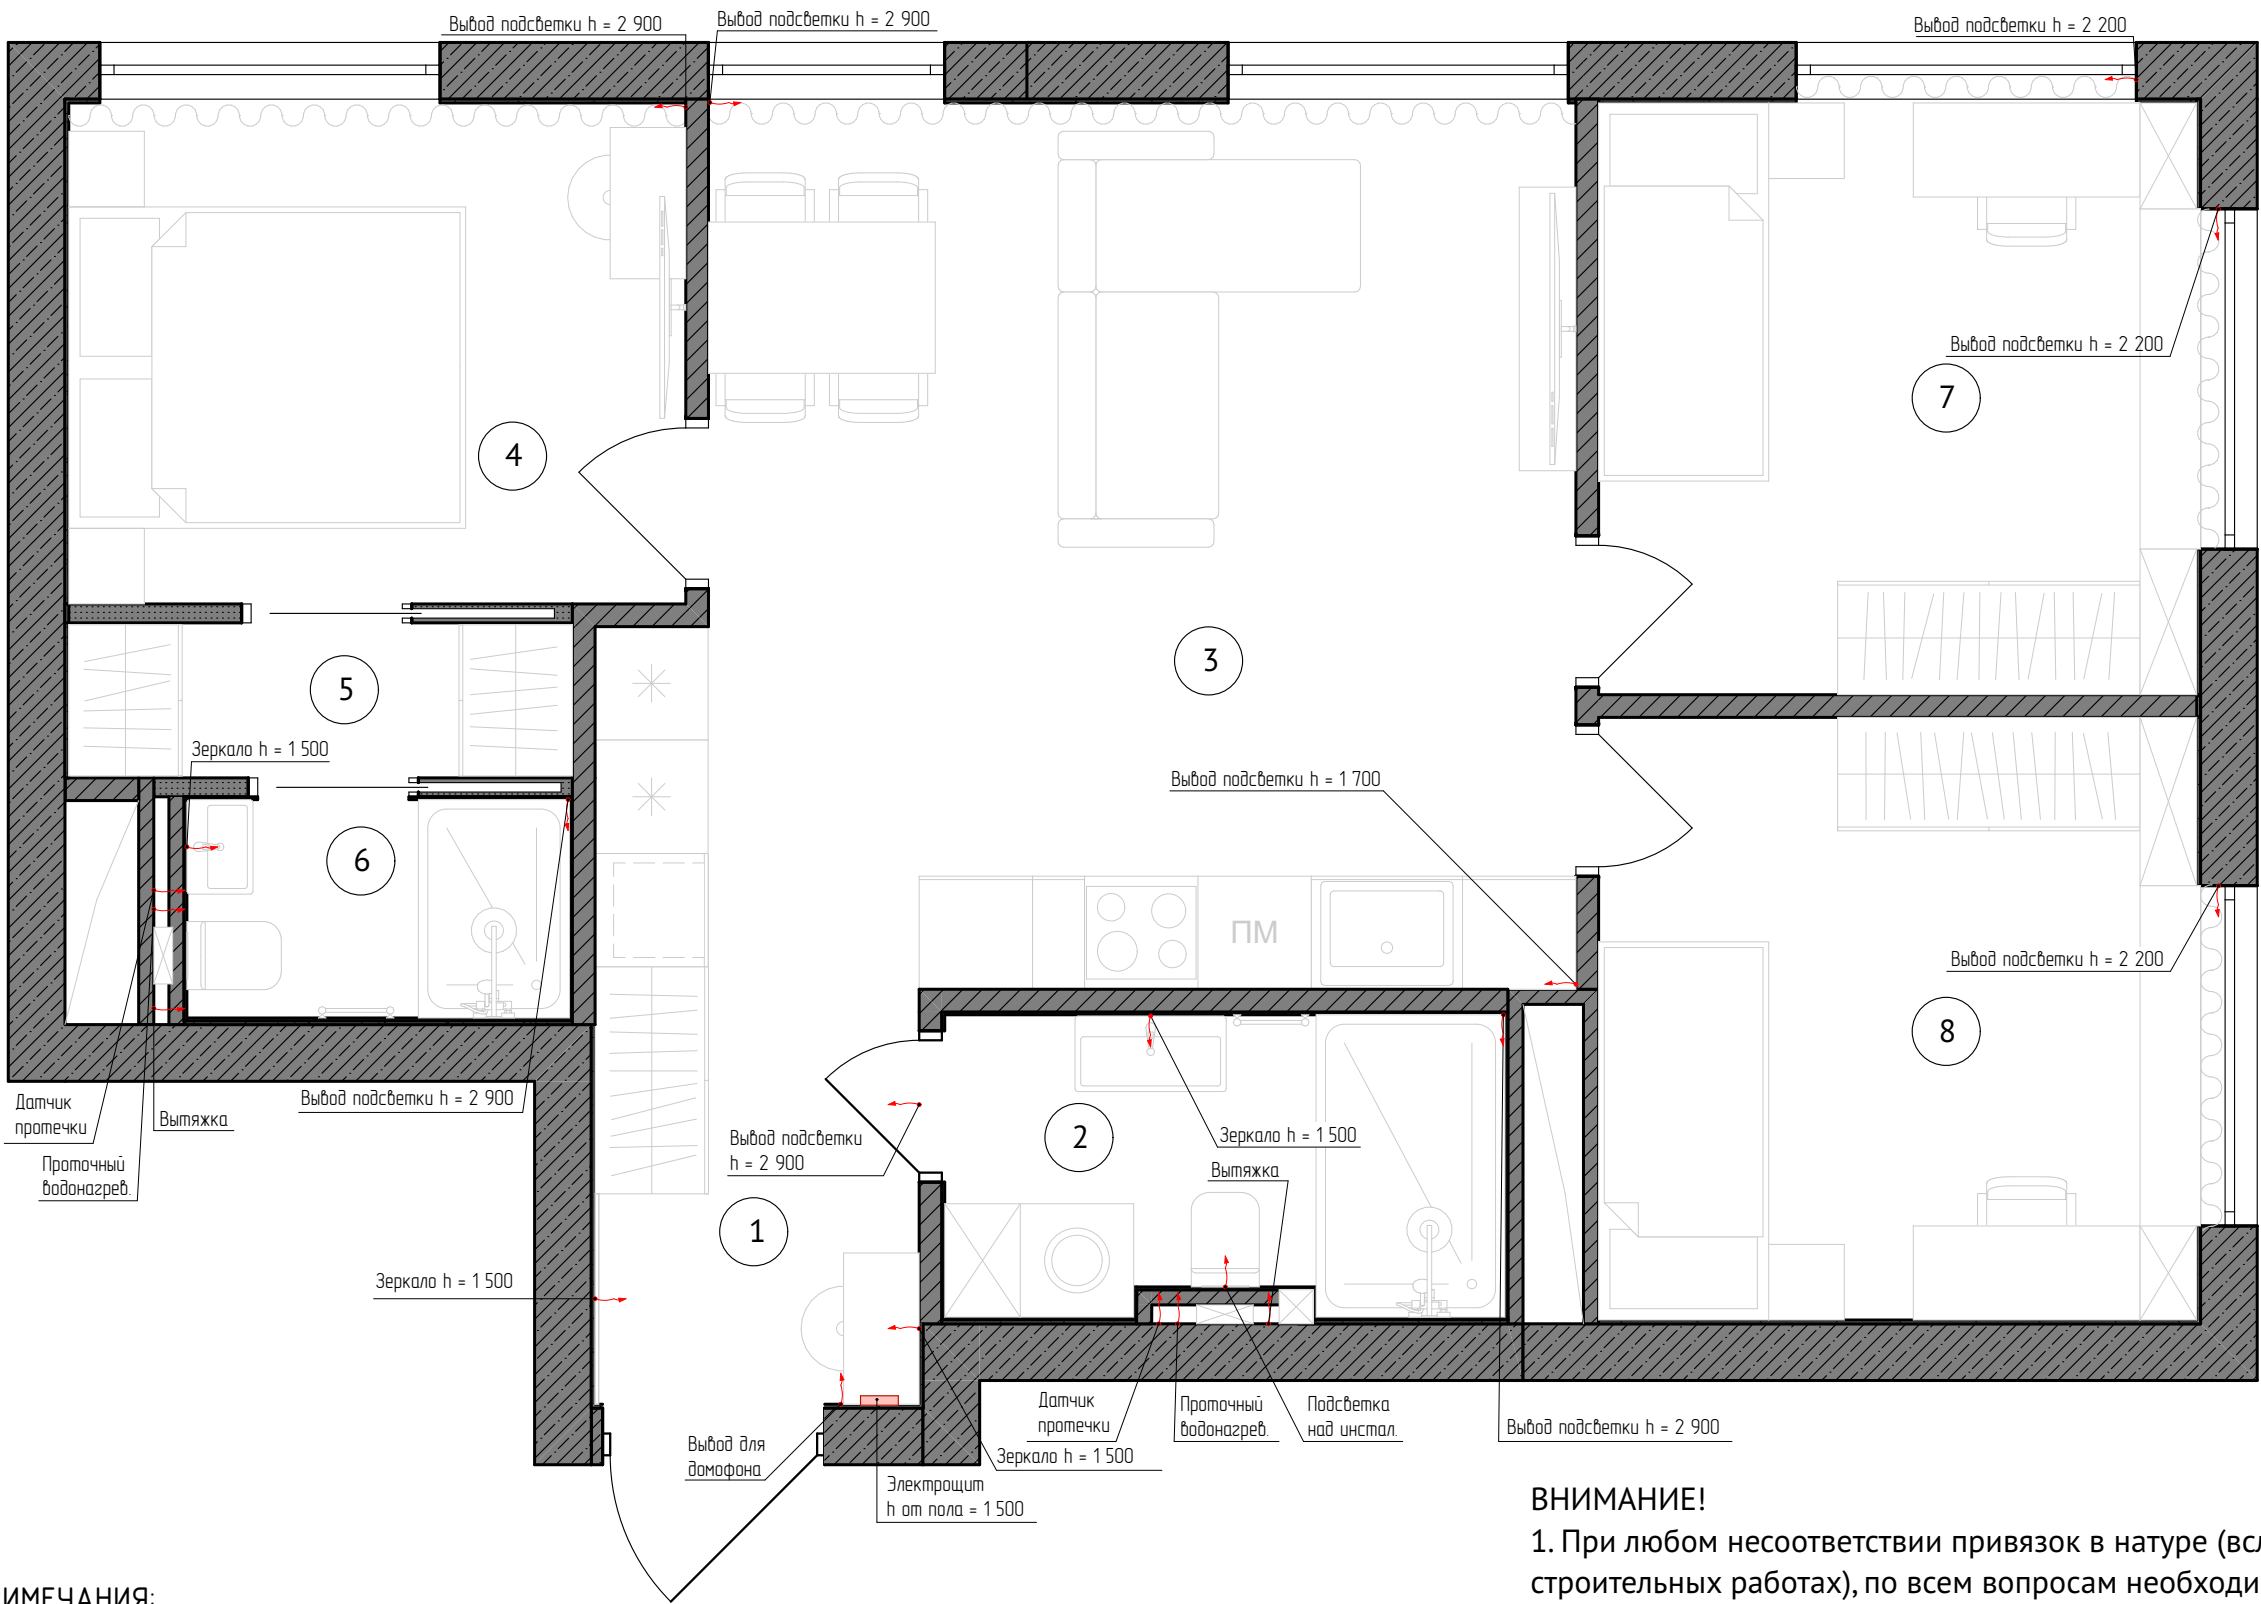

Экспликация помещений

№	Наименование	Площадь, кв.м.
1	Прихожая	3,77
2	Санузел	4,59
3	Кухня-Гостиная	22,73
4	Мастер спальня	8,69
5	Гардеробная	2,19
6	Мастер санузел	2,34
7	Детская 1	9,94
8	Детская 2	10,09
		64,34 м²

ПРИМЕЧАНИЯ:

- Данный лист рассматривать совместно с разделом ЭО.
- Розетки и электровыводы для кухонного оборудования, их количество и привязки согласовать по тех.картам поставщиков при заказе мебели.
- Пожарная и охранная сигнализация выполняются по отдельным проектам. Предусмотреть питание и сигнальные кабели для датчиков.
- Спутниковое ТВ, электропитание специальных устройств, бытовой техники, аудиосистем, электроники предусмотреть в соответствии с их особенностями.
- Все размеры, указанные на чертежах, условны и требуют уточнения после проведения монтажных работ.


ВНИМАНИЕ!

1. При любом несоответствии привязок в натуре (вследствии погрешности в обмерах и строительных работах), по всем вопросам необходимо обратиться к авторам проекта для внесения соответствующих корректировок на месте.
- Любые отклонения от плана БТИ подлежат согласованию в муниципальных органах.
- Ответственность за данное нарушение заказчик принимает на себя.

ПЛАН РОЗЕТОК И ВЫКЛЮЧАТЕЛЕЙ (РАЗМЕРЫ)

Экспликация помещений

№	Наименование	Площадь, кв.м.
1	Прихожая	3,77
2	Санузел	4,59
3	Кухня-Гостиная	22,73
4	Мастер спальня	8,69
5	Гардеробная	2,19
6	Мастер санузел	2,34
7	Детская 1	9,94
8	Детская 2	10,09
		64,34 м²

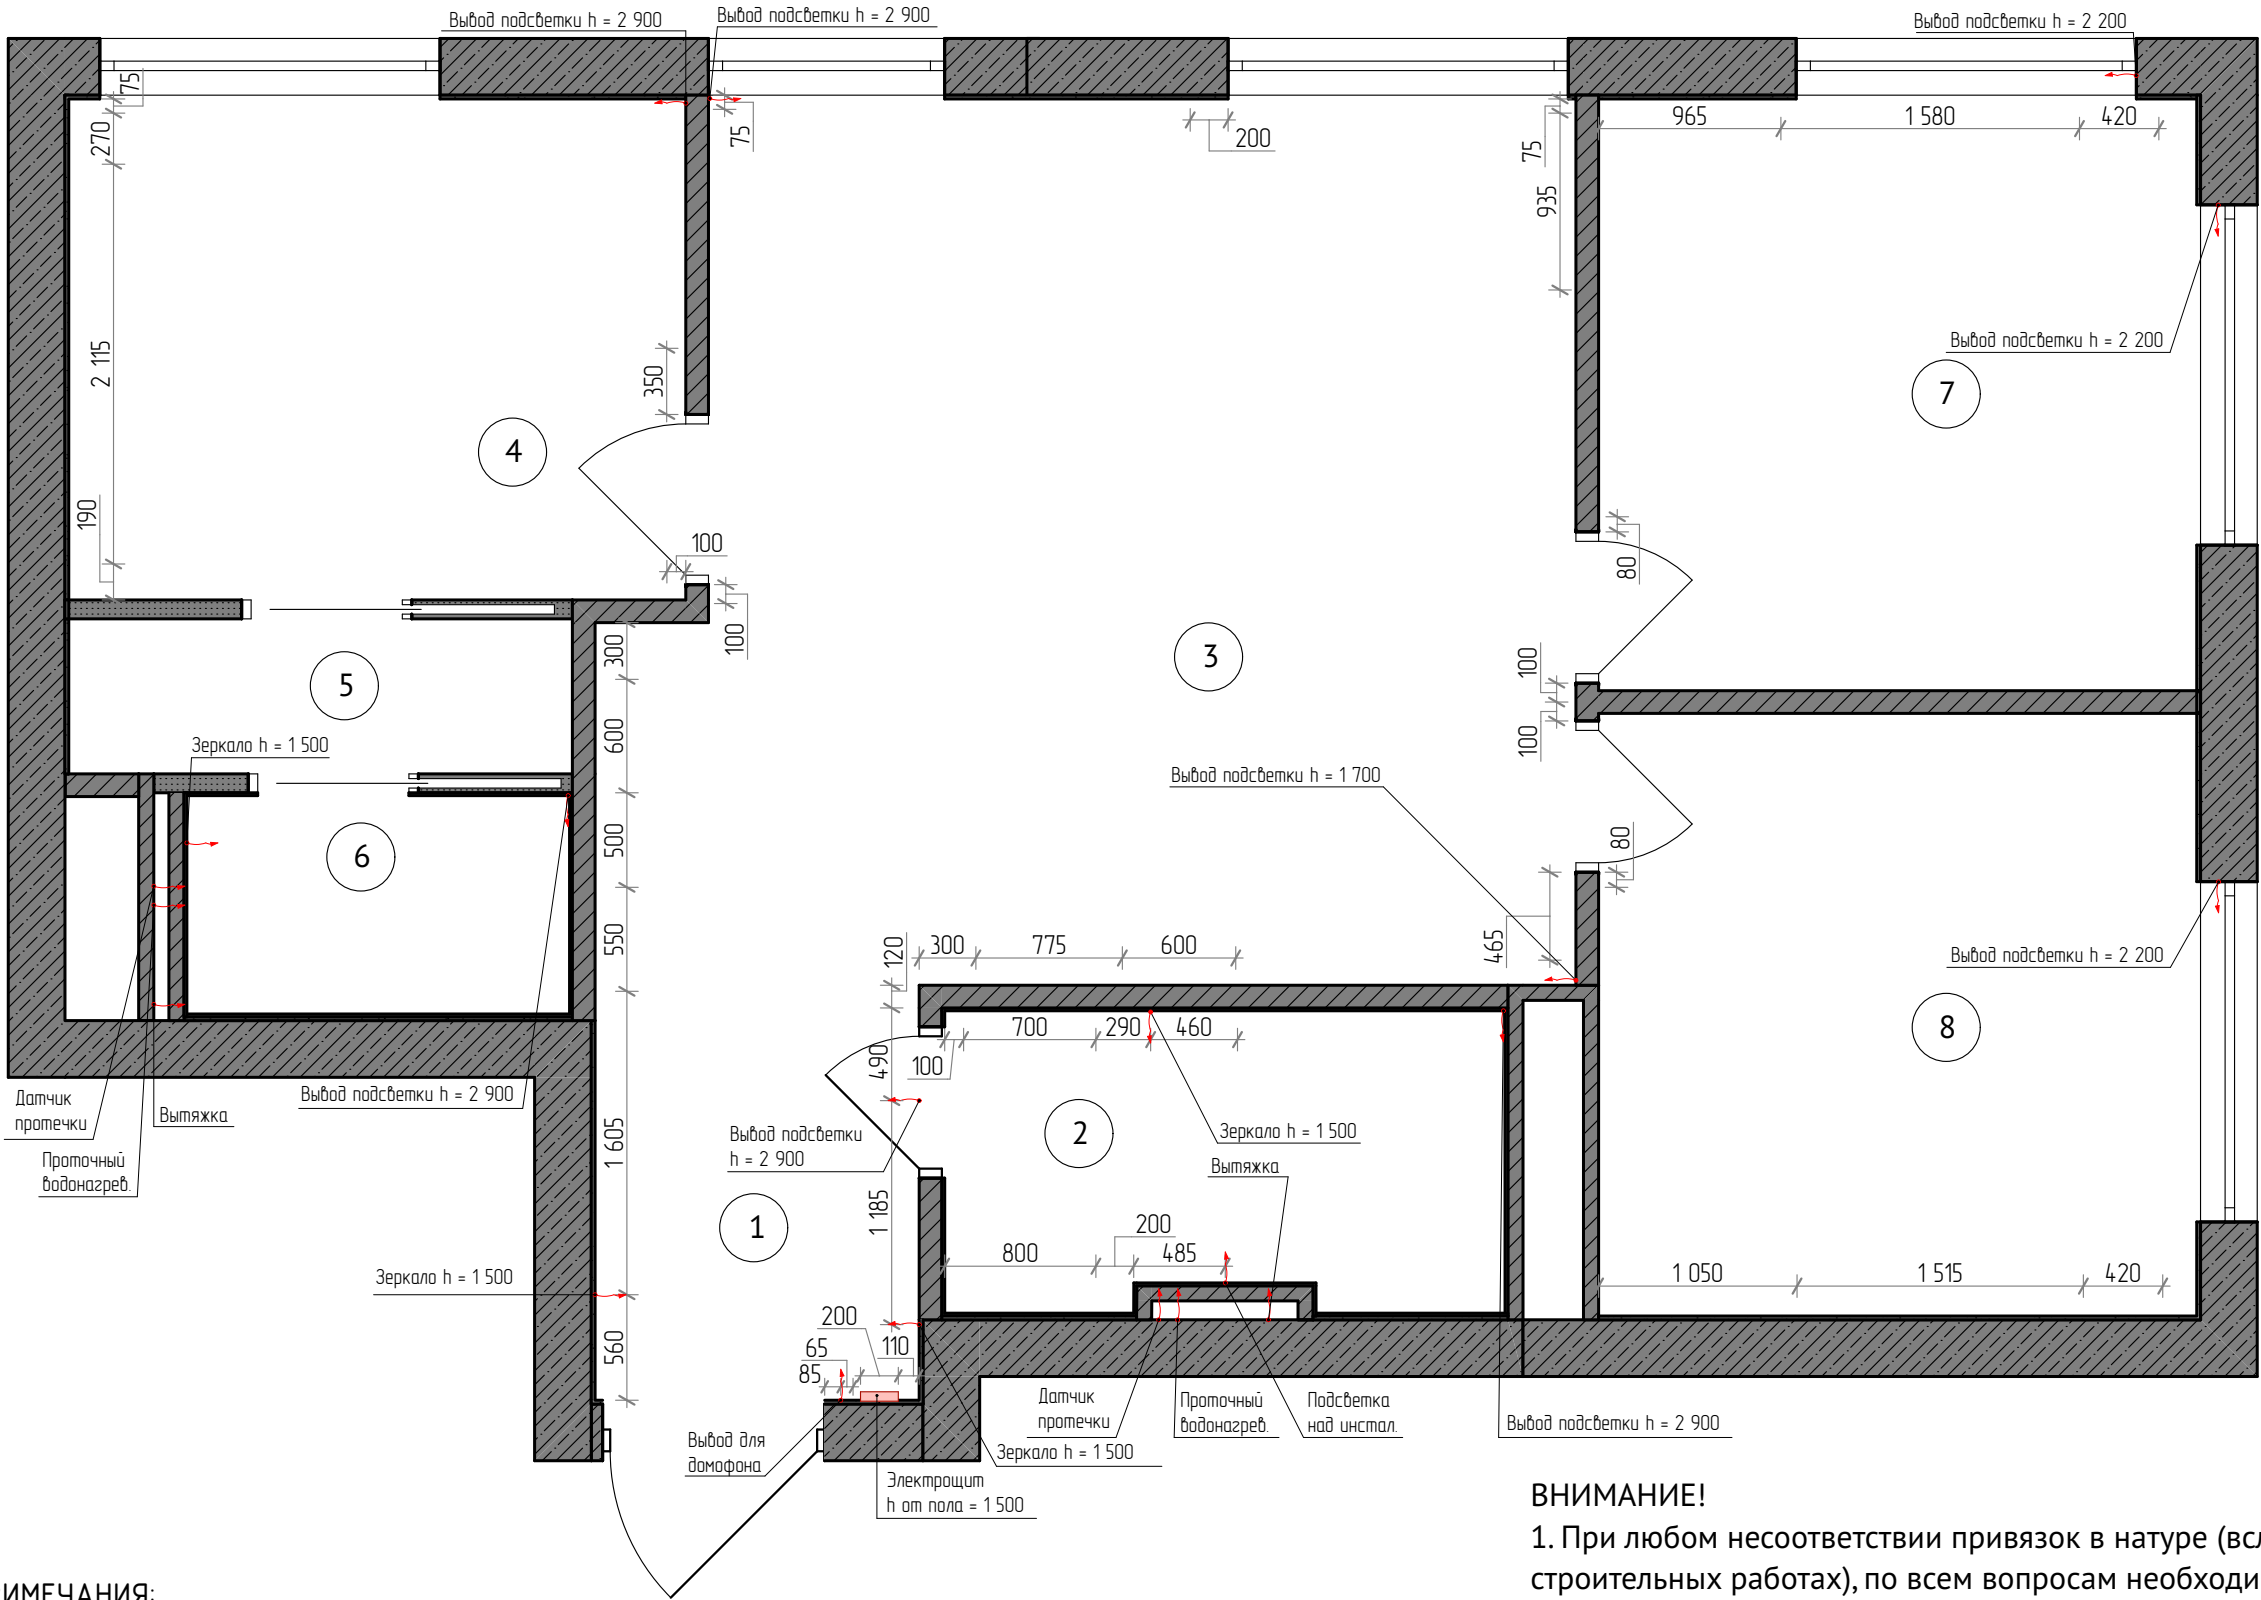

ПРИМЕЧАНИЯ:

- Данный лист рассматривать совместно с разделом ЭО.
- Розетки и электропроводы для кухонного оборудования, их количество и привязки согласовать по тех.картам поставщиков при заказе мебели.
- Пожарная и охранная сигнализация выполняются по отдельным проектам. Предусмотреть питание и сигнальные кабели для датчиков.
- Спутниковое ТВ, электропитание специальных устройств, бытовой техники, аудиосистем, электроники предусмотреть в соответствии с их особенностями.
- Все размеры, указанные на чертежах, условны и требуют уточнения после проведения монтажных работ.

ВНИМАНИЕ!

- При любом несоответствии привязок в натуре (вследствии погрешности в обмерах и строительных работах), по всем вопросам необходимо обратиться к авторам проекта для внесения соответствующих корректировок на месте.
- Любые отклонения от плана БТИ подлежат согласованию в муниципальных органах.
Ответственность за данное нарушение заказчик принимает на себя.

2D-символ	Класс защиты	Вставки(Механизмы)					Вставки(Механизмы) – Количество по типам										Кол.
		Поз. 1	Поз. 2	Поз. 3	Поз. 4	Поз. 5	Розетка 220	Выкл 1 кл.	Выкл 2 кл.	Выкл 3 кл.	Светорегулятор	Розетка TV	Розетка тел.	Розетка сетев.	Спец.	Заглушка	
	IP44	Терморегулятор теплого пола	-	-	-	-	0	0	0	0	0	0	0	0	1	0	1
	IP20	Выключатель 1 клавишный Мастер-свет	Выключатель 2 клавишный проходной	Розетка 220V	-	-	1	1	1	0	0	0	0	0	0	0	3
	IP20	Выключатель 2 клавишный проходной	Выключатель 2 клавишный проходной	Выключатель 2 клавишный 100-1000W	-	-	0	0	3	0	0	0	0	0	0	0	3
	IP20	Выключатель 2 клавишный проходной	-	-	-	-	0	0	1	0	0	0	0	0	0	0	1
	IP20	Выключатель 2 клавишный (перекрестный)	-	-	-	-	0	0	1	0	0	0	0	0	0	0	1
	IP20	Выключатель 2 клавишный проходной	Выключатель 1 клавишный	Розетка 220V	-	-	1	1	1	0	0	0	0	0	0	0	3
	IP20	Выключатель 1 клавишный	Выключатель 2 клавишный	-	-	-	0	1	1	0	0	0	0	0	0	0	2
	IP20	Розетка 220V	-	-	-	-	1	0	0	0	0	0	0	0	0	0	1
	IP20	Розетка 220V	Терморегулятор теплого пола	-	-	-	1	0	0	0	0	0	0	0	1	0	2
	IP20	Розетка 220V	Розетка 220V	Розетка телевизионная TV-FM	-	-	2	0	0	0	0	1	0	0	0	0	3
	IP20	Розетка 220V	Розетка 220V	Розетка 220V	-	-	3	0	0	0	0	0	0	0	0	0	3
	IP20	Розетка 220V	Розетка 220V	-	-	-	2	0	0	0	0	0	0	0	0	0	2
	IP44	Розетка 220V с заземляющими контактами с крышкой с защитными шторками	Розетка 220V с заземляющими контактами с крышкой с защитными шторками	-	-	-	2	0	0	0	0	0	0	0	0	0	2
	IP44	Розетка 220V	-	-	-	-	1	0	0	0	0	0	0	0	0	0	1


2D-символ	Класс защиты	Вставки(Механизмы)					Вставки(Механизмы) – Количество по типам										Кол.
		Поз. 1	Поз. 2	Поз. 3	Поз. 4	Поз. 5	Розетка 220	Выкл 1 кл.	Выкл 2 кл.	Выкл 3 кл.	Светорегулятор	Розетка TV	Розетка тел.	Розетка сетев.	Спец.	Заглушка	
	IP44	Розетка 220V	Розетка 220V	-	-	-	2	0	0	0	0	0	0	0	0	0	2
	IP20	Розетка 220V с заземляющими контактами	Розетка 220V с заземляющими контактами	-	-	-	2	0	0	0	0	0	0	0	0	0	2
	IP20	Розетка 220V с заземляющими контактами	-	-	-	-	1	0	0	0	0	0	0	0	0	0	1
	IP44	Розетка 220V	Розетка 220V	Выключатель 1 клавишный	-	-	2	1	0	0	0	0	0	0	0	0	3
	IP20	Розетка 220V	Розетка сетевая RJ45 x2	-	-	-	1	0	0	0	0	0	0	1	0	0	2
	IP20	Розетка 220V	Выключатель 1 клавишный Мастер отпущ	-	-	-	1	1	0	0	0	0	0	0	0	0	2
							45	8	14	0	0	2	0	1	3	0	73

Дизайн проект

			Подпись	Дата	Квартира Жк Кинетик
Разработал	Соколов Н.Е.				
Заказчик	Шубалова Е.Е.				

СПЕЦИФИКАЦИЯ ЭЛЕКТРООБОРУДОВАНИЯ

Стадия	Лист	Масштаб
ДП	13	1:40

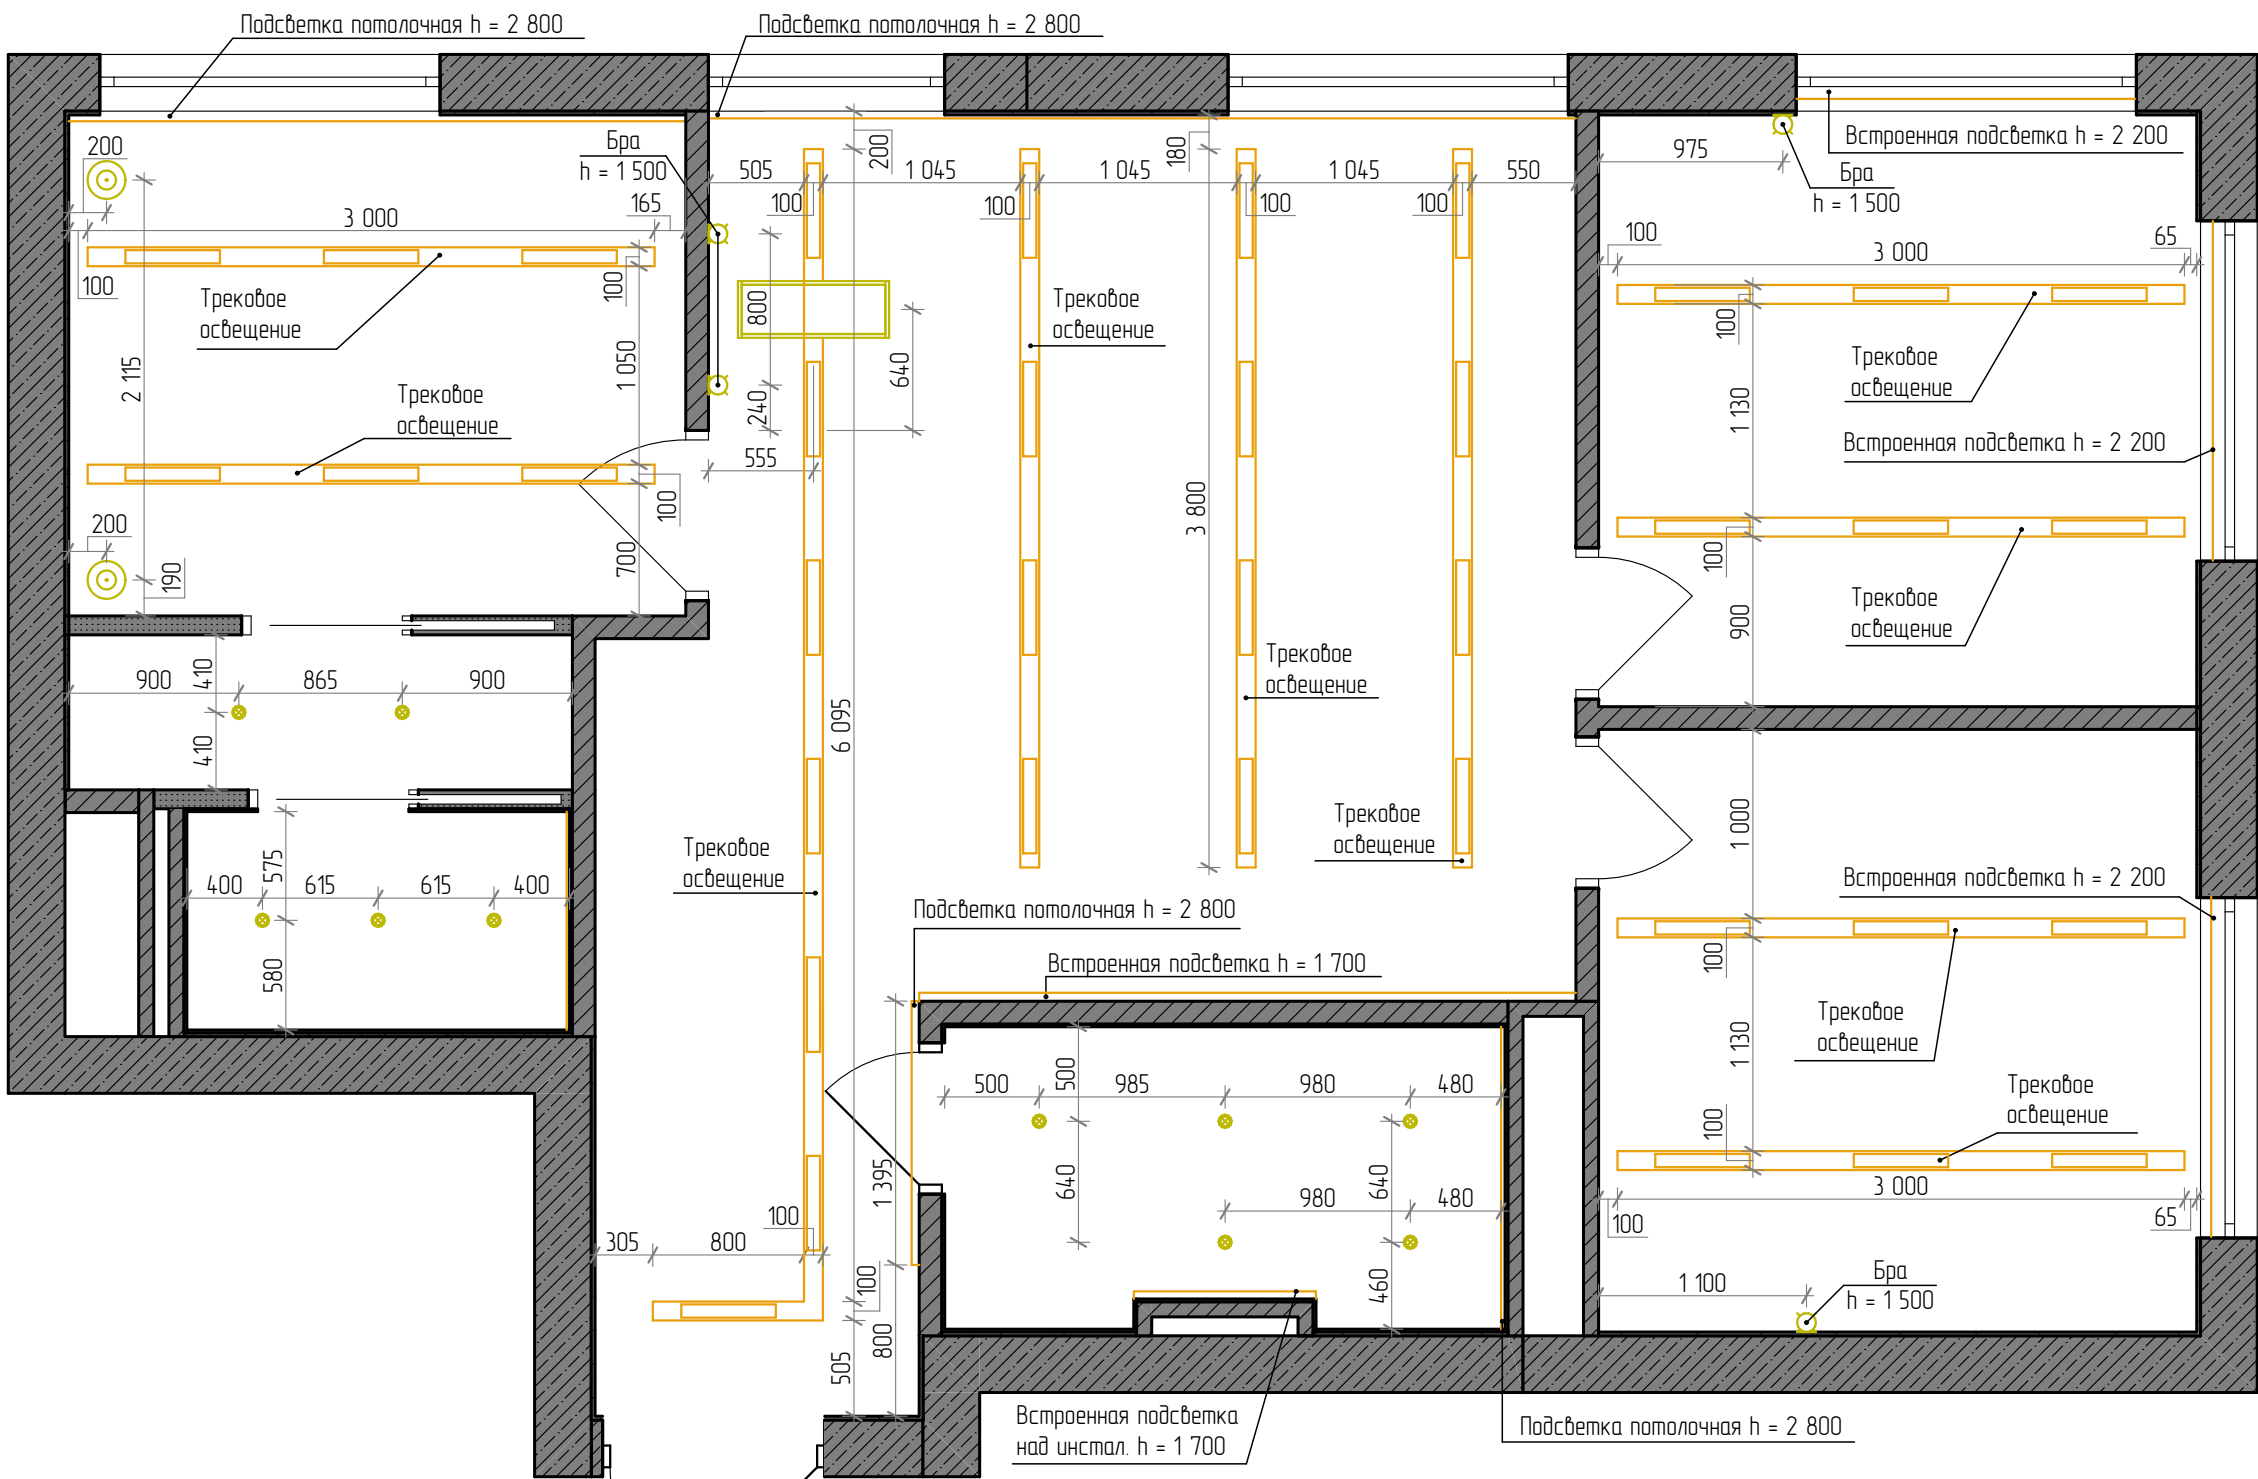

Спецификация освещения

Обозначение на плане	Наименование	Кол-во
●	Точечный светильник	10
—	Подсветка	20,585 м
○	Бра	6
▬	Трековое освещение	35,545 м


ПРИМЕЧАНИЯ:

- Данный лист рассматривать совместно с разделом ЭО.
- Розетки и электровыводы для кухонного оборудования, их количество и привязки согласовать по тех.картам поставщиков при заказе мебели.
- Пожарная и охранная сигнализация выполняются по отдельным проектам. Предусмотреть питание и сигнальные кабели для датчиков.
- Спутниковое ТВ, электропитание специальных устройств, бытовой техники, аудиосистем, электроники предусмотреть в соответствии с их особенностями.
- Все размеры, указанные на чертежах, условны и требуют уточнения после проведения монтажных работ.

ВНИМАНИЕ!
1. При любом несоответствии привязок в натуре (вследствии погрешности в обмерах и строительных работах), по всем вопросам необходимо обратиться к авторам проекта для внесения соответствующих корректировок на месте.
Любые отклонения от плана БТИ подлежат согласованию в муниципальных органах. Ответственность за данное нарушение заказчик принимает на себя.

Спецификация освещения

Обозначение на плане	Наименование	Кол-во
	Точечный светильник	10
	Подсветка	20,585 м
	Бра	4
	Светильник подвесной	2
	Точечное трековое освещение	20,545 м
	Трековое освещение	6,00 м

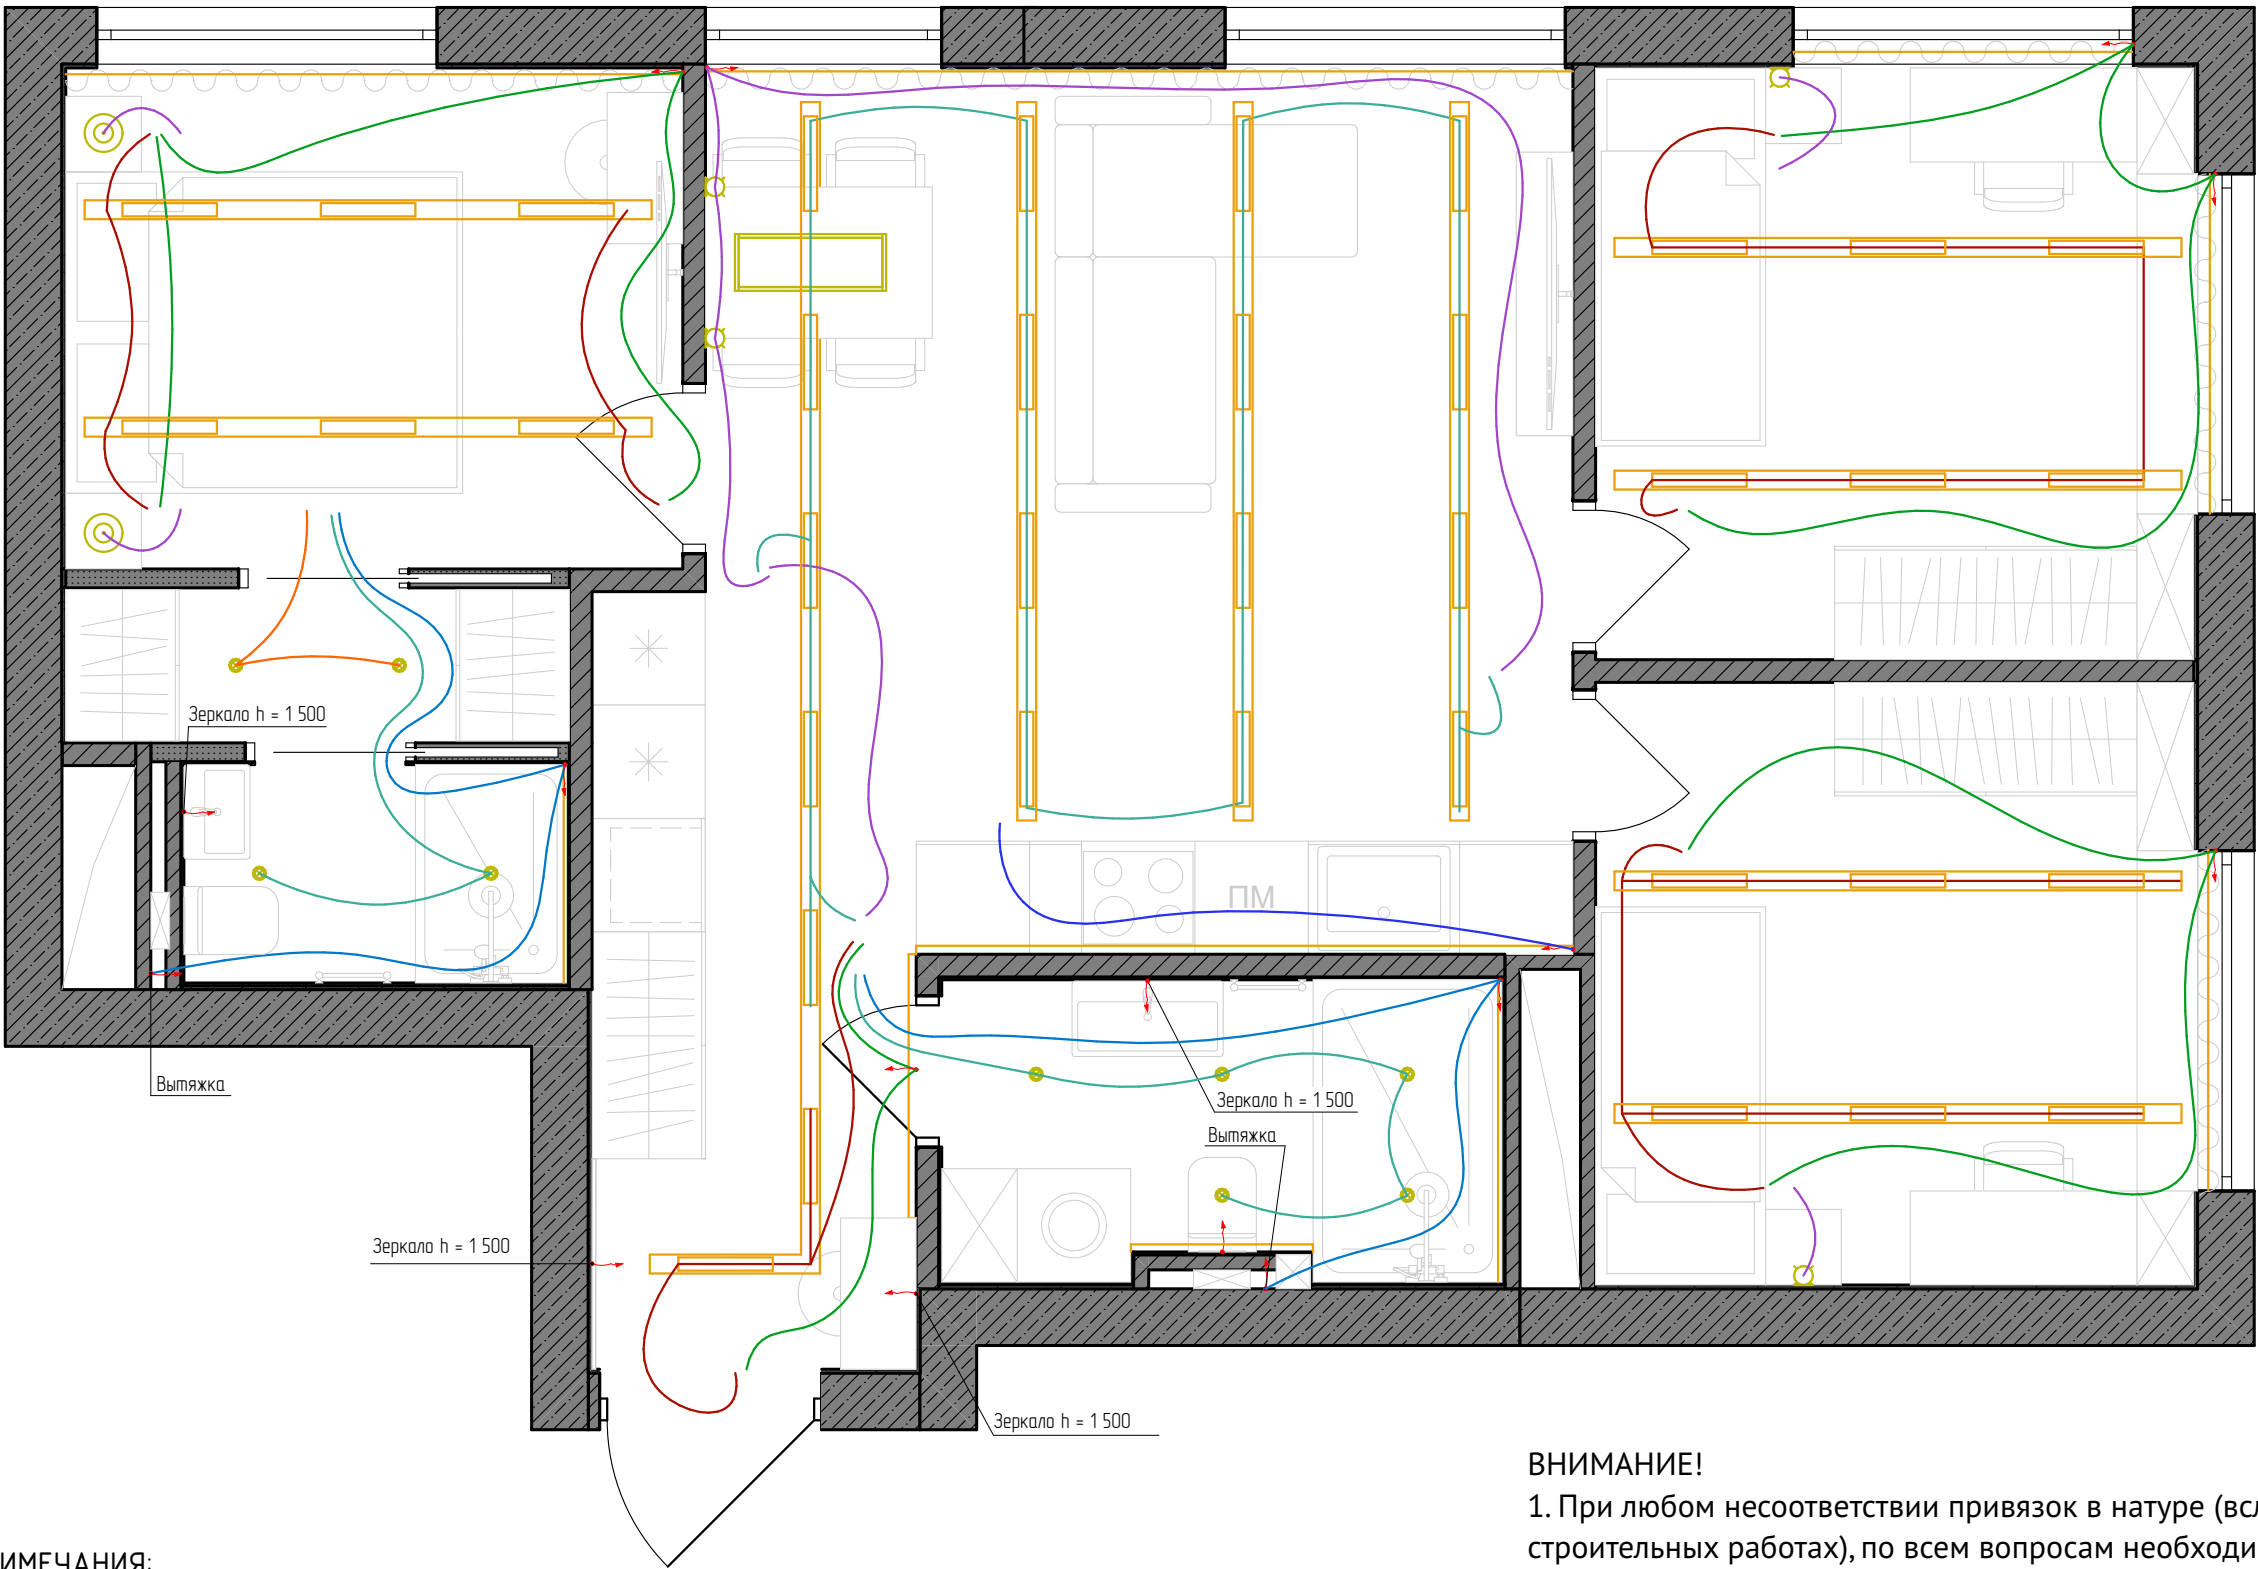

ПРИМЕЧАНИЯ:


1. Данный лист рассматривать совместно с разделом ЭО.
2. Розетки и электровыводы для кухонного оборудования, их количество и привязки согласовать по тех.картам поставщиков при заказе мебели.
3. Пожарная и охранная сигнализация выполняются по отдельным проектам. Предусмотреть питание и сигнальные кабели для датчиков.
4. Спутниковое ТВ, электропитание специальных устройств, бытовой техники, аудиосистем, электроники предусмотреть в соответствии с их особенностями.
5. Все размеры, указанные на чертежах, условны и требуют уточнения после проведения монтажных работ.


ВНИМАНИЕ!

1. При любом несоответствии привязок в натуре (вследствии погрешности в обмерах и строительных работах), по всем вопросам необходимо обратиться к авторам проекта для внесения соответствующих корректировок на месте.
- Любые отклонения от плана БТИ подлежат согласованию в муниципальных органах.
Ответственность за данное нарушение заказчик принимает на себя.

Экспликация помещений


№	Наименование	Площадь, кв.м.
1	Прихожая	3,77
2	Санузел	4,59
3	Кухня-Гостиная	22,73
4	Мастер спальня	8,69
5	Гардеробная	2,19
6	Мастер санузел	2,34
7	Детская 1	9,94
8	Детская 2	10,09
		64,34 м²

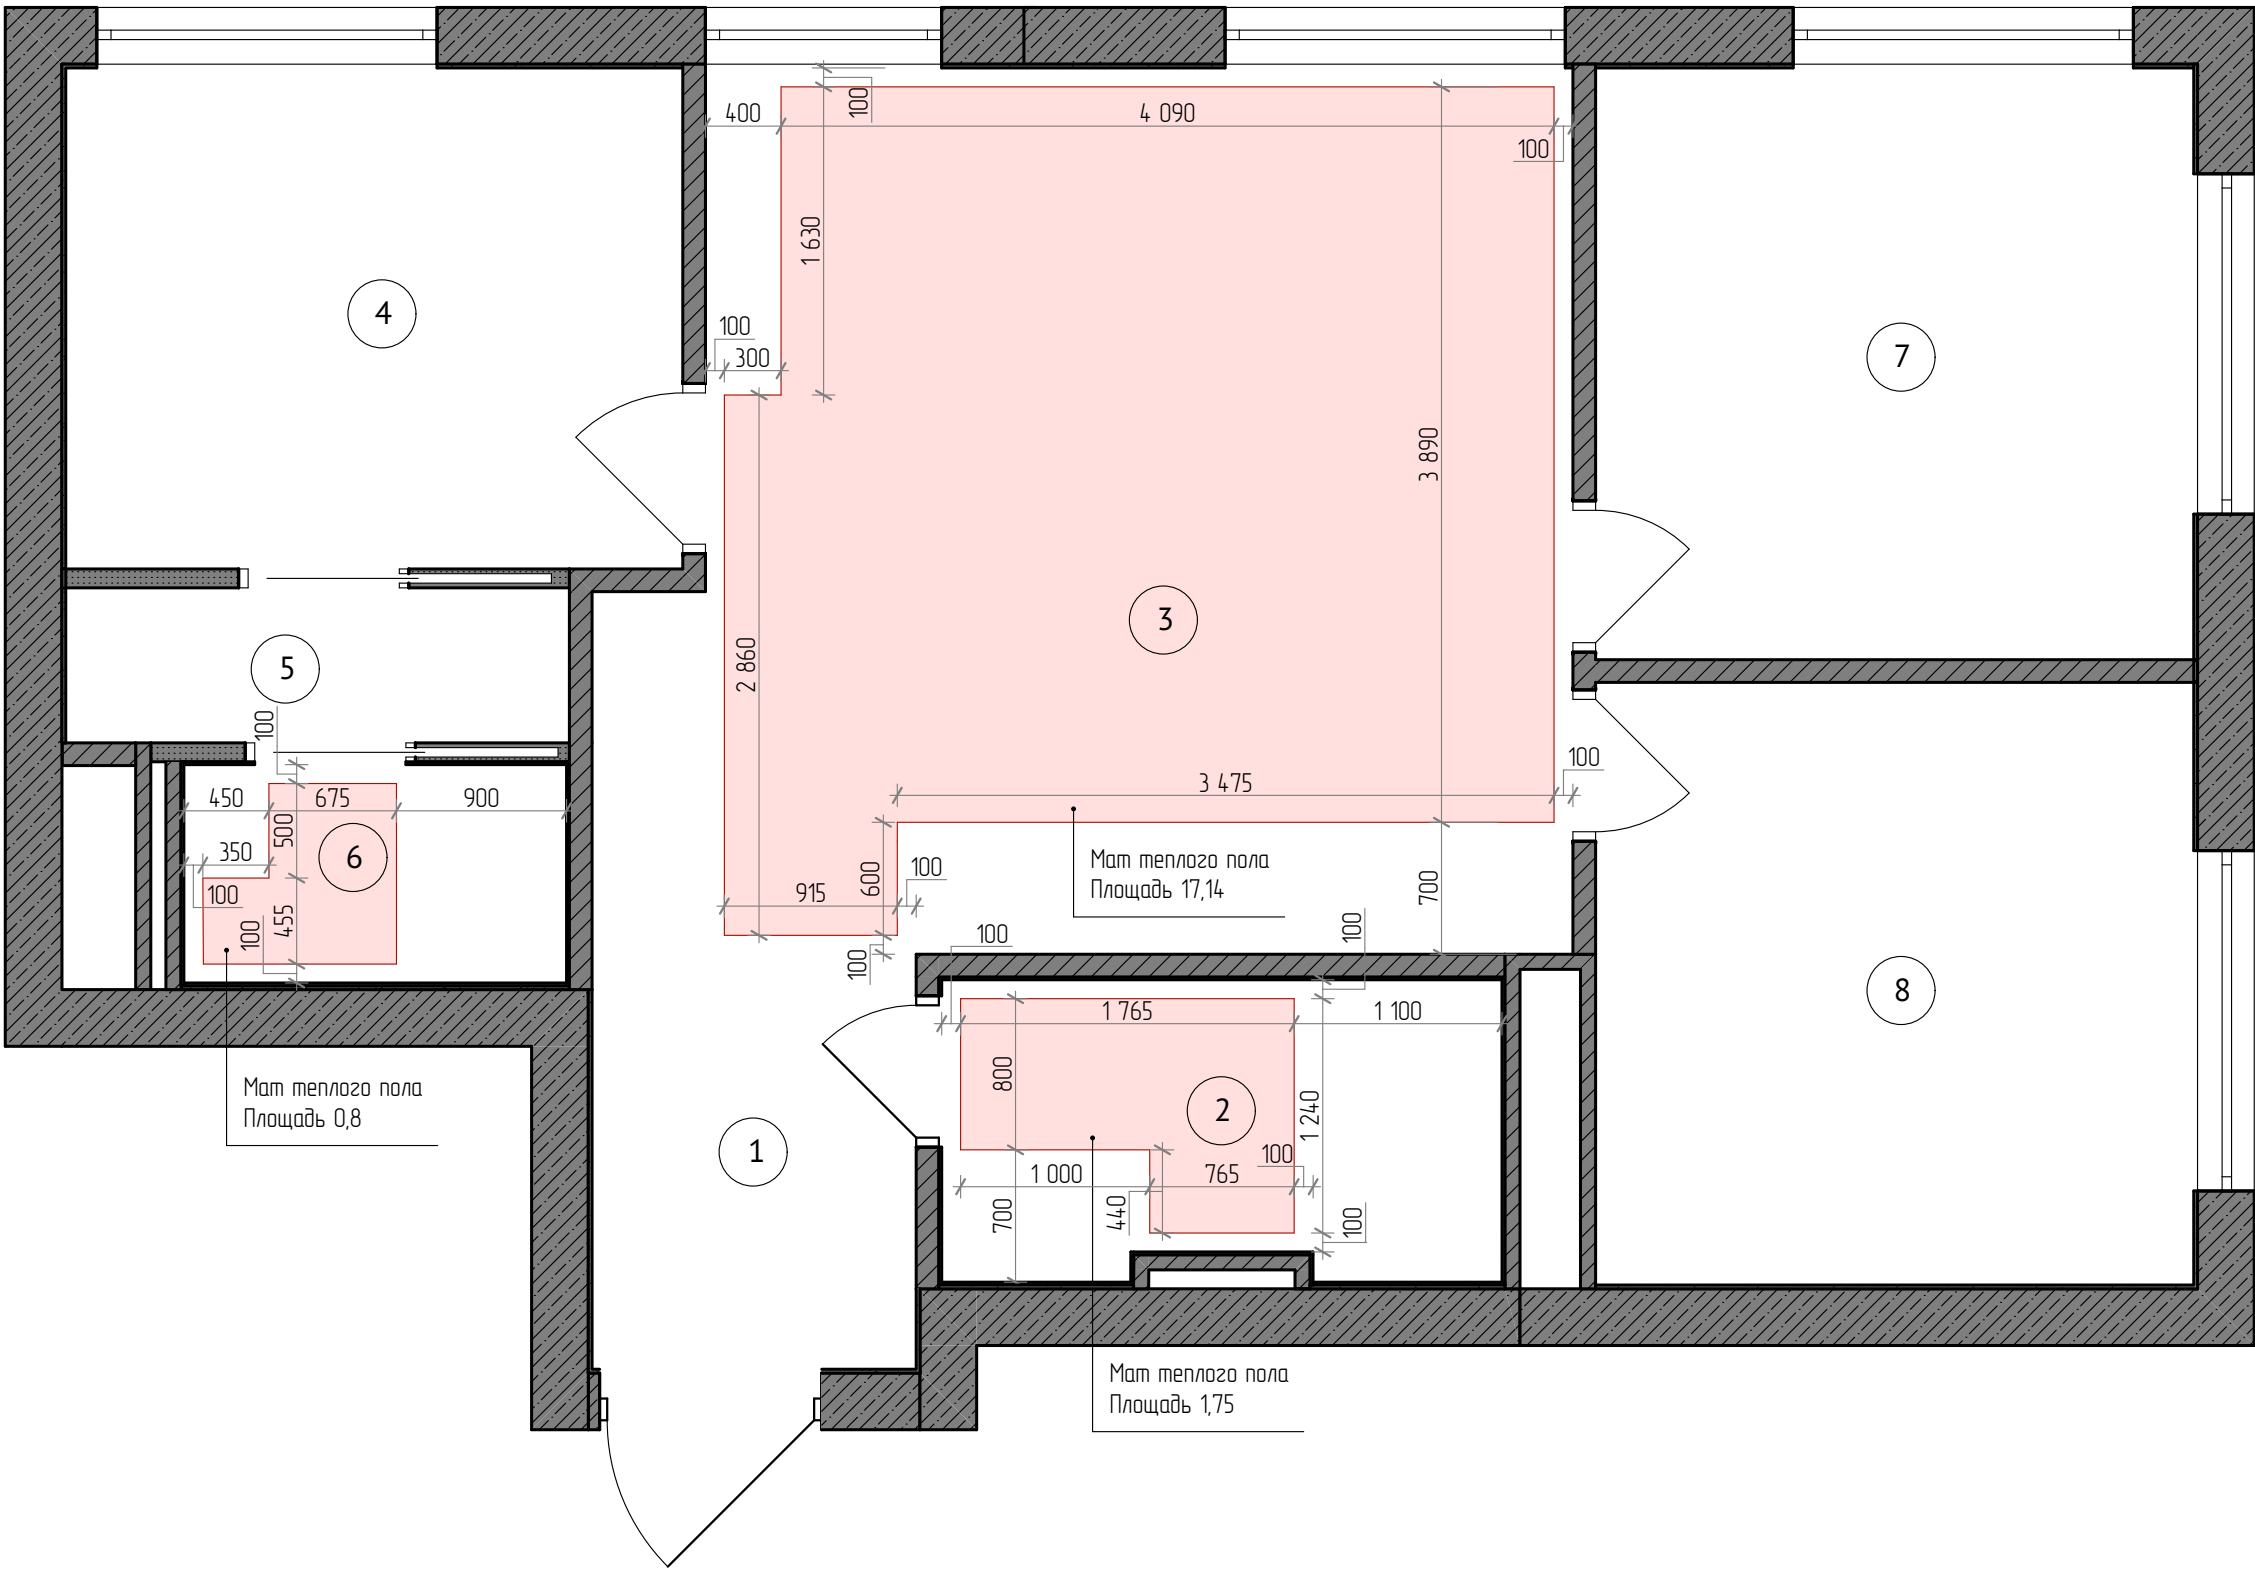

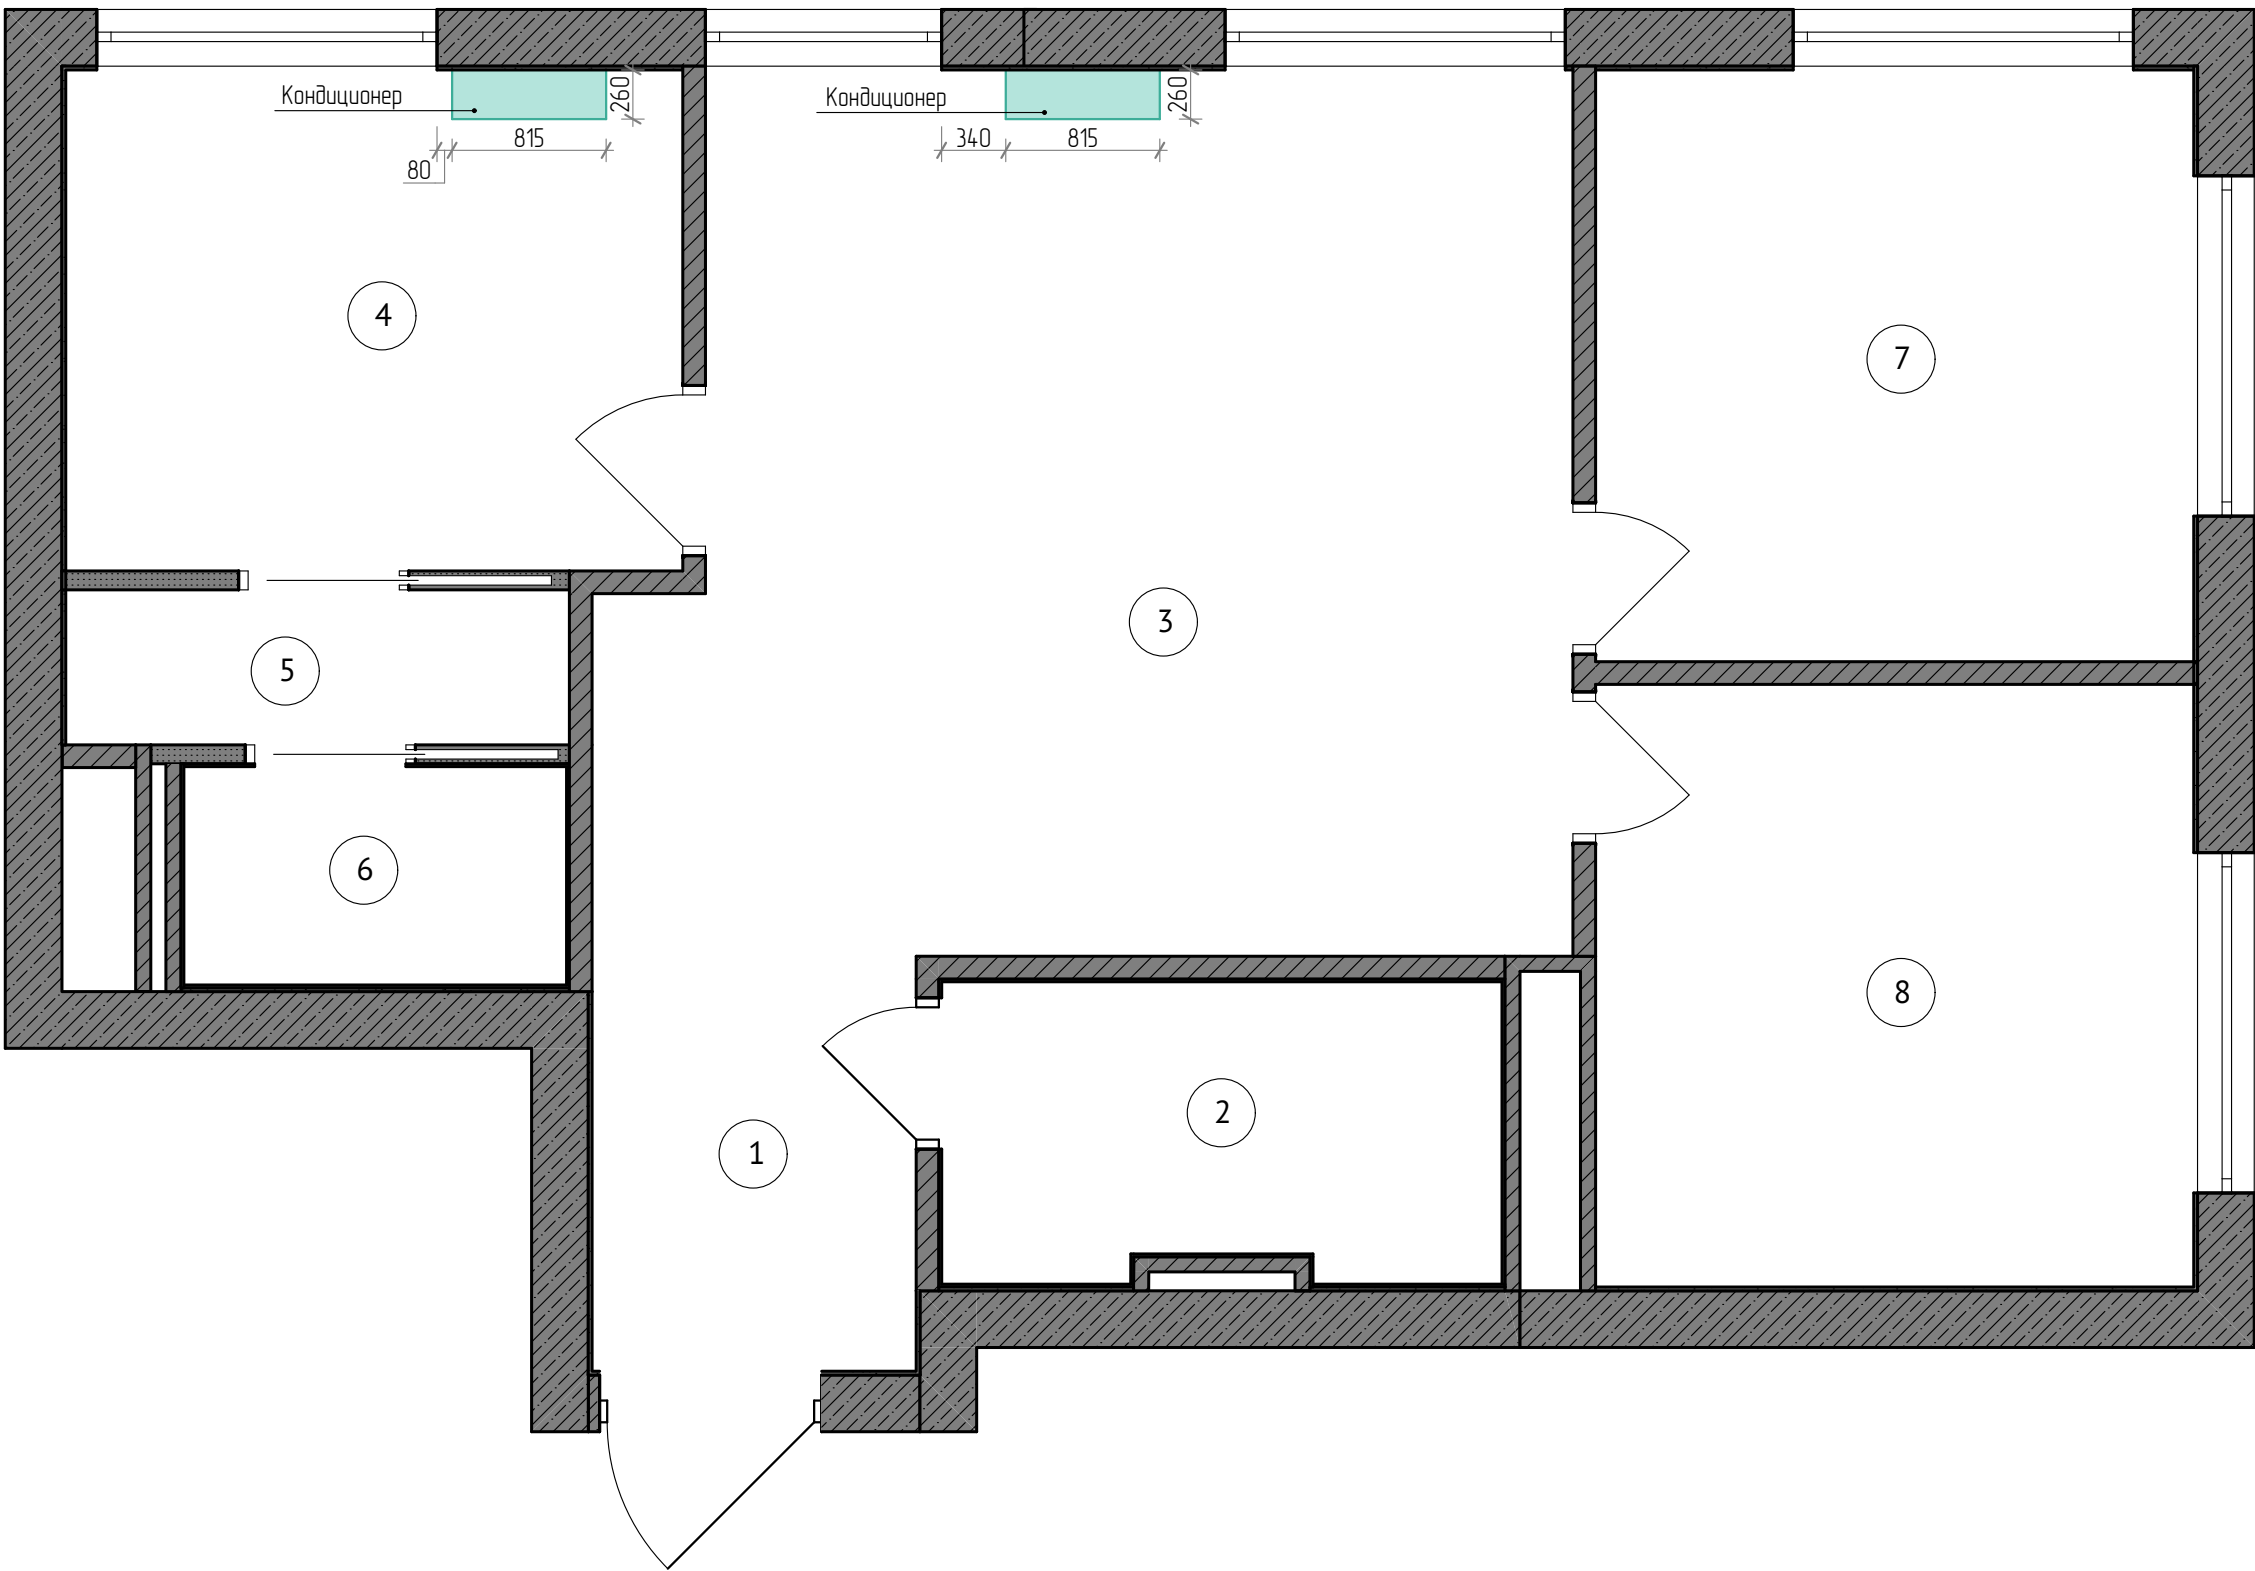

Экспликация помещений

№	Наименование	Площадь, кв.м.
1	Прихожая	3,77
2	Санузел	4,59
3	Кухня-Гостиная	22,73
4	Мастер спальня	8,69
5	Гардеробная	2,19
6	Мастер санузел	2,34
7	Детская 1	9,94
8	Детская 2	10,09
		64,34 м²

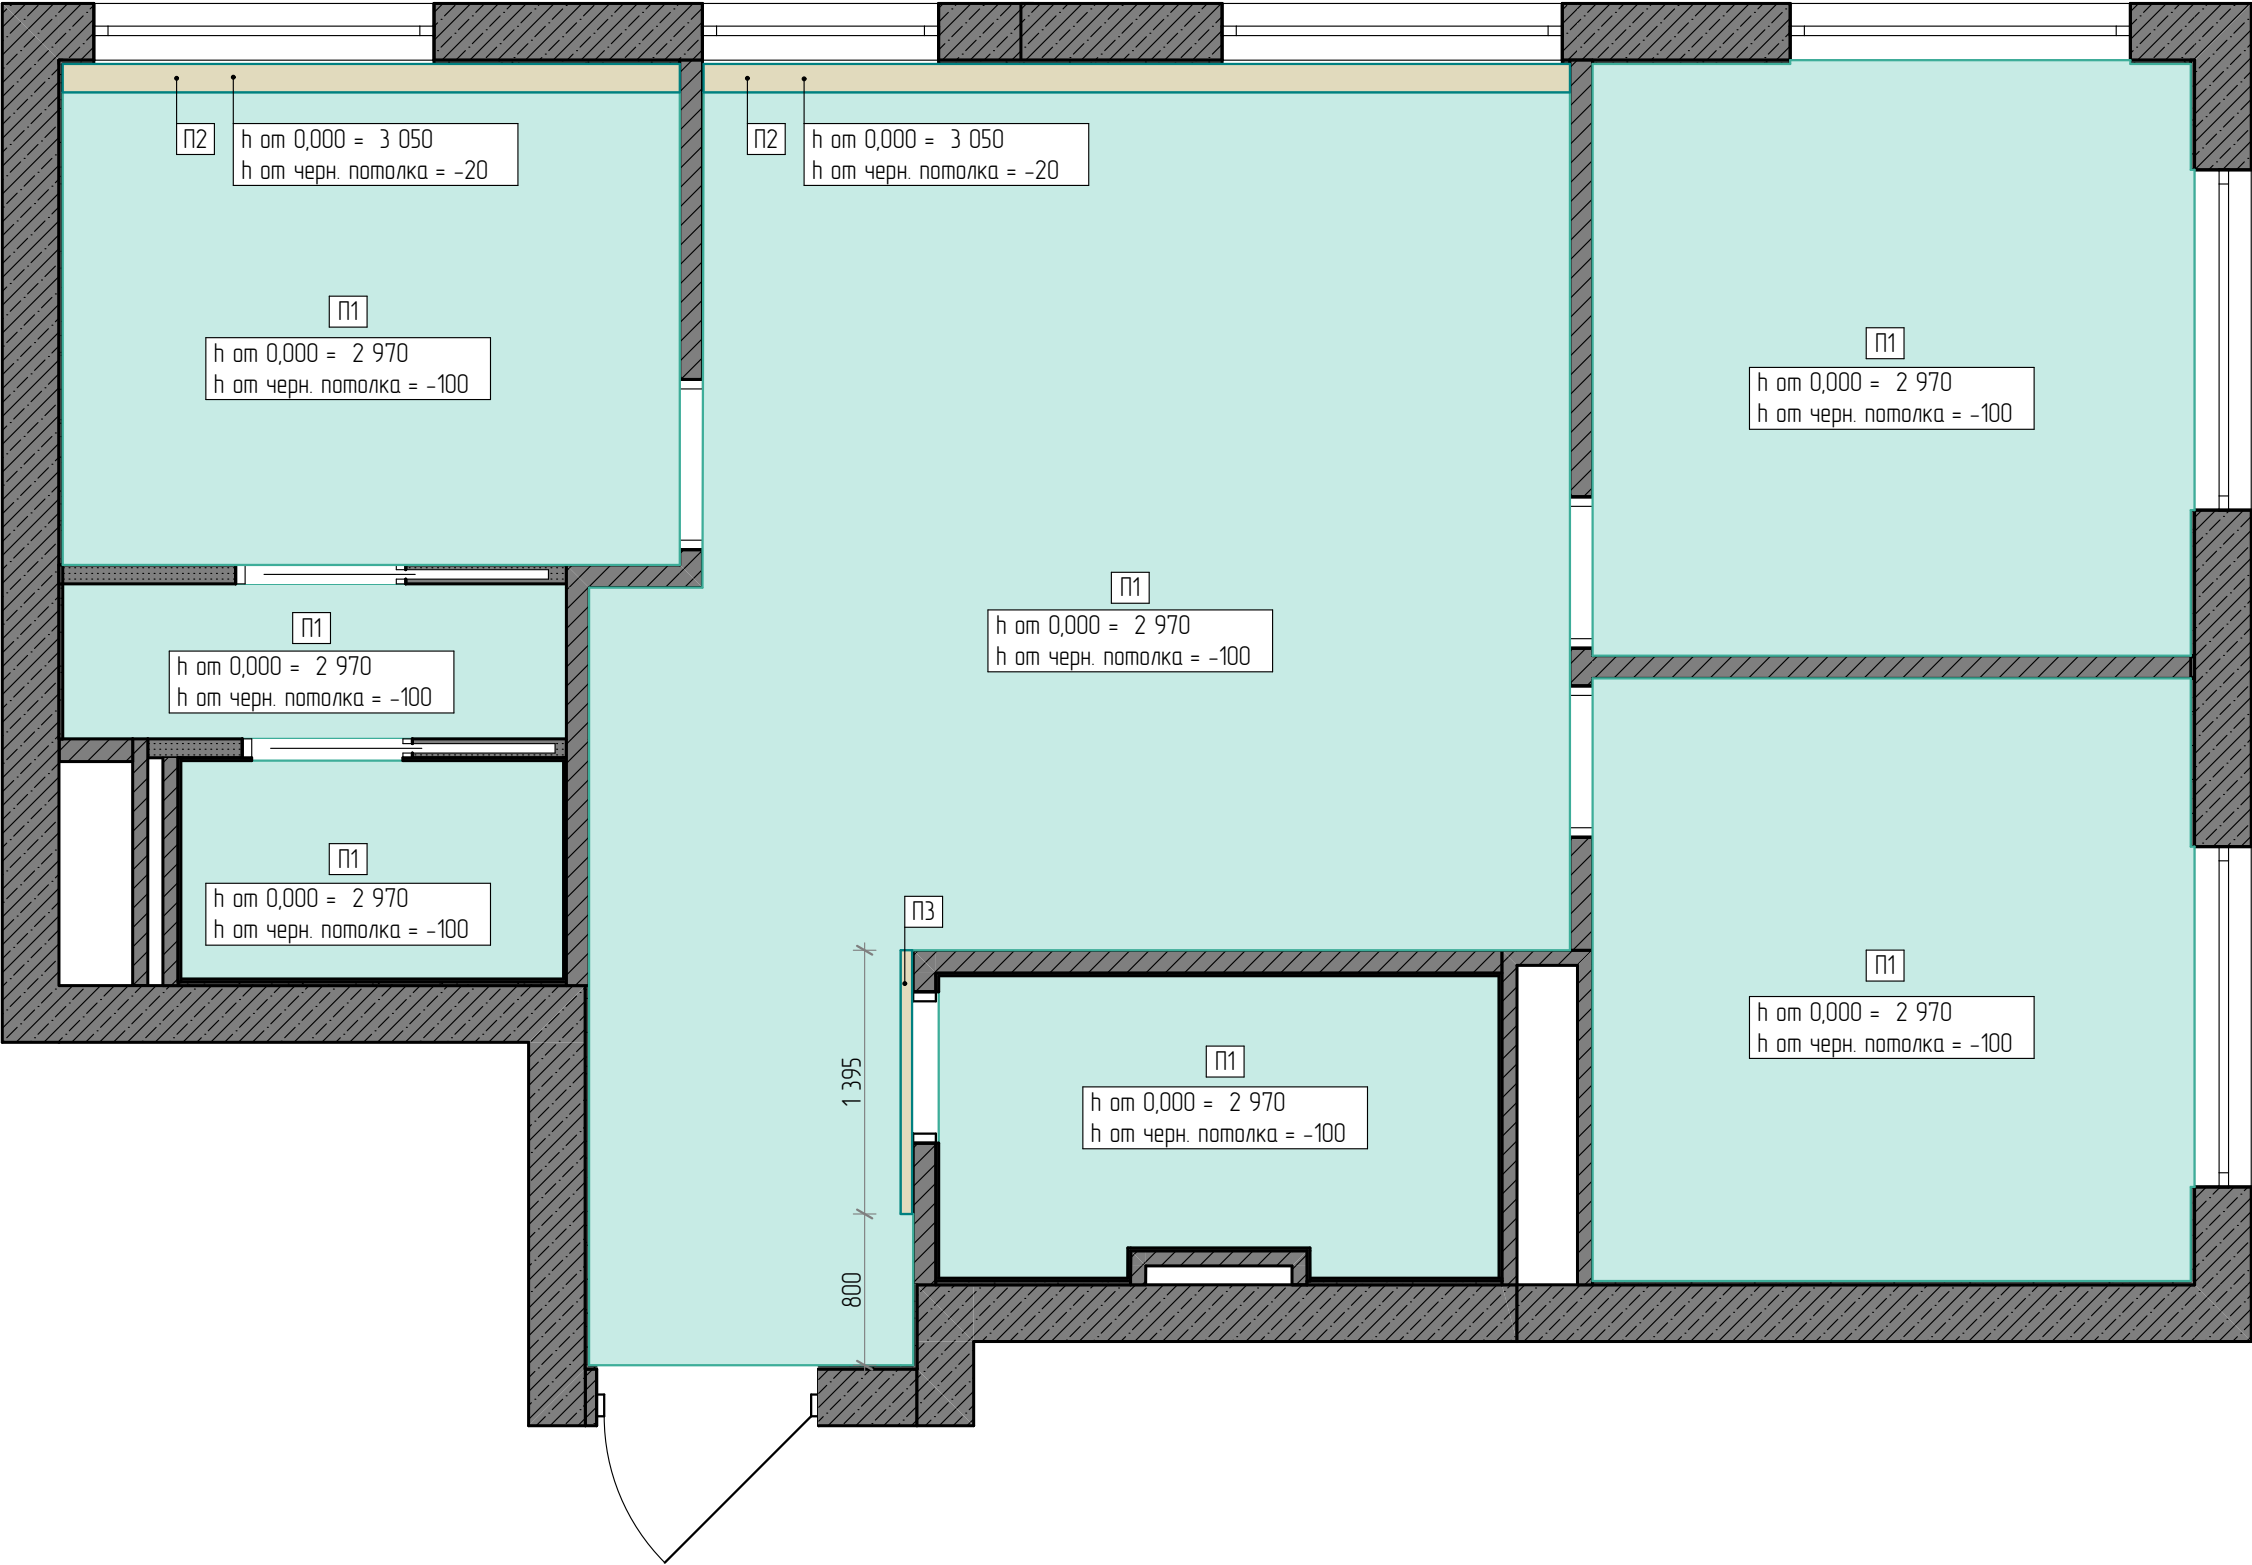


Спецификация отделки потолка

Условное обозначение	Марка	Тип	Площадь, м²
	П1	Натяжной потолок	63,02

Спецификация потолочных элементов

Условное обозначение	Марка	Наименование	Площадь, м²
	П2	Ниша для штор 150мм	1,18
	П3	Ниша для подсветки 60 мм	0,08

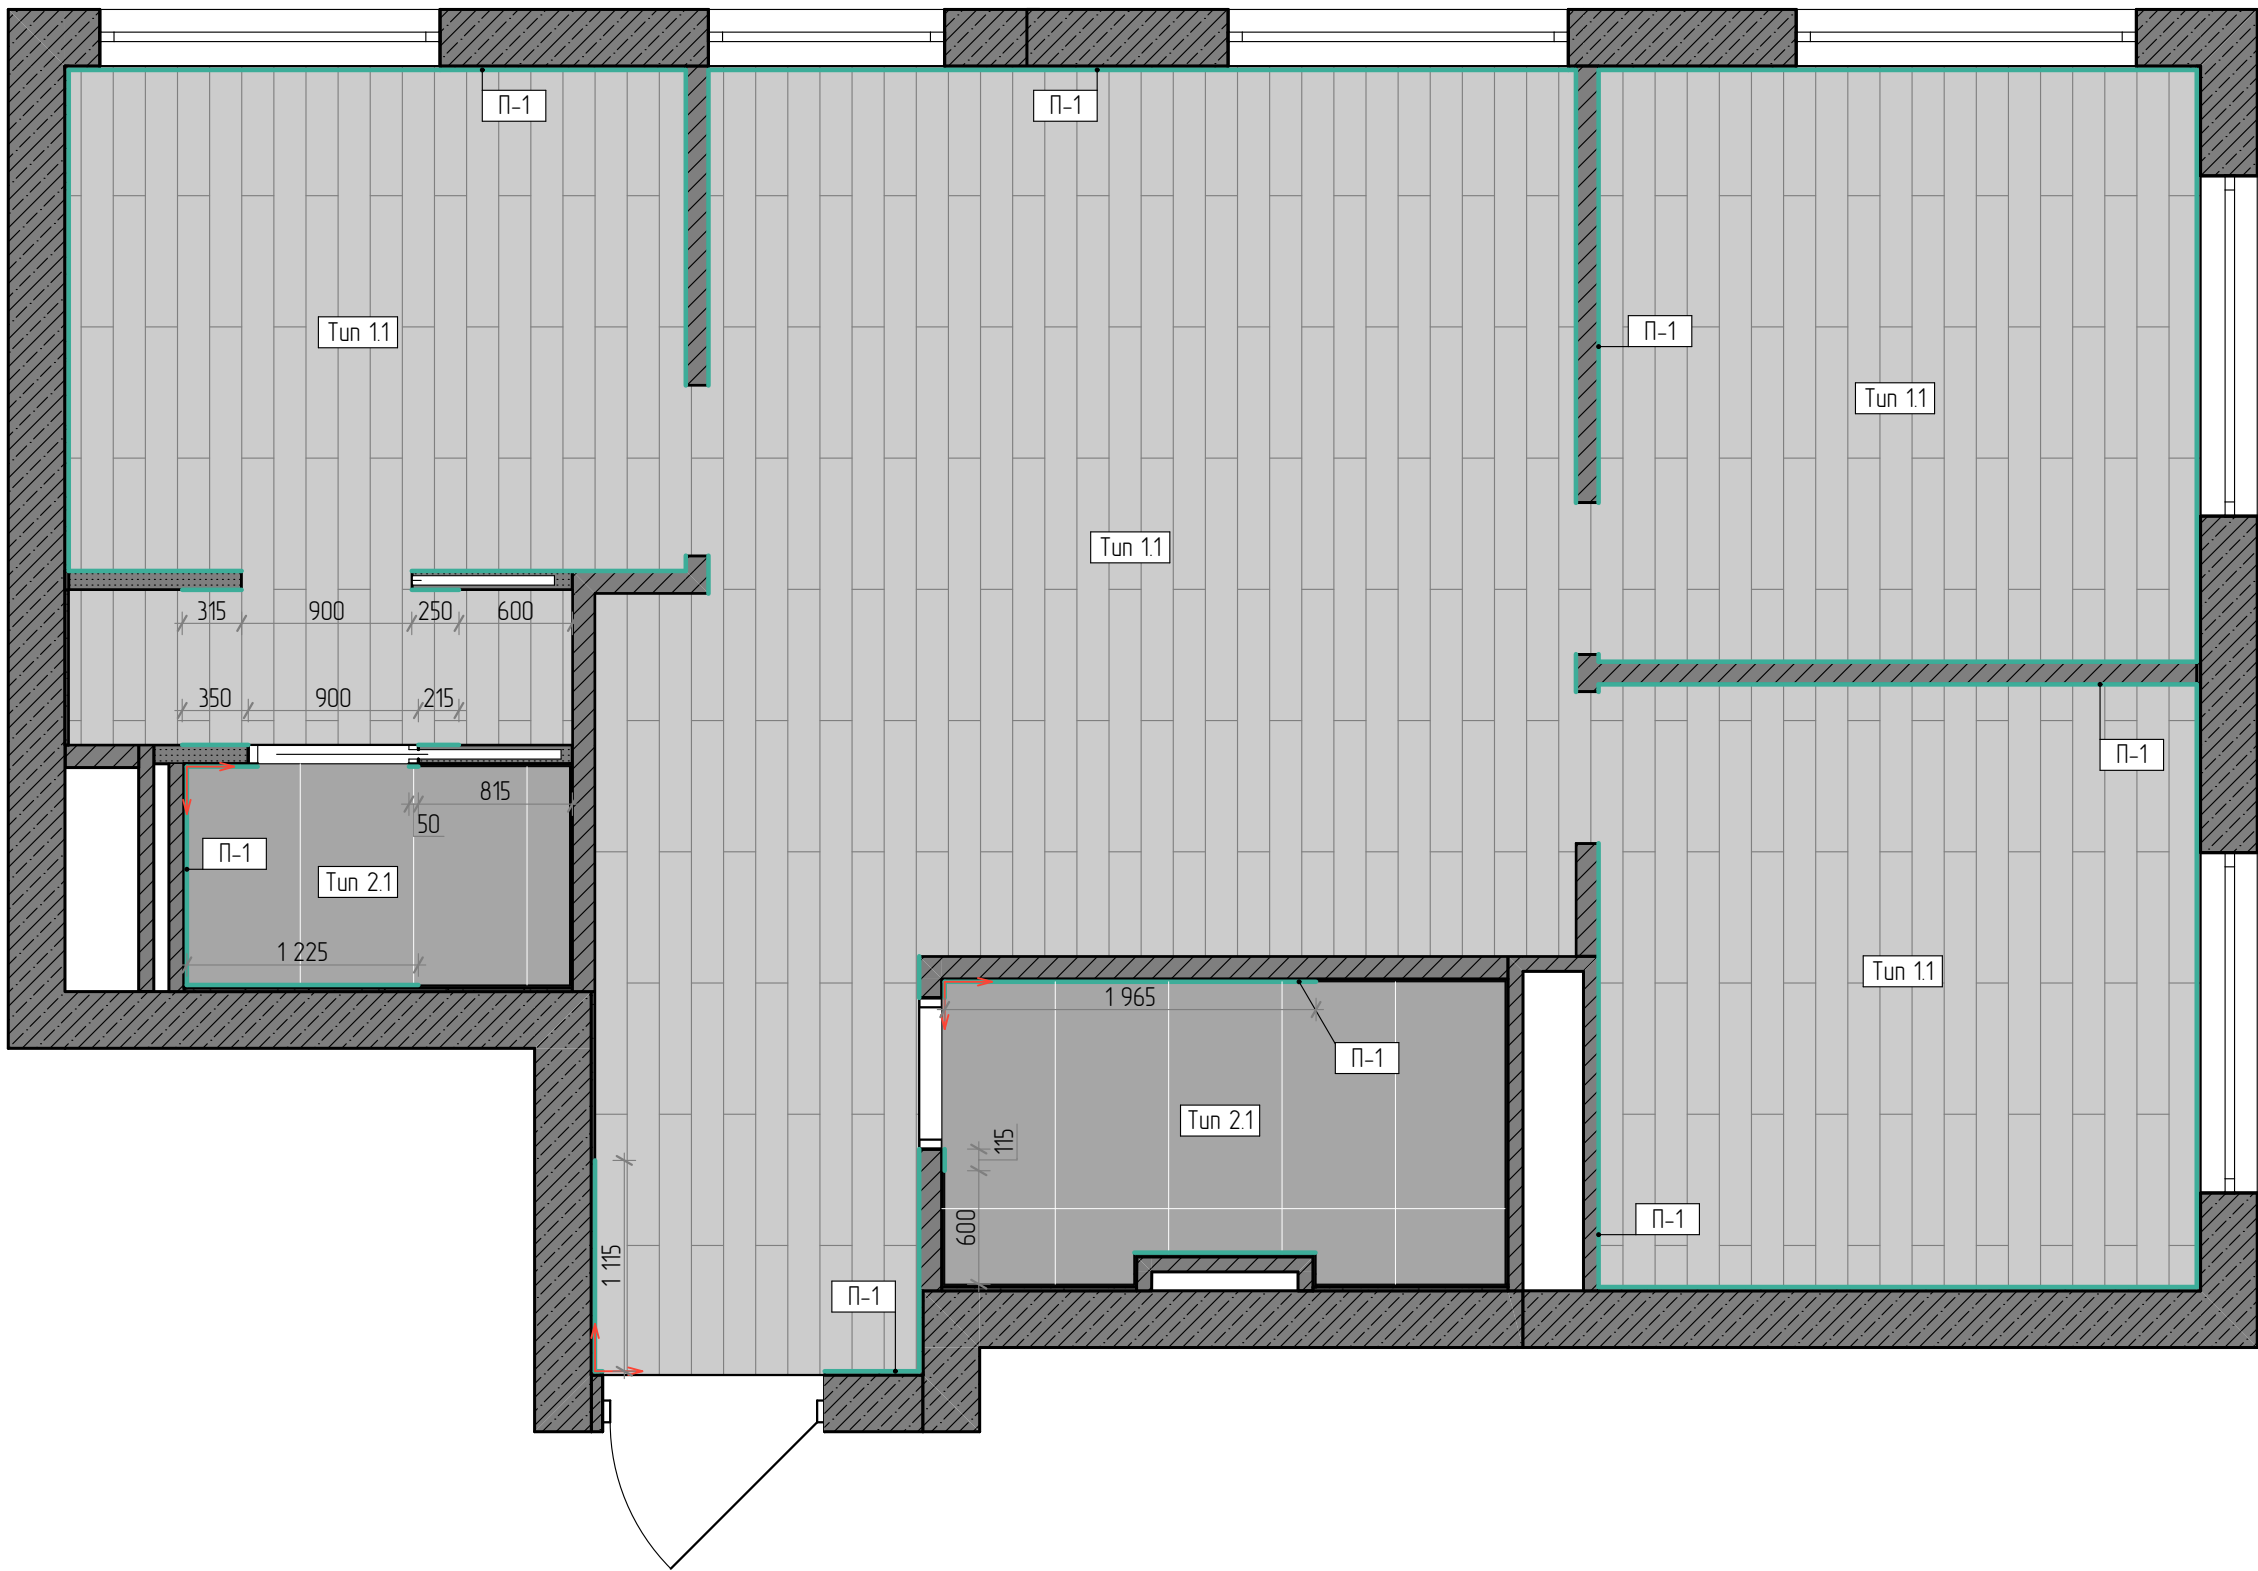

Кол-во плинтуса

Условное обозначение	Марка	Наименование	Кол-во, мм
	П-1	Плинтус	52 785

Напольные покрытия

Условное обозначение	Тип	Наименование	Площадь, м²
	Тип 1.1	Кварцвинил	57,89
	Тип 2.1	Керамогранит 120*60	6,95


ПЛАН ОТДЕЛКИ СТЕН

Экспликация помещений

№	Наименование	Площадь, кв.м.
1	Прихожая	3,77
2	Санузел	4,59
3	Кухня-Гостиная	22,73
4	Мастер спальня	8,69
5	Гардеробная	2,19
6	Мастер санузел	2,34
7	Детская 1	9,94
8	Детская 2	10,09
		64,34 м²

Спецификация отделки стен

Условное обозначение	Тип	Наименование	Площадь, м²
_____	Тип 1	Покраска стен	107,014
_____	Тип 2	Покраска стен	64,58
_____	Тип 3	Керамогранит 60*60	22,42
_____	Тип 4	Керамогранит 60*60	26,68
_____	Тип 5	Керамогранит 60*60	11,02

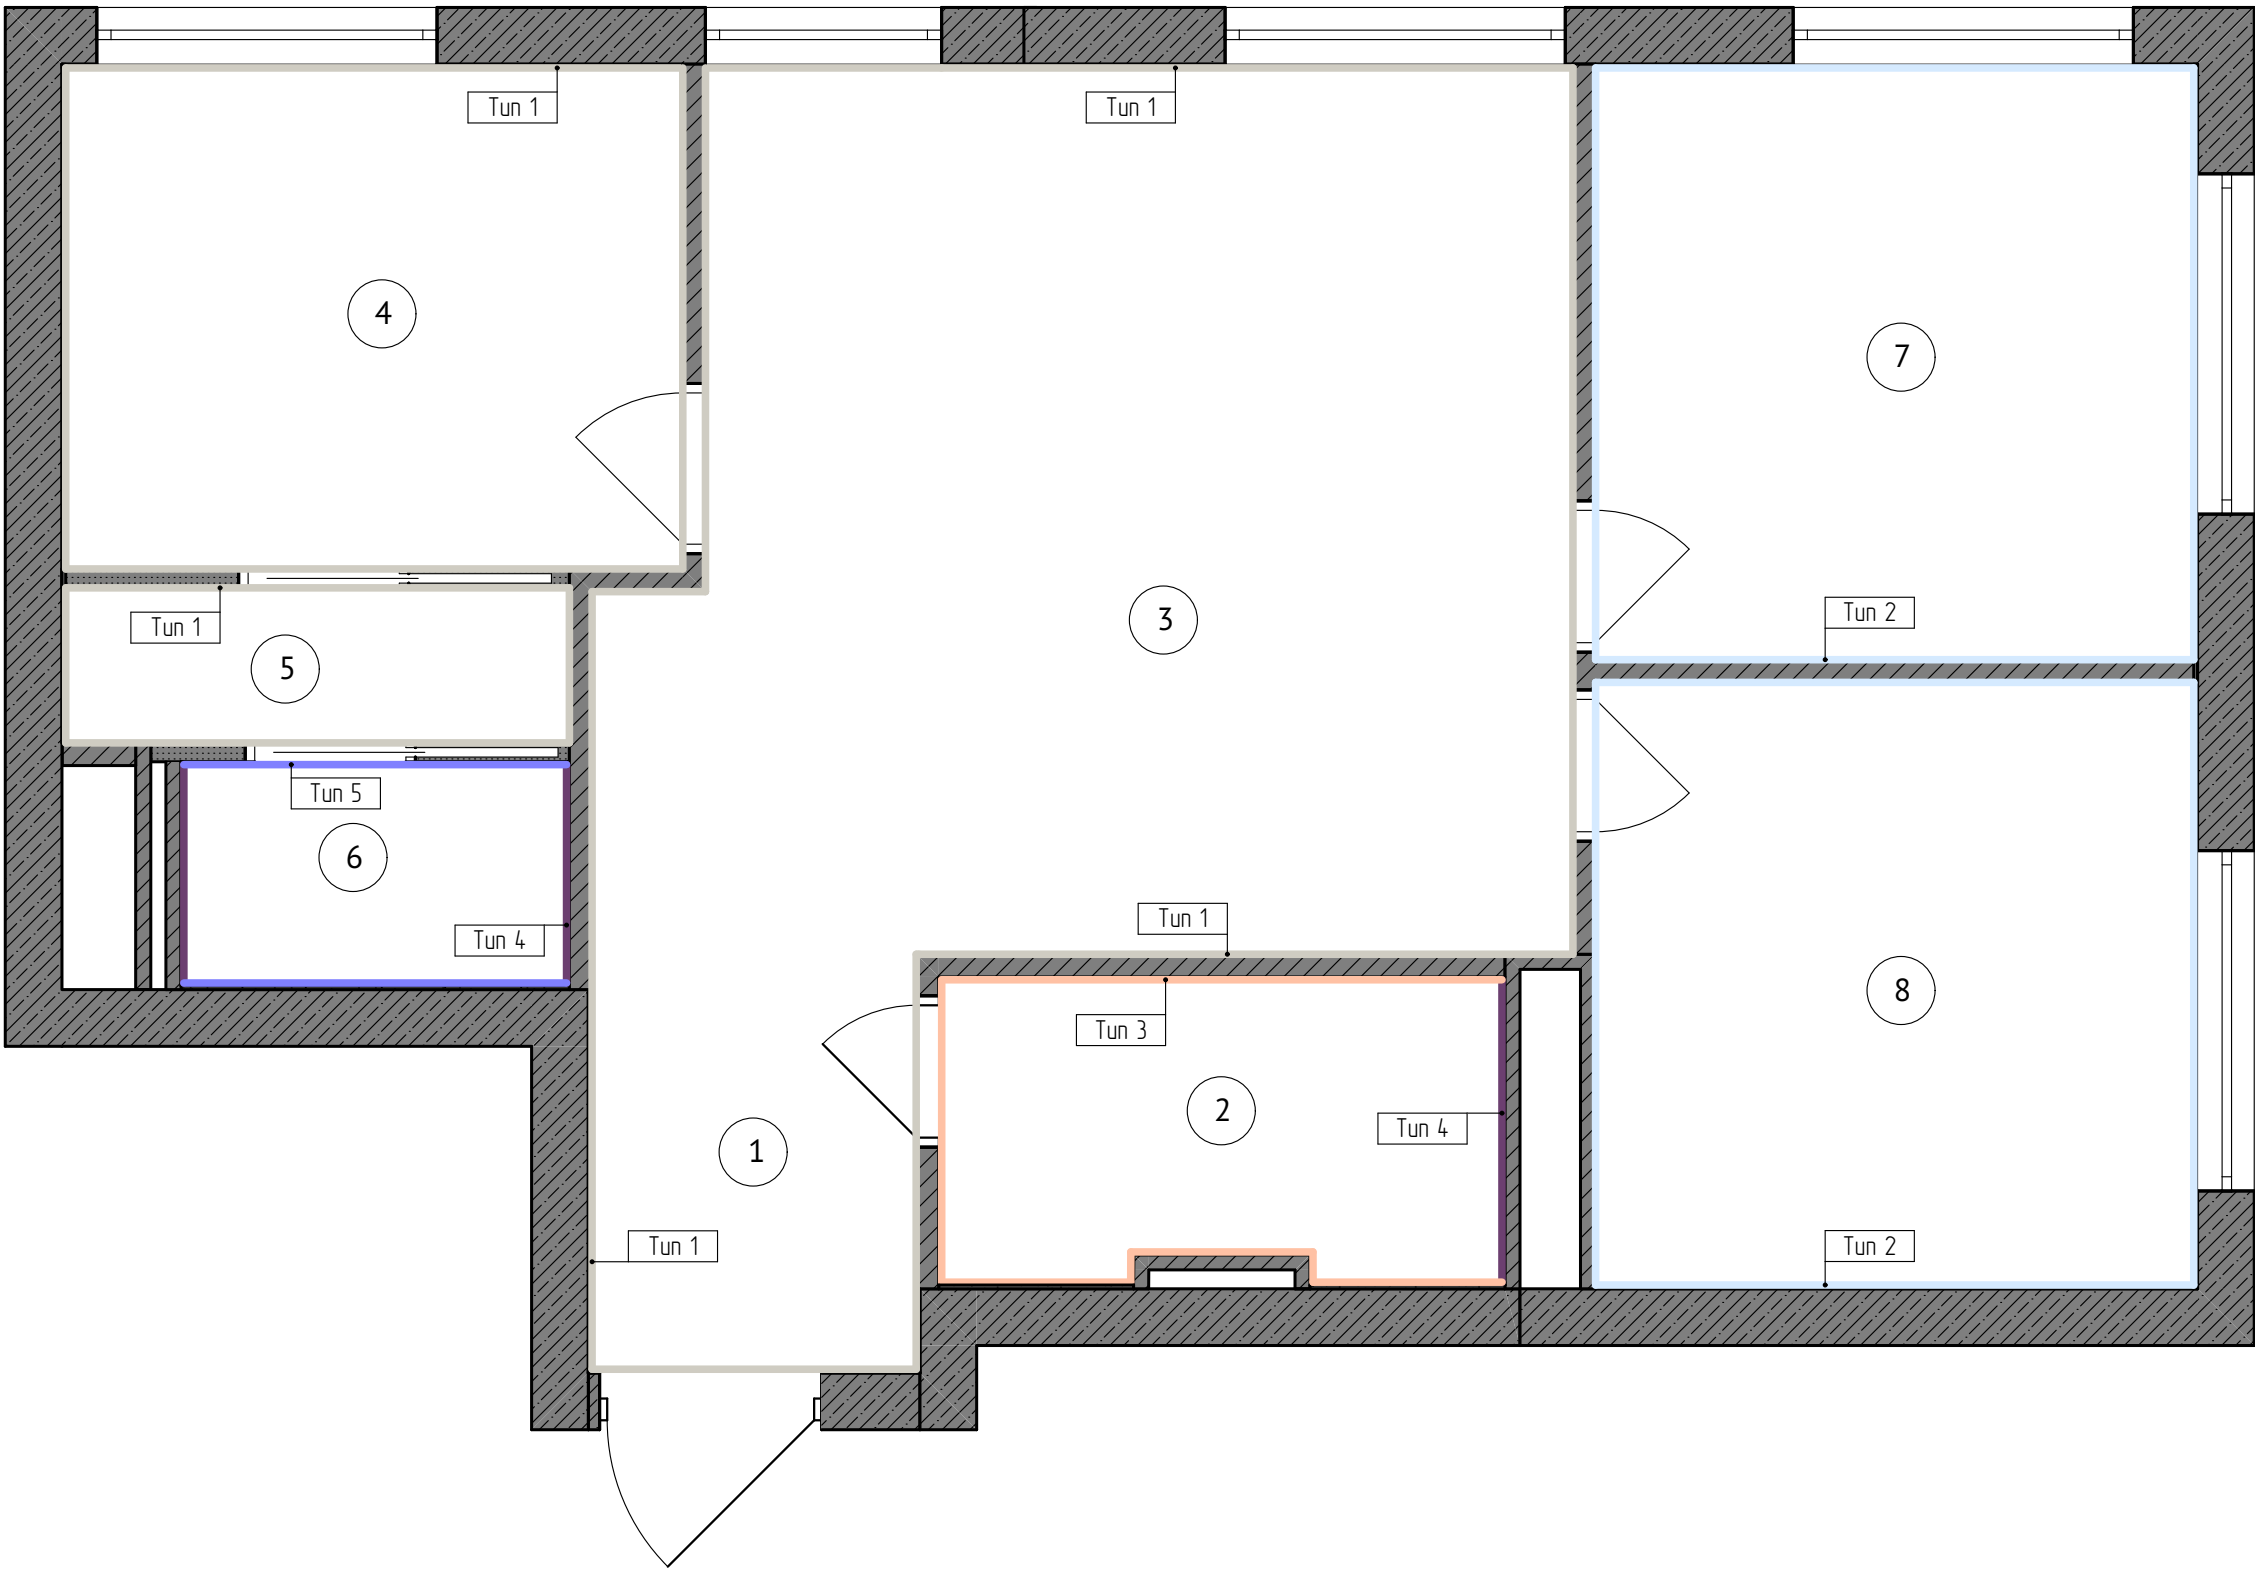


Дизайн проект

Разработал	Соколов Н.Е.	Подпись	Дата	Квартира
Заказчик	Шувалова Е.Е.			Жк Кинетик

ПЛАН ОТДЕЛКИ СТЕН

Стадия	Лист	Масштаб
ДП	20	1:40

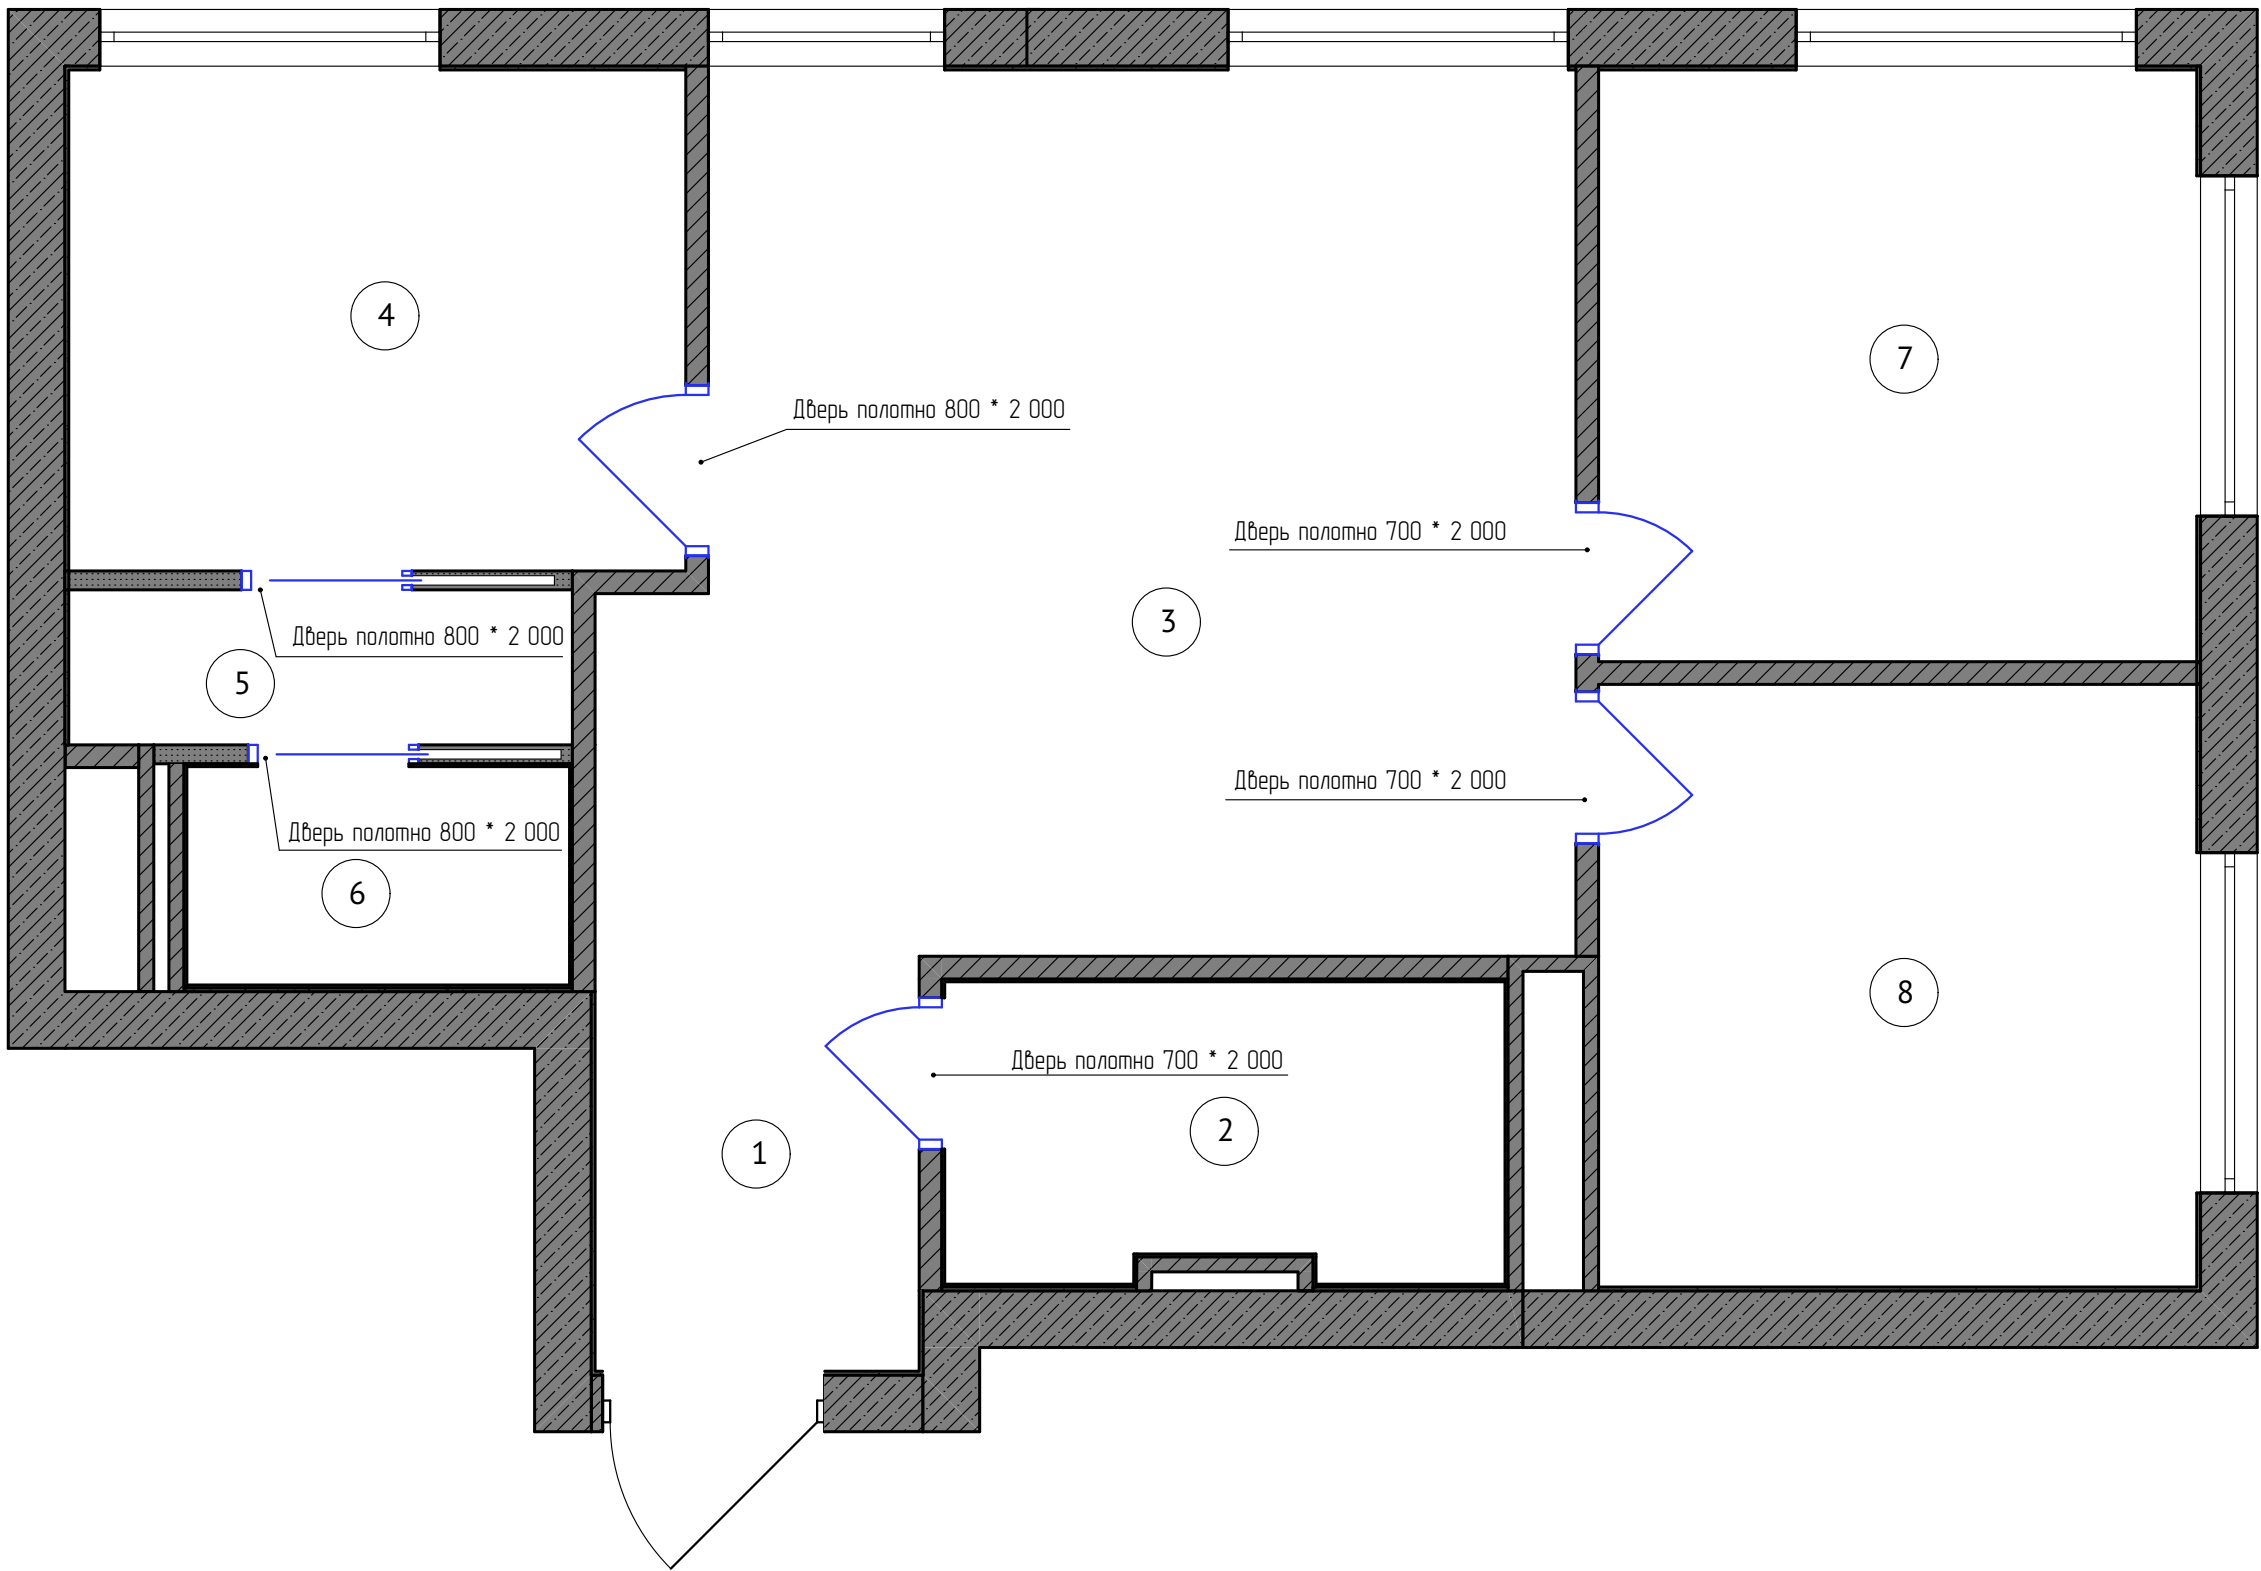

Экспликация помещений

№	Наименование	Площадь, кв.м.
1	Прихожая	3,77
2	Санузел	4,59
3	Кухня-Гостиная	22,73
4	Мастер спальня	8,69
5	Гардеробная	2,19
6	Мастер санузел	2,34
7	Детская 1	9,94
8	Детская 2	10,09
		64,34 м²

Дизайн проект			Подпись	Дата	Квартира Жк Кинетик	РАЗВЕРТКИ ПРИХОЖЕЙ	Стадия	Лист	Масштаб
	Разработал	Соколов Н.Е.					ДП	22	1:40
	Заказчик	Шувалова Е.Е.							



Дизайн проект

		Подпись	Дата	Квартира Жк Кинетик
Разработал	Соколов Н.Е.			
Заказчик	Шувалова Е.Е.			

ВИЗУАЛИЗАЦИЯ ПРИХОЖЕЙ

Стадия	Лист	Масштаб
ДП	23	1:40

Дизайн проект

		Подпись	Дата
Разработал	Соколов Н.Е.		
Заказчик	Шувалова Е.Е.		

Квартира
Жк Кинетик

РАЗВЕРТКИ САНУЗЛА

Стадия	Лист	Масштаб
ДП	24	1:40




Дизайн проект

		Подпись	Дата	Квартира Жк Кинетик
Разработал	Соколов Н.Е.			
Заказчик	Шувалова Е.Е.			

ВИЗУАЛИЗАЦИЯ САНУЗЛА

Стадия	Лист	Масштаб
ДП	25	1:40

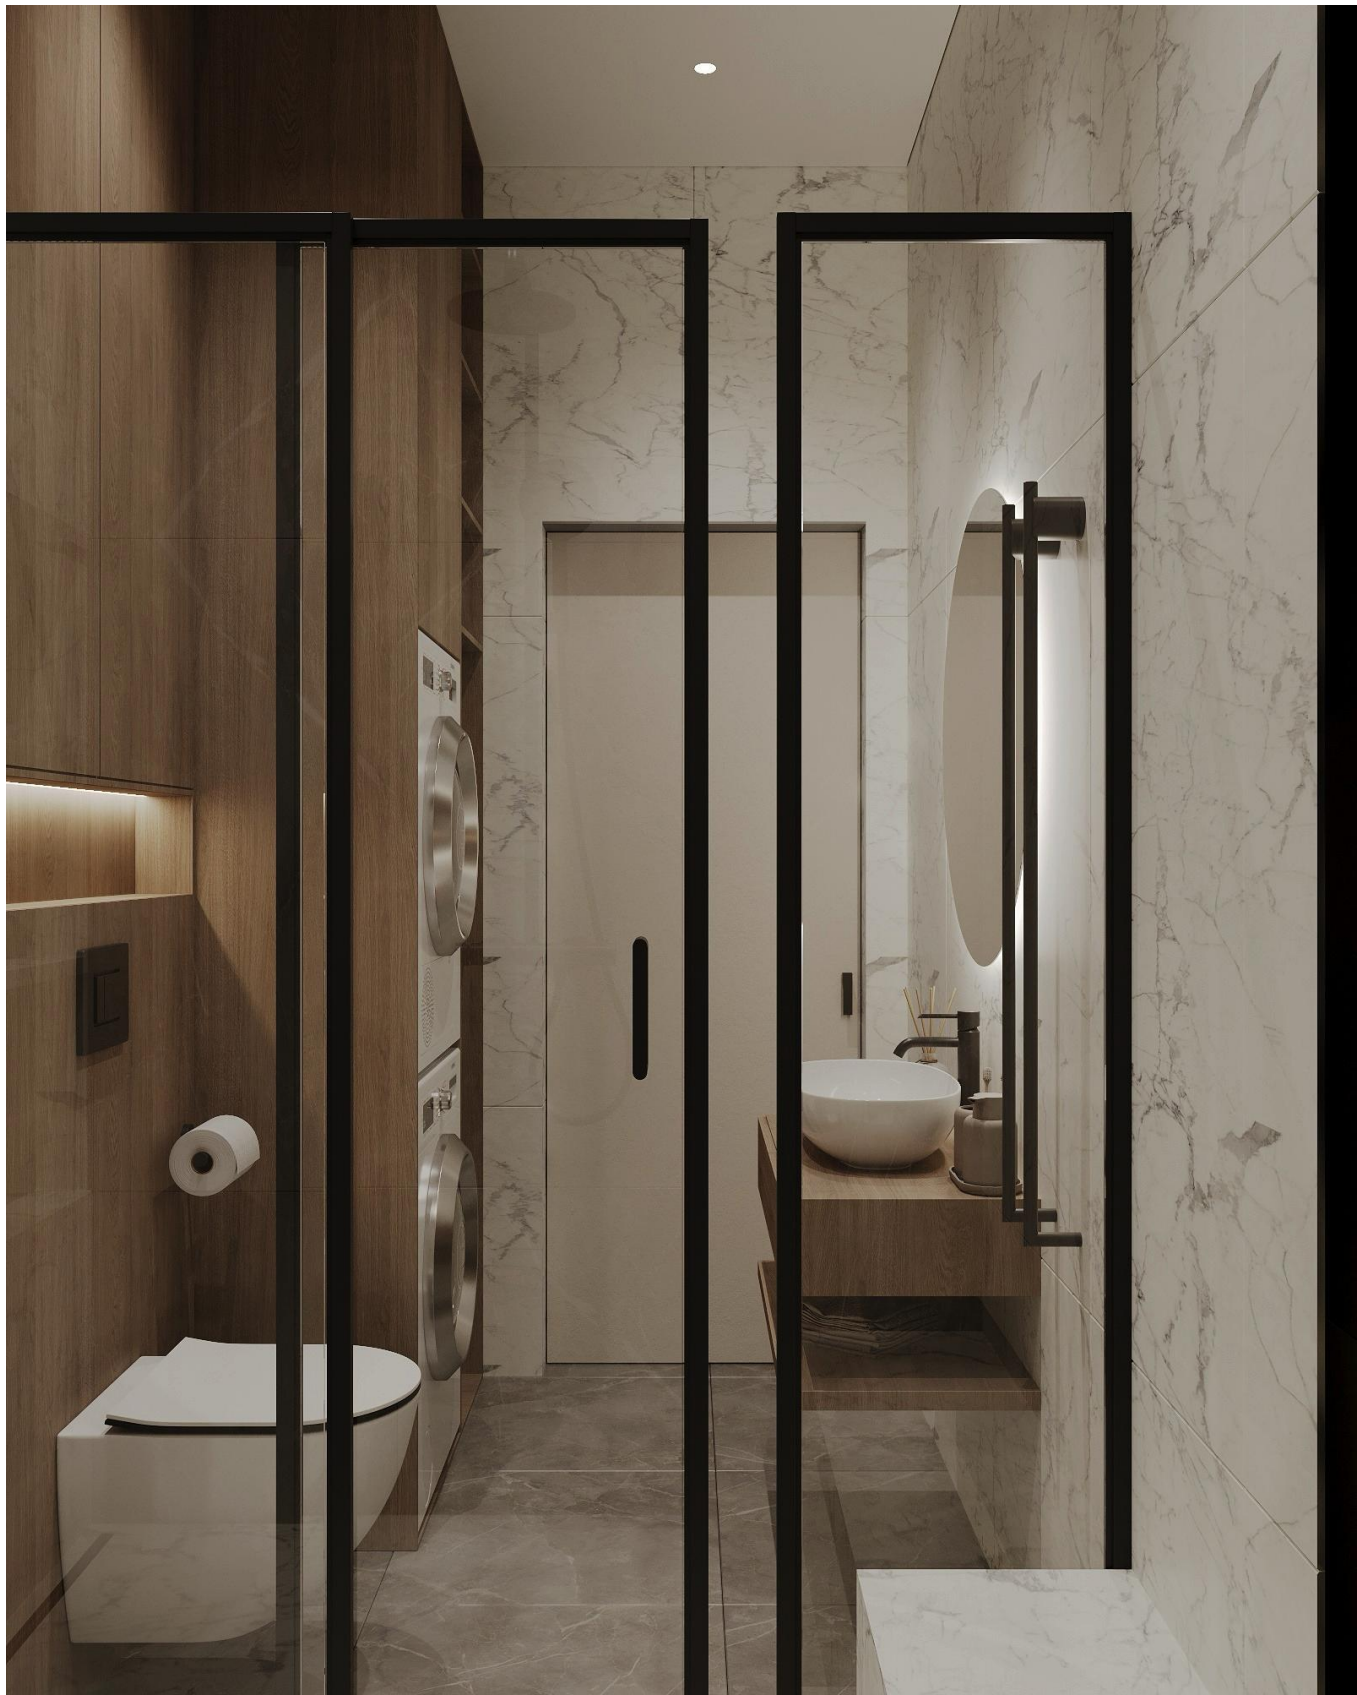

Дизайн проект

Разработал	Соколов Н.Е.	Подпись	Дата	Квартира Жк Кинетик
Заказчик	Шуфалова Е.Е.			

ВИЗУАЛІЗАЦІЯ САНУЗЛА

Стадия	Лист	Масштаб
ДП	26	1:40

Дизайн проект

		Подпись	Дата
Разработал	Соколов Н.Е.		
Заказчик	Шувалова Е.Е.		

Квартира
Жк Кинетик

РАЗВЕРТКИ КУХНИ

Стадия	Лист	Масштаб
ДП	27	1:40



Дизайн проект

		Подпись	Дата	Квартира Жк Кинетик
Разработал	Соколов Н.Е.			
Заказчик	Шувалова Е.Е.			

ВИЗУАЛИЗАЦИЯ КУХНИ

Стадия	Лист	Масштаб
ДП	28	1:40



Дизайн проект

		Подпись	Дата	Квартира Жк Кинетик
Разработал	Соколов Н.Е.			
Заказчик	Шувалова Е.Е.			

ВИЗУАЛИЗАЦИЯ КУХНИ

Стадия	Лист	Масштаб
ДП	29	1:40

Дизайн проект			Подпись	Дата	Квартира Жк Кинетик	РАЗВЕРТКИ ГОСТИНОЙ	Стадия	Лист	Масштаб
	Разработал	Соколов Н.Е.					ДП	30	1:40
	Заказчик	Шувалова Е.Е.							



Дизайн проект

Разработал Заказчик	Соколов Н.Е.	Подпись	Дата	Квартира Жк Кинетик	ВИЗУАЛИЗАЦИЯ ГОСТИНОЙ	Стадия	Лист	Масштаб
	Шувалова Е.Е.					ДП	31	1:40



Дизайн проект

		Подпись	Дата	Квартира Жк Кинетик
Разработал	Соколов Н.Е.			
Заказчик	Шувалова Е.Е.			

ВИЗУАЛИЗАЦИЯ ГОСТИНОЙ

Стадия	Лист	Масштаб
ДП	32	1:40



Дизайн проект

		Подпись	Дата	Квартира Жк Кинетик
Разработал	Соколов Н.Е.			
Заказчик	Шувалова Е.Е.			

ВИЗУАЛИЗАЦИЯ СТОЛОВОЙ

Стадия	Лист	Масштаб
ДП	33	1:40

Дизайн проект			Подпись	Дата	Квартира Жк Кинетик	РАЗВЕРТКИ МАСТЕР СПАЛЬНИ	Стадия	Лист	Масштаб
	Разработал	Соколов Н.Е.					ДП	34	1:40
	Заказчик	Шувалова Е.Е.							



Дизайн проект

		Підпис	Дата	Квартира Жк Кинетик
Розроботал	Соколов Н.Е.			
Заказчик	Шувалова Е.Е.			

ВИЗУАЛІЗАЦІЯ МАСТЕР СПАЛЬНИ

Стадия	Лист	Масштаб
ДП	35	1:40



Дизайн проект

		Підпись	Дата	Квартира Жк Кинетик
Разроботал	Соколов Н.Е.			
Заказчик	Шуфалова Е.Е.			

ВИЗУАЛІЗАЦІЯ МАСТЕР СПАЛЬНИ

Стадия	Лист	Масштаб
ДП	36	1:40

Дизайн проект			Подпись	Дата	Квартира Жк Кинетик	РАЗВЕРТКИ МАСТЕР САНУЗЛА	Стадия	Лист	Масштаб
	Разработал	Соколов Н.Е.					ДП	37	1:40
	Заказчик	Шувалова Е.Е.							



Дизайн проект

		Підпись	Дата	Квартира Жк Кинетик
Разроботал	Соколов Н.Е.			
Заказчик	Шуфалова Е.Е.			

ВИЗУАЛІЗАЦІЯ МАСТЕР САНУЗЛА

Стадия	Лист	Масштаб
ДП	38	1:40

Дизайн проект

		Подпись	Дата
Разработал	Соколов Н.Е.		
Заказчик	Шувалова Е.Е.		

Квартира
Жк Кинетик

РАЗВЕРТКИ ДЕТСКОЙ 1

Стадия	Лист	Масштаб
ДП	39	1:40



Дизайн проект

		Подпись	Дата	Квартира Жк Кинетик
Разработал	Соколов Н.Е.			
Заказчик	Шувалова Е.Е.			

ВИЗУАЛИЗАЦИЯ ДЕТСКОЙ 1

Стадия	Лист	Масштаб
ДП	40	1:40



Дизайн проект

		Подпись	Дата	Квартира Жк Кинетик
Разработал	Соколов Н.Е.			
Заказчик	Шуфалова Е.Е.			

ВИЗУАЛИЗАЦИЯ ДЕТСКОЙ 1

Стадия	Лист	Масштаб
ДП	41	1:40

Дизайн проект

		Подпись	Дата
Разработал	Соколов Н.Е.		
Заказчик	Шувалова Е.Е.		

Квартира
Жк Кинетик

РАЗВЕРТКИ ДЕТСКОЙ 2

Стадия	Лист	Масштаб
ДП	42	1:40



Дизайн проект

		Подпись	Дата	Квартира Жк Кинетик
Разработал	Соколов Н.Е.			
Заказчик	Шувалова Е.Е.			

ВИЗУАЛИЗАЦИЯ ДЕТСКОЙ 2

Стадия	Лист	Масштаб
ДП	43	1:40



Дизайн проект

		Подпись	Дата	Квартира Жк Кинетик
Разработал	Соколов Н.Е.			
Заказчик	Шувалова Е.Е.			

ВИЗУАЛИЗАЦИЯ ДЕТСКОЙ 2

Стадия	Лист	Масштаб
ДП	44	1:40